


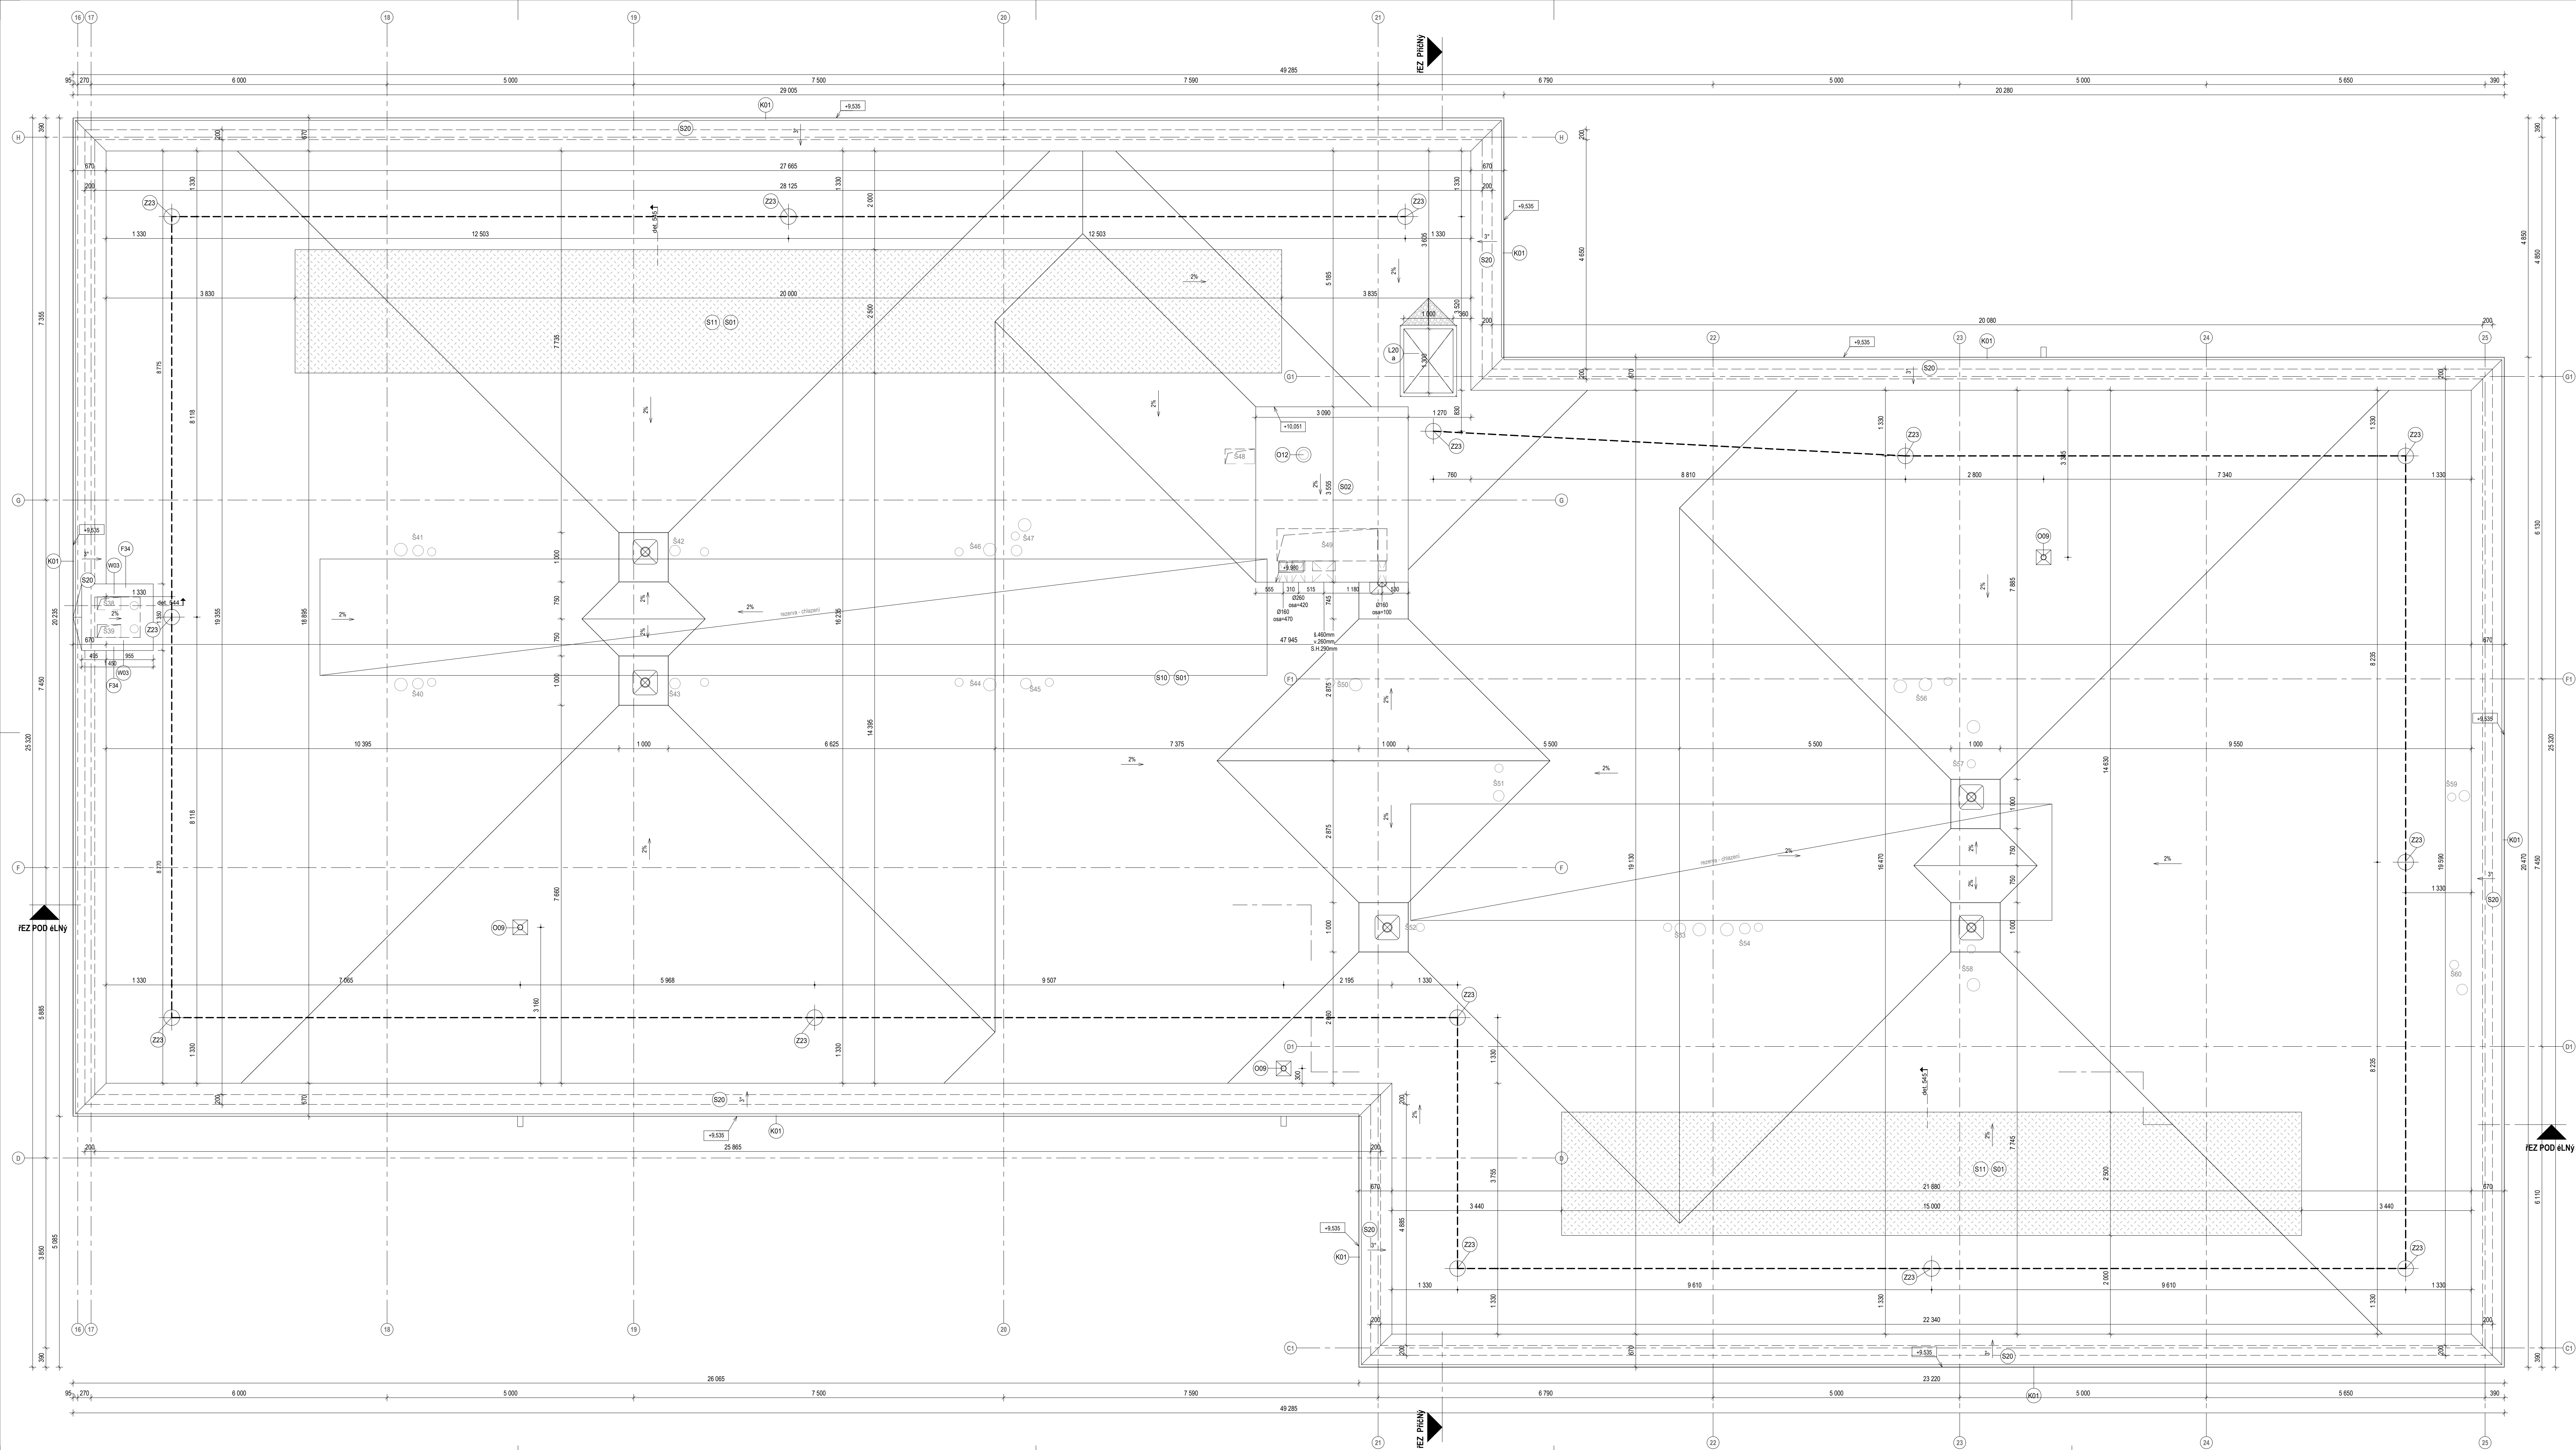


Schéma kótování:

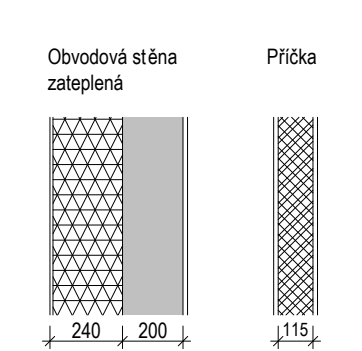

Legenda výrobků:

- L Okna
- D Dveře
- W Skladby stěn
- P Skladby podlah
- S Skladby střeš
- F Skladby fasád a zateplení
- C Skladby podlahy

Legenda materiálů:

- K Klenčíkové prvky
- Z Zateplené prvky
- U Truhlářské výrobky
- O Oskvěny prvky
- R Překážky
- Železobeton, nosné konstrukce
- Zdivo, keramické tělísko AKU 300 mm, nosné konstrukce
- Zdivo, keramické tělísko 250 mm, nosné konstrukce
- Zdivo, keramické tělísko, nenosné konstrukce
- Zdivo, betonové tělísko, nenosné konstrukce
- Zdivo, porobeton, instalační předstěny
- Tepelná izolace z expandovaného polystyrenu (EPS)
- Tepelná izolace z minerální vlny
- Tepelná izolace z tuhé fenolické pěny
- Tepelná izolace z extrudovaného polystyrenu (XPS)
- SDK podlahy / zateplení stropu
- Zemina stávající
- Zásep zeminou, subzbit
- Kačín

Poznámky:

- Dokumentace je vypracována ve stupni dokumentace pro provádění stavby (DPS). Není náhradou za dílenskou dokumentaci.
- Všechny prvky nosné konstrukce jsou dimenzovány v části D - 3. Dokumentace stavební konstrukcí to řešení.
- Všechny konstrukce a prvky budovy jsou řešeny podlažní na podlaží odlišné části D.4 - Podlaží bezpečnostní řešení (PBR). Styky konstrukcí budou upraveny dle příslušných norem a PBR.
- Všechny instalace, prvky a jejich detaily budou řešeny kompletním systémovým řešením s garancí dodavatele.
- Instalace šachty kvůli požární úsek spolu s bytem, ke kterému náleží. V rovné střeše upravení rozvodu systémovým upravením se zabráněním akustického přesahu.
- Keramické tělísko budou v kosených provedení do výšky po spodní hraně podlahy. Na samostatných WC budou přivešeny do výšky 1200 mm.
- Pod keramický obklad bude aplikována hydroizolační páska, v podlahě vždy pod keramickou dlažbou, a vyláčením min. 100 mm nad okrajem podlahy a na stěnu v místě sprchového koulu nebo vývěvy do výšky keramického obkladu. V rozích a koutech bude vždy použit systémový výztužný těsnicí pás dle technologického předpisu výrobce.
- Výkresová plocha místnosti je orientována a vypočtena po povrchu světelného průměru ohraničujících stěn.
- Stěny a stropní desky v řezu jsou kótovány bez omítky a obkladu - viz schéma kótování.
- Sálavé výšky v kutech obkladu 2,62 m, v místnostech s podhledem 2,4 m. Sálavé výšky ve společných chodbách 2,38 m.
- Před výrobou jednotlivých stavebních prvků je nutné ověřit skutečné rozměry v místě osazení na vybudované konstrukce.
- Rozměr stěny po obkladové zátěži bude určen dle konkrétního výrobce. Standardně o 50 mm vyšší a o 100 mm širší než požadovaný šel okraj dveří.
- Prostředky v menších konstrukcích nejsou v půdorysích zakreslovány.
- Dodávka prvků musí být vždy jako komplet, tzn. včetně kování, těsnění, pomocných konstrukcí apod.
- Při jakýchkoli nejasnostech nebo rozporů skutečností je nutné kontaktovat projektanta projektové dokumentace.
- Provedení výztužky stěly - postup dle detailu č. 540, rev. 01 ze dne 16.4.2025.

00	Vydání dokumentace	31.10.2025
01	Doplnění dokumentace - dle požadavků investora	6.2.2026
02	Okotování atiky	5.5.2026
Revize	Popis revize	Datum

sever

schéma

stavba

Na Mariánské cestě - 2. etapa

zpracovatel

DC DVA DVA

DC design, s.r.o.

Hanusova 347/16,
140 00 Praha 4
+420 724 320 976
proj@dc2.cz
www.dc2.cz

zodpovědný projektant

Ing. Libor Doležal

vypracoval

Ing. arch. Jiří Šebek
Ing. Karel Martinek

investor

DOMOPLAN a.s.
Třída Šatov, Brno, 602 00

generální projektant

BR engineering project s.r.o.
Hanusova 347/16,
140 00 Praha 4
info@brproject.cz

hlavní inženýr projektu

Ing. Libor Doležal

stavební objekt

SO03 - Bytový dům D2 a C2

část

D.1.1 - Architektonicko - stavební řešení

profesionál / členění část

01 - Stavební část

datum

rev 02 - 5.5.2026

číslo paré

A4

měřítko

1:50

zakázka

365

stupeň

50

s. objekt

SO03

část

D.1.1

č. výkresu

01

č. výkresu

105b

revize

02

± 0,000 = 224,62 m.n.m (BPV)

stavební objekt

SO03 - Bytový dům D2 a C2

část

D.1.1 - Architektonicko - stavební řešení

profesionál / členění část

01 - Stavební část

datum

rev 02 - 5.5.2026

číslo paré

A4

měřítko

1:50

zakázka

365

stupeň

50

s. objekt

SO03

část

D.1.1

č. výkresu

01

č. výkresu

105b

revize

02

Půdorys střechy - sekce C2