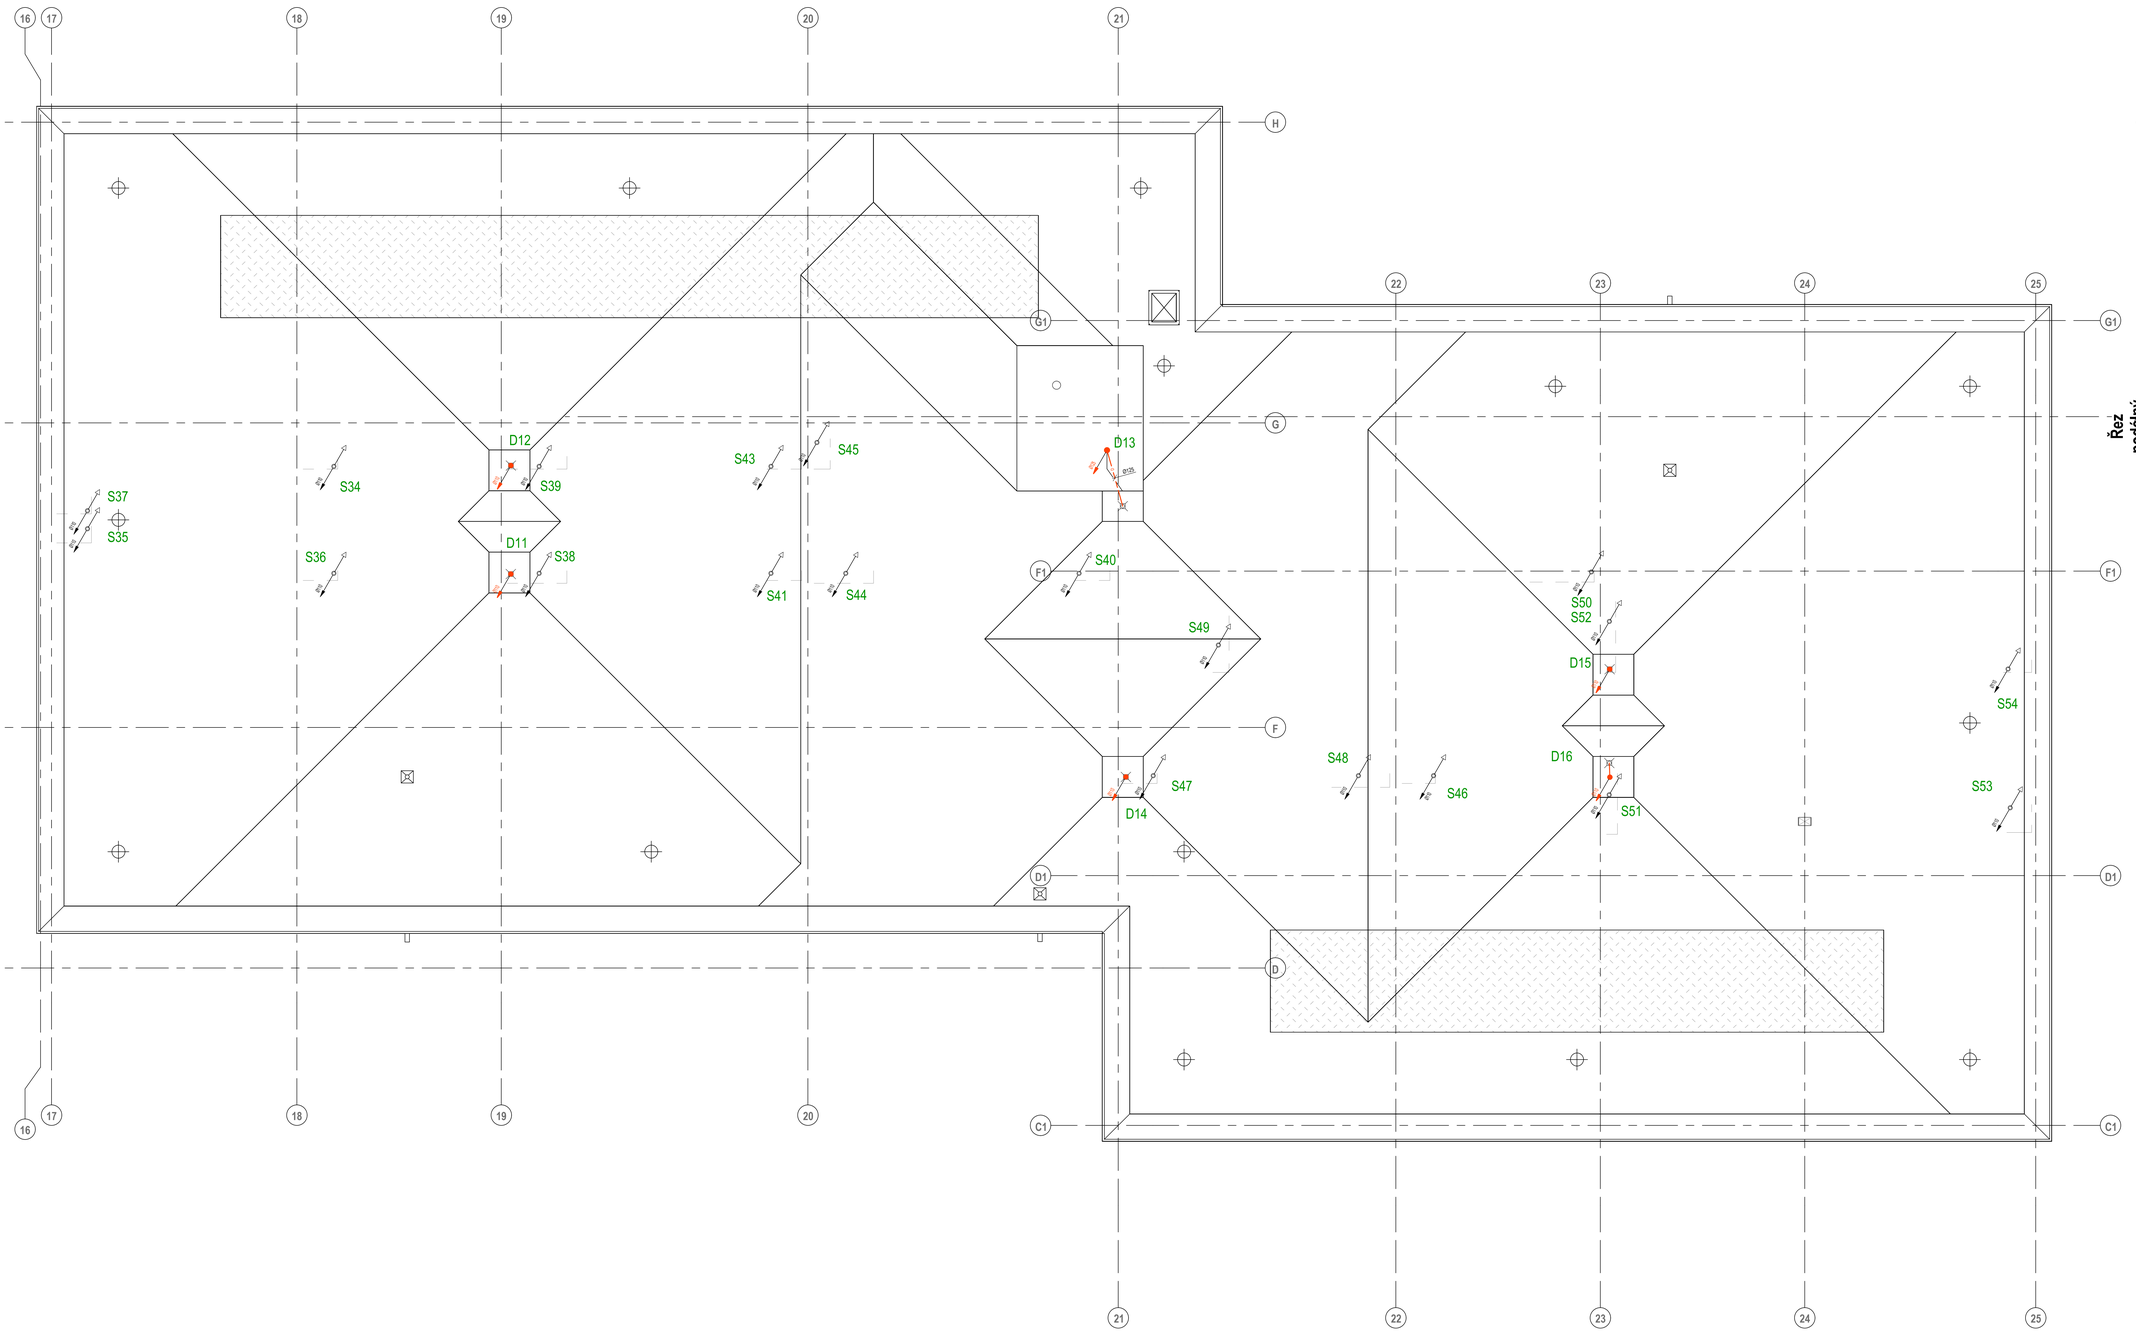

LEGENDA:

- SPLAŠKOVÁ KANALIZACE PŘIPOJOVACÍ POTRUBÍ (PP-HT)
- SPLAŠKOVÁ KANALIZACE POD STROPEM (PP-HT)
- SPLAŠKOVÁ KANALIZACE V PODLAZE (PP-HT)
- DEŠŤOVÁ KANALIZACE POD STROPEM (SVAŘOVANÉ PE, IZOLOVÁNO)
- DEŠŤOVÁ KANALIZACE V PODLAZE (SVAŘOVANÉ PE, IZOLOVÁNO)

Sx Dx

SVISLÝ ODPAD KANALIZACE
SPLAŠKOVÉ, DEŠŤOVÁ

LEGENDA zařizovacích předmětů

WC	ZÁVĚSNÝ KLOZET KERAMICKÝ BÍLÝ, SPLACHOVACÍ NÁDRŽKA VESTAVĚNÁ, OVLAD. DESTIČKA S TLAČÍTKEM, ROHOVÝ VENTIL 1/2" SOUČÁSTÍ NÁDRŽKY
U	UMYVADLO KERAMICKÉ UMYVADLOVÁ KERAMA 16 DESKU, SIFON UMYVADLOVÝ
	TRUBKOVÝ DN 40, SIFON UMYVADLOVÝ DN 40, UMYVADLOVÁ BATERIE STOJANKOVÁ PÁKOVÁ, 2x ROHOVÝ VENTIL S PŘÍPOJOVACÍ HADICÍ
D	KUCH. DŘEZ, SIFON DŘEZOVÝ DN40 S PŘEPADEM, BATERIE DŘEZOVÁ STOJANKOVÁ PÁKOVÁ, DŘEZ NENÍ SOUČÁSTÍ DODÁVKY ZTI
SK	SPRCHOVÝ KOUT SE ZASTĚNOU, SPRCHA HLAVOVÁ, SPRCHOVÁ BAT. PODOMÍTKOVÝ SET, SPRCHOVÝ ŽLÁBEK SE SIFONEM DN 50
V	VANA AKRYLÁTOVÁ, SIFON VANOVÝ DN 50 S PŘEPADEM, BATERIE VANOVÁ NÁSTĚNNÁ, SE SPRCHOVÝM SETEM
M	KUCHYŇSKÁ MYČKA PRAČKOVÝ SIFON HL400, PRAČKOVÝ KOHOUT 1/2" - KULOVÝ
AP+S	AUTOMATICKÁ PRAČKA + SUŠIČKA PRAČKOVÝ SIFON HL400.2, PRAČKOVÝ KOHOUT 1/2" - KULOVÝ
VL	VTLEVKA KERAMICKÁ STACIONÁRNÍ NEBO ZÁVĚSNÁ, BATERIE VTLEVKOVÁ NÁSTĚNNÁ PÁKOVÁ
G	PODLAHOVÁ VPUST - např. HL310NPr se svislým odtokem nebo HL310NPr-h vodorovným odtokem a přídavnou suchou uzávěrkou

POZNÁMKA: SPECIFIKACE ZAŘIZOVACÍCH PŘEDMĚTŮ PRO GASTRO PROVOZ VIZ PD GASTRO
PŘESNÁ SPECIFIKACE OSTATNÍCH ZAŘIZOVACÍCH PŘEDMĚTŮ DLE INVESTORA A ARCHITEKTA.

Revize	Popis revize	Datum

± 0,000 = 224,62 m.n.m (BPV)

soverka

stavba
BD Na Mariánské cestě - 2. etapa

stupeň
Dokumentace pro provádění stavby

zpracovatel
vodopro
Ing. Pavel Jakubů
Hranická 107, 468 11
Janov nad Nisou

zodpovědný projektant
Ing. Pavel Jakubů

vypracoval
Ing. Sandra Nevímová
Daria Tombegr

stavební objekt
SO03 - Bytový dům D2 a C2

část
D.1.2.2 - Zdravotně technické instalace

profesní díl / členění části
02 - Zdravotně technické instalace - KANALIZACE

investor
DOMOPLAN a.s.
Trnitá 543/16, Brno, 602 00

generální projektant
BK engineering project s.r.o.
Hanusova 347/16
160 00 Praha 4
info@bkproject.cz

datum
10/2025

číslo paré

18 x A4

měřítko
1:50

hlavní inženýr projektu
Ing. Libor Doležal

PŮDORYS STŘECHY - OBJEKT C2	zakázka	stupeň	s.objekt	část	členění	č. výkresu	revize
	365	50	SO03	D.1.2.2	02	007b	