


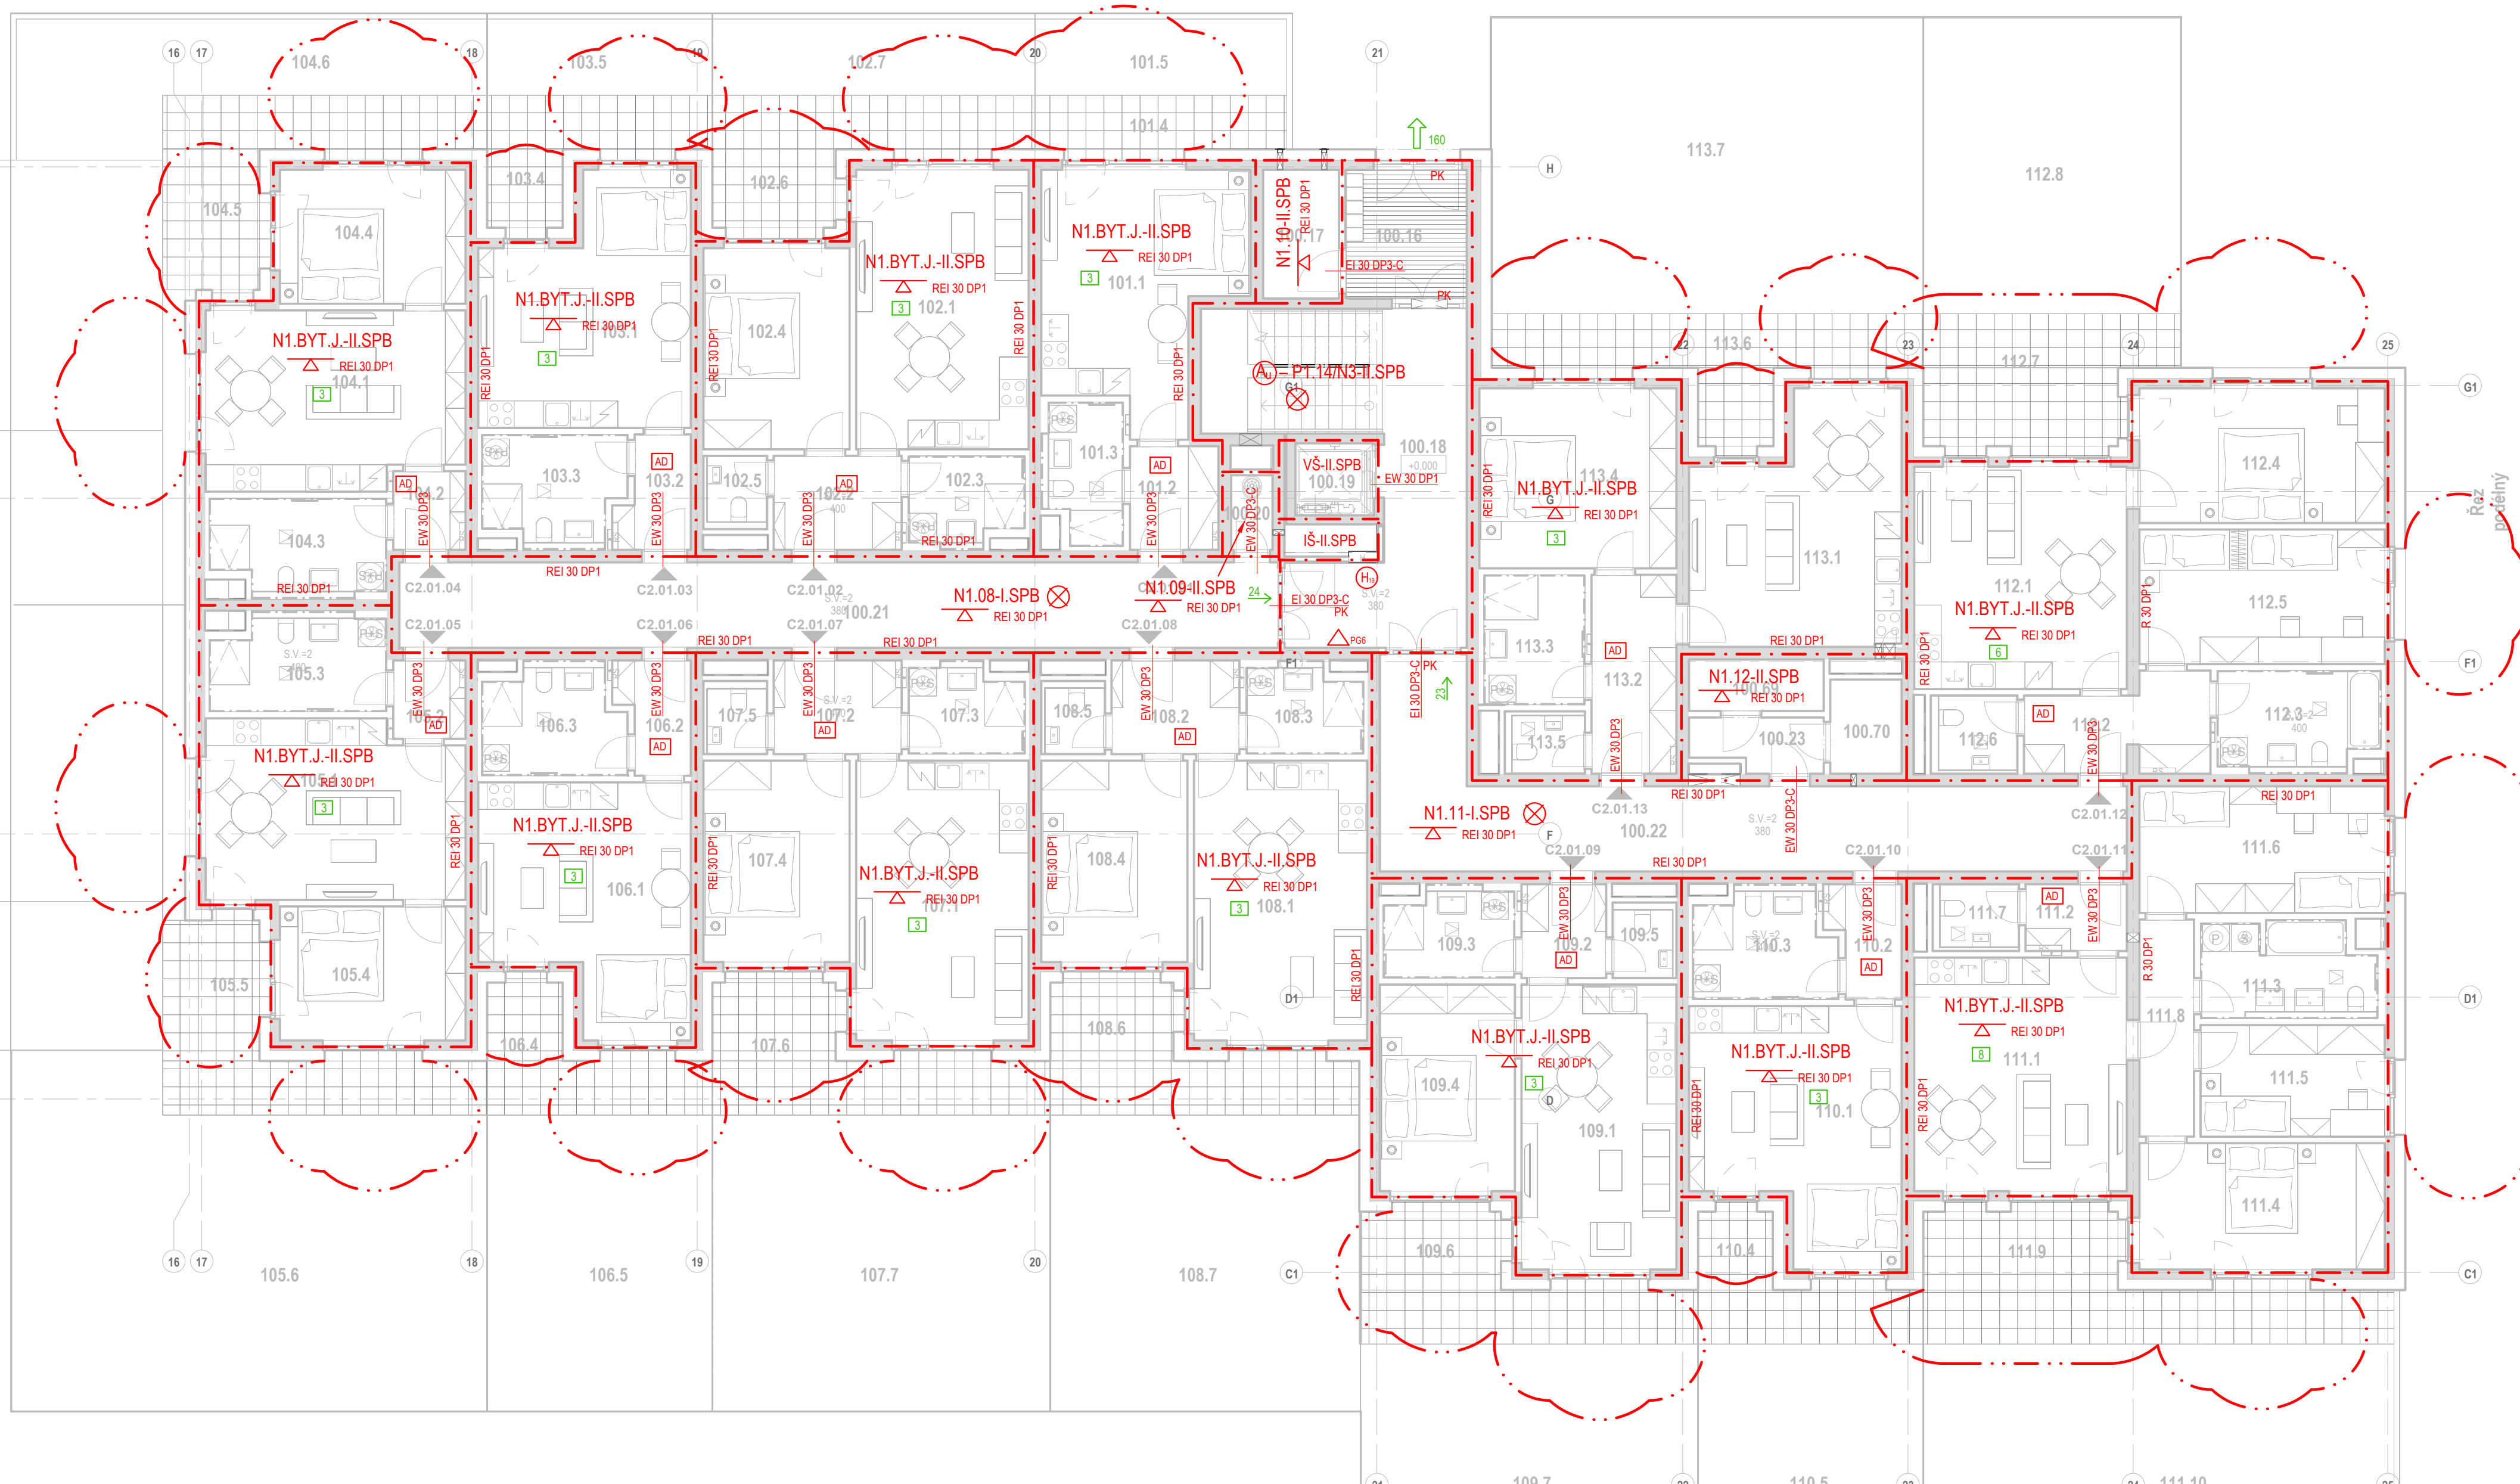

- ### POZNÁMKY:
- Požadovaná PO konstrukcí chránících instalaci a vytákové šachty (JŠ, VŠ) je EI 30 DP1, pokud není uvedeno jinak
 - Požadovaná PO užitelné instalací šachet je EW 30 DP1 a EI 30 DP1-S200, pokud užitelný ústí do CHÚC
 - Instalční šachty v byt. jednotkách jsou součástí PÚ byt. jednotek a musí být požárně přechýleny. PO min. EI 30 DP1