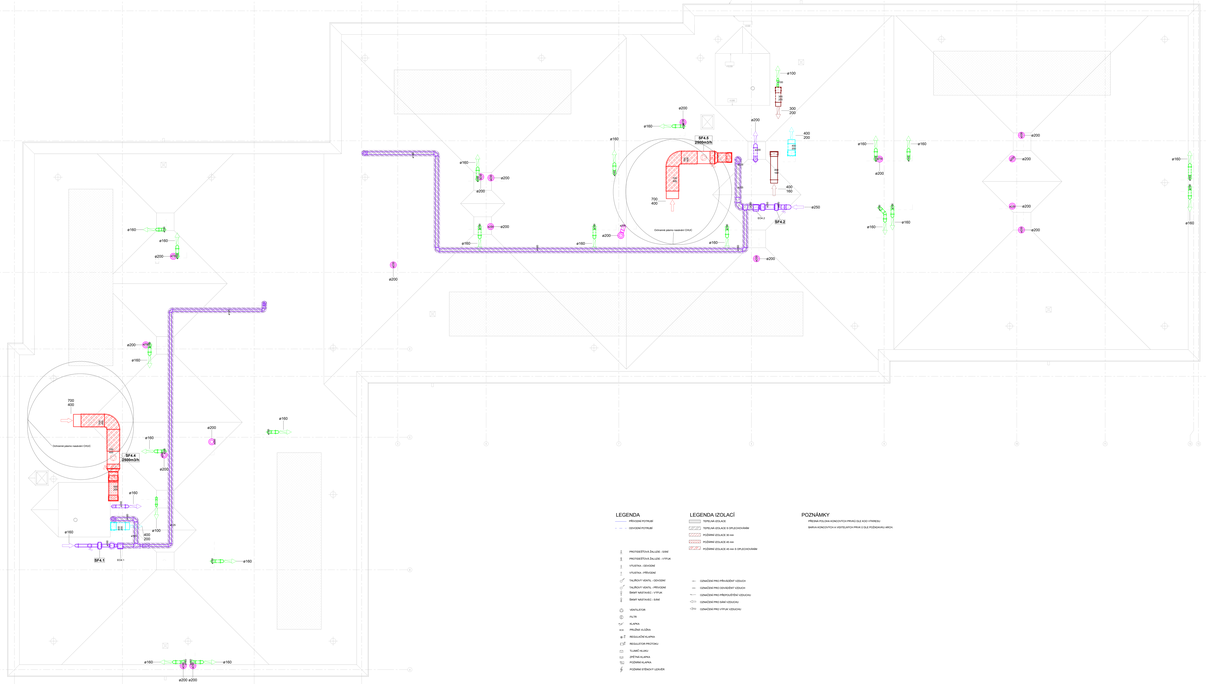

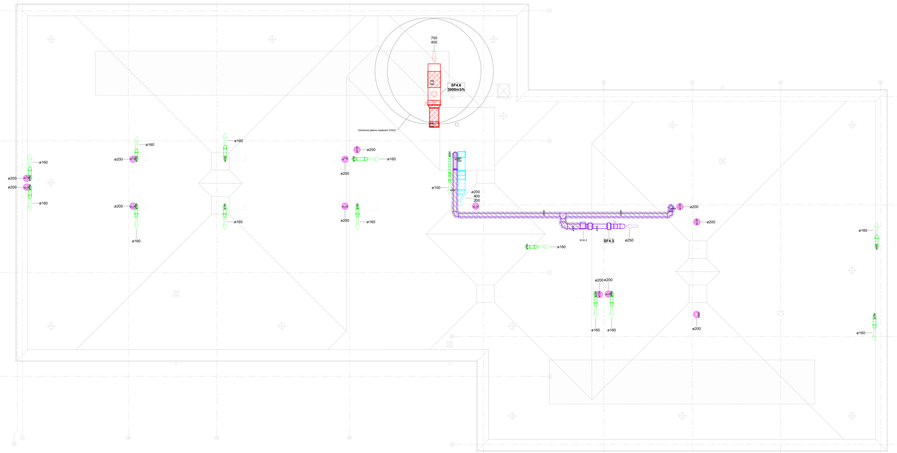

LEGENDA

- PŘÍVODNÍ POTRUBÍ
- ODVODNÍ POTRUBÍ

1. PROTIDEŠŤOVÁ ŽALUZIE - SANÍ
2. PROTIDEŠŤOVÁ ŽALUZIE - VÝFUK
3. VÝUSTKA - SÁNÍ/ANI
4. VÝUSTKA - PŘÍVOD/ANI
5. TALÍŘOVÝ VENTIL - SÁNÍ/ANI
6. TALÍŘOVÝ VENTIL - PŘÍVOD/ANI
7. BRAM MAGYAR/EU - VÝFUK
8. BRAM MAGYAR/EU - SÁNÍ

- AKUMULÁTOR
- FILTR
- KLAPKA
- PRUŽNÁ VLOŽKA
- REGULAČNÍ KLAPKA
- REGULÁTOR PRŮTOKU
- TLUMIČ HLUKU
- ZPĚTNÁ KLAPKA
- POŽÁRNÍ KLAPKA
- POŽÁRNÍ ID DŮLEŽITÝ UZAVĚR

LEGENDA IZOLACÍ

- TEPELNÁ IZOLACE
- TEPELNÁ IZOLACE S DIFUZNÍ BARIÉROU
- POŽÁRNÍ IZOLACE 30 min
- POŽÁRNÍ IZOLACE 60 min
- POŽÁRNÍ IZOLACE 30 min S DIFUZNÍ BARIÉROU

- OZNAČENÍ PRO PRŮMĚRNÝ VZDUCH
- OZNAČENÍ PRO MAXIMÁLNÍ VZDUCH
- OZNAČENÍ PRO PŘEPOUŠTĚNÝ VZDUCH
- OZNAČENÍ PRO MIN VZDUCHU
- OZNAČENÍ PRO VÝFUK VZDUCHU

POZNÁMKY

PŘESNÁ POLOHA KONCOVÝCH PRVKŮ DLE ROZV.VYKRESU
MAXIMÁLNÍ RYCHLOST VZDUCHU V POTRUBÍ PRO VŠECHNY MÍSTNOSTI

Revize | Popis revize | Datum

1:100 / 1:50 (A1) m.m. (BPV)

Akce
BD Na Mariánské cestě - 2. etapa

Investor
YTZB DESIGN
Na Valentince 1
150 00 Praha 5 - Smíchov
tel.: 602 123 456
e-mail: info@ytzb.cz
www.ytzb.cz

Autor
Ing. Martin Hejtmar
tel.: 602 123 456
e-mail: info@ytzb.cz

Hlavní projektant
Ing. Jiří Hejtmar

Projektant
Ing. Martin Hejtmar

Stupeň
Dokumentace pro provádění stavby

Obsah stupně
B.03 - Bytový dům SO 4.2

Název
D.1.2 - Technika prostředí staveb

Jméno výkresu
03 - Půdorys střechy

Měřítko
1:50

Datum
12/2025

Formát
A1

Číslo
005

Počet listů
1

Půdorys střechy

stavba	stupeň	objekt	část	druh	profese	číslo
365	00	SO03	D.1.2	03		005