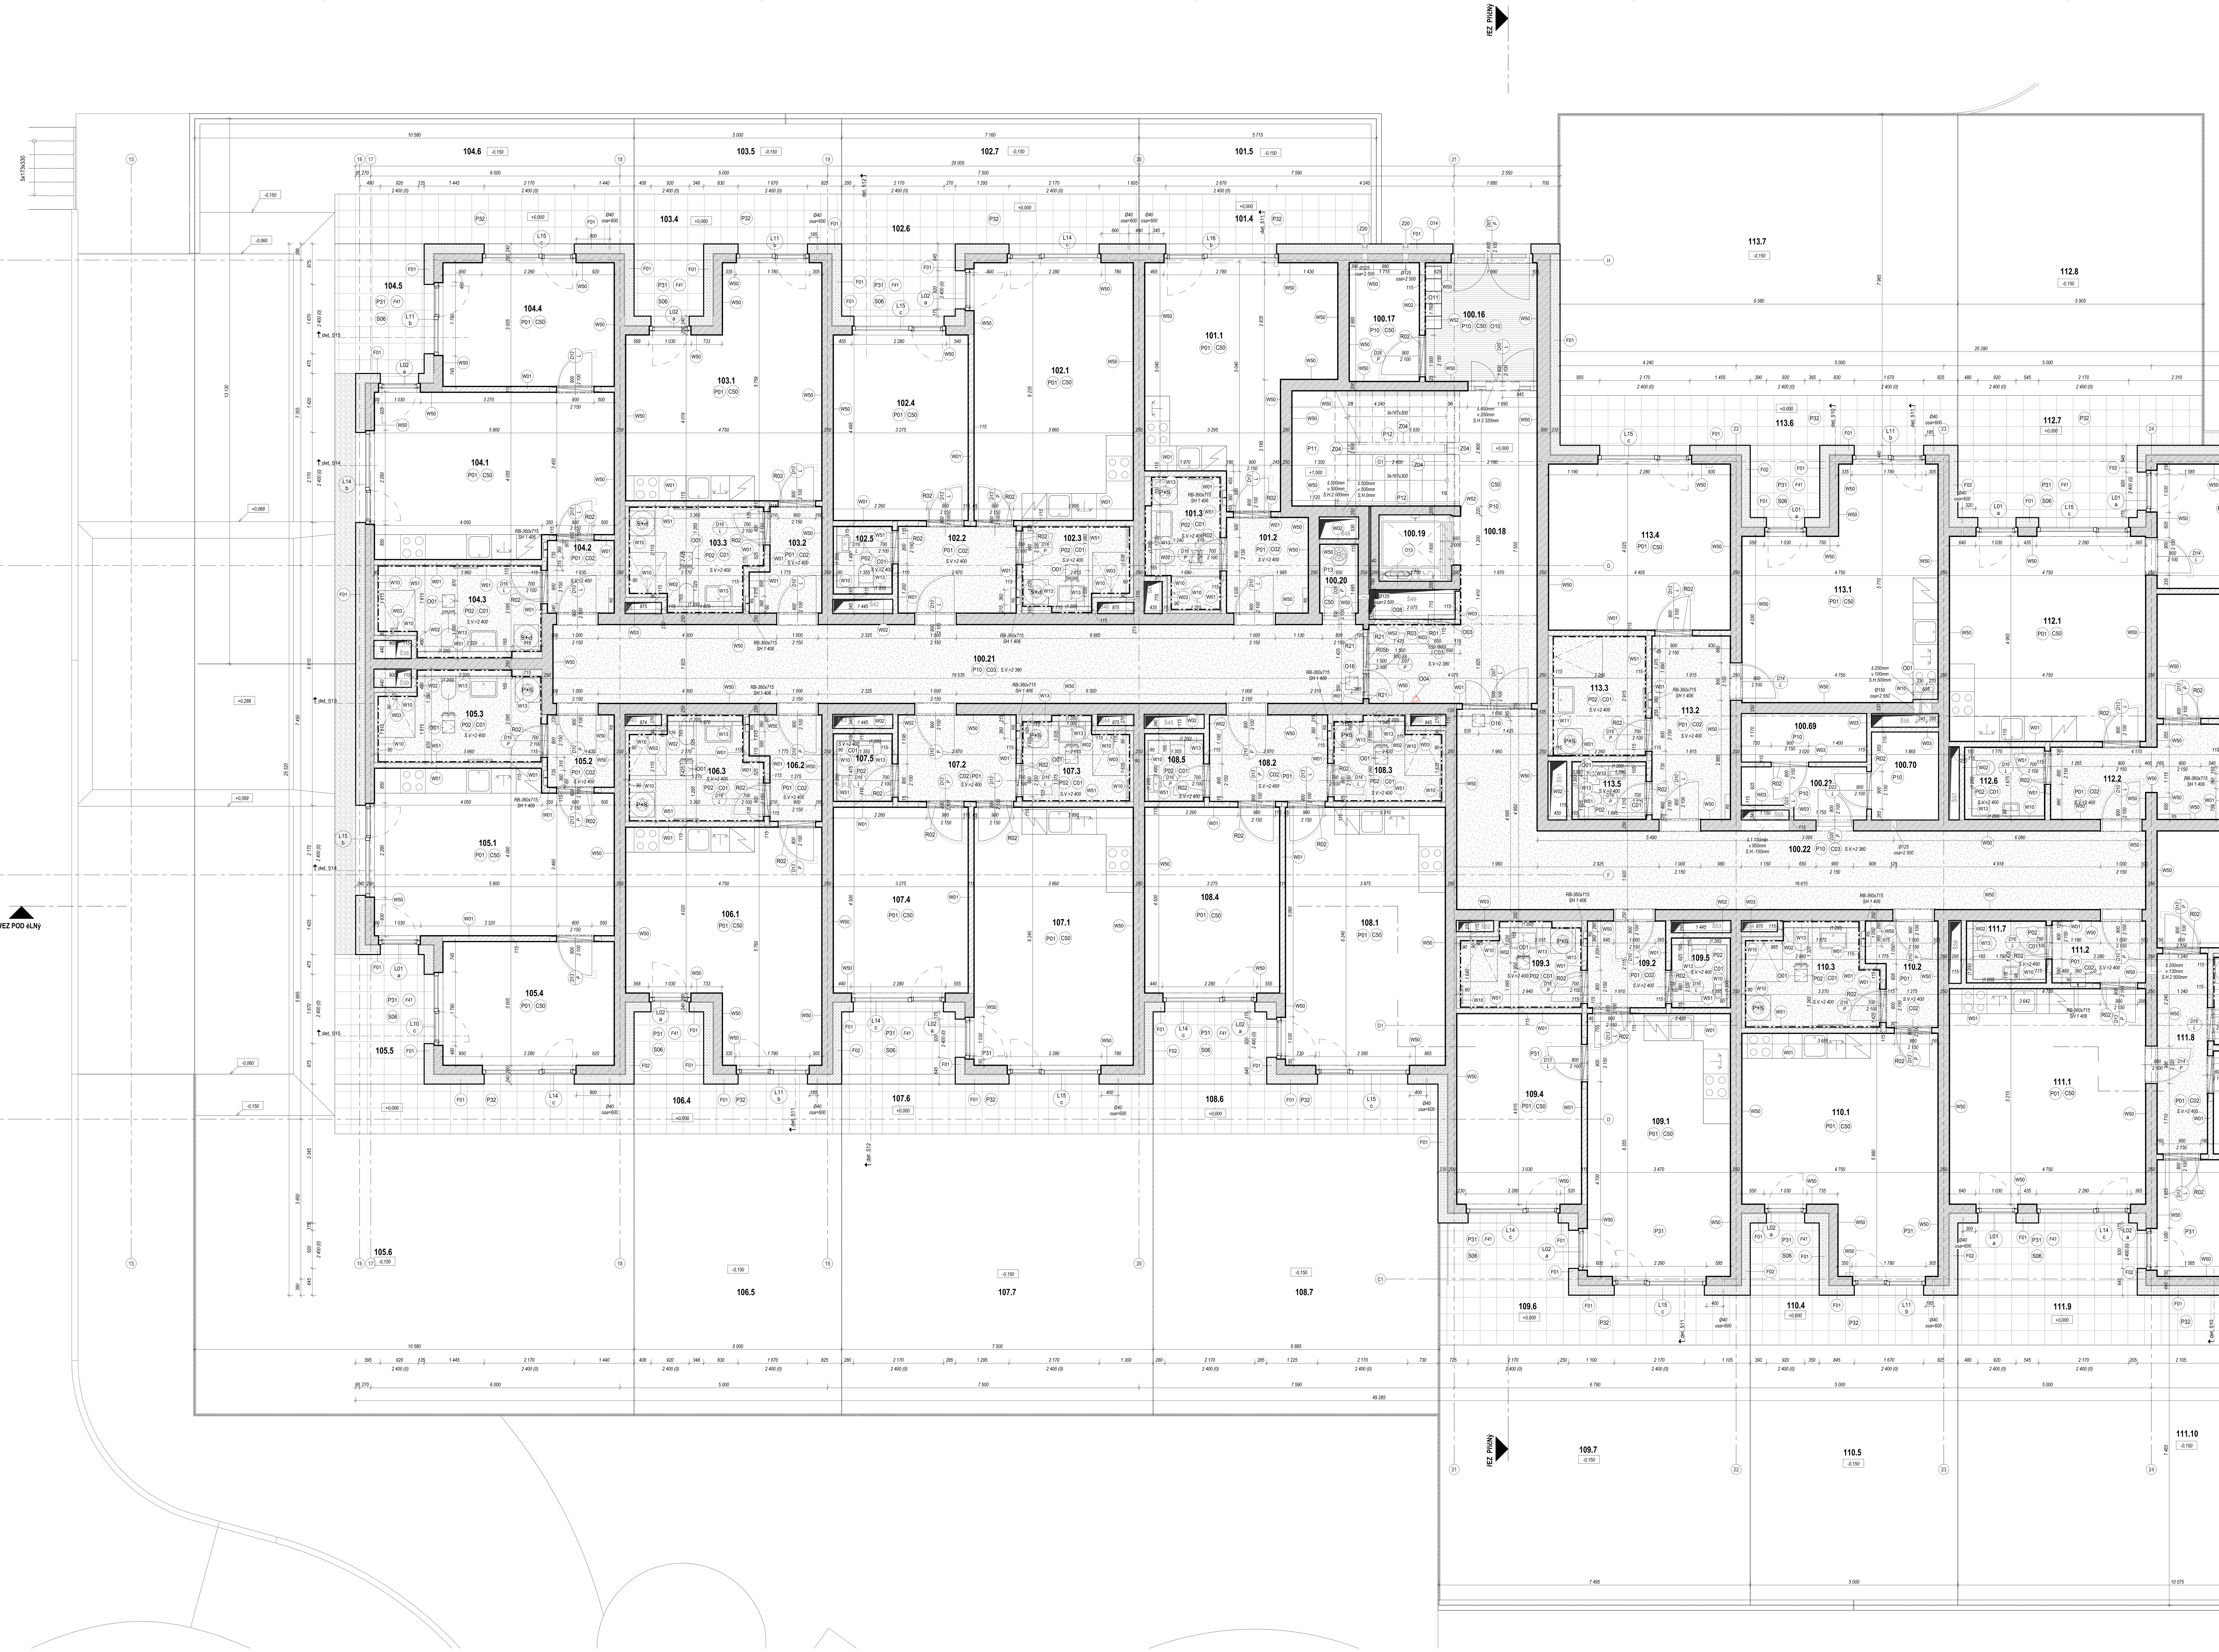

Místnosti 1NP - sekce C2

Číslo	Název	Povrchové úpravy – Podlaha	Povrchové úpravy – Stěny	Povrchové úpravy – Strop	Výška místnosti [m]	Plocha [m2]
100.69	Sklep	keramická dlažba, P10	výmalba, W03	výmalba, -	2,62	3,53
100.70	Sklep	keramická dlažba, P10	výmalba, W03	výmalba, -	2,62	3,42
						6,96
100.16	Zádveří	keramická dlažba, P10	výmalba, W50/W52	výmalba, C50	2,62	7,67
100.17	Kočárkárna	keramická dlažba, P10	výmalba, W50	výmalba, C50	2,62	4,81
100.18	Schodiště	keramická dlažba, P10	výmalba, C50	výmalba, W50/W52	2,38-2,62	29,25
100.19	Výtah	protiolejový nátěr, P22	uzavírací transparentní nátěr, -	uzavírací transparentní nátěr, -	-	2,80
100.20	Úklid	keramická dlažba, P13	omyvatelný nátěr, W02	výmalba, C50	2,62	1,52
100.21	Chodba	keramická dlažba, P10	výmalba, W50	výmalba, C03	2,38	36,96
100.22	Chodba	keramická dlažba, P10	výmalba, W50	výmalba, C03	2,38	37,00
100.23	Chodba	keramická dlažba, P10	výmalba, W03	výmalba, -	2,62	3,42
						123,42
C2.01.00 - Společné prostory						130,38
101.1	Obývací pokoj + kk	vinylová podlaha, P01	výmalba, W50	výmalba, C50	2,62	21,50
101.2	Předsíň	vinylová podlaha, P01	výmalba, W50	výmalba, C02	2,40	4,52
101.3	Koupelna	keramická dlažba, P02	keramický obklad, W51	výmalba, C01	2,40	4,84
						30,85
101.4	Terasa	keramická dlažba, P31	fasádní probarvená omítka, F01	-	-	6,71
101.5	Přezahrádka	zahradní substrát, -	-	-	-	9,45
						16,16
C2.01.01						47,01
102.1	Obývací pokoj + kk	vinylová podlaha, P01	výmalba, W50	výmalba, C50	2,62	23,76
102.2	Předsíň	vinylová podlaha, P01	výmalba, W50	výmalba, C02	2,40	5,92
102.3	Koupelna	keramická dlažba, P02	keramický obklad, W51	výmalba, C01	2,40	4,80
102.4	Pokoj	vinylová podlaha, P01	výmalba, W50	výmalba, C50	2,62	14,49
102.5	WC	keramická dlažba, P02	keramický obklad/výmalba, W51/W50	výmalba, C01	2,40	2,28
						51,25
102.6	Terasa	keramická dlažba, P31	fasádní probarvená omítka, F01	fasádní probarvená omítka, F41	2,65	13,35
102.7	Přezahrádka	zahradní substrát, -	-	-	-	12,10
						25,45
C2.01.02						76,70

Místnosti 1NP - sekce C2

Číslo	Název	Povrchové úpravy – Podlaha	Povrchové úpravy – Stěny	Povrchové úpravy – Strop	Výška místnosti [m]	Plocha [m2]
103.1	Obývací pokoj + kk	vinylová podlaha, P01	výmalba, W50	výmalba, C50	2,62	22,99
103.2	Předsíň	vinylová podlaha, P01	výmalba, W50	výmalba, C02	2,40	3,68
103.3	Koupelna	keramická dlažba, P02	keramický obklad, W51	výmalba, C01	2,40	7,23
						33,91
103.4	Terasa	keramická dlažba, P31	fasádní probarvená omítka, F01	fasádní probarvená omítka, F41	2,65	8,91
103.5	Přezahrádka	zahradní substrát, -	-	-	-	8,45
						17,36
C2.01.03						51,27
104.1	Obývací pokoj + kk	vinylová podlaha, P01	výmalba, W50	výmalba, C50	2,62	22,17
104.2	Předsíň	vinylová podlaha, P01	výmalba, W50	výmalba, C02	2,40	2,80
104.3	Koupelna	keramická dlažba, P02	keramický obklad, W51	výmalba, C01	2,40	7,99
104.4	Pokoj	vinylová podlaha, P01	výmalba, W50	výmalba, C50	2,62	12,26
						45,22
104.5	Terasa	keramická dlažba, P31	fasádní probarvená omítka, F01	fasádní probarvená omítka, F41	2,65	15,35
104.6	Přezahrádka	zahradní substrát, -	-	-	-	59,17
						74,53
C2.01.04						119,74
105.1	Obývací pokoj + kk	vinylová podlaha, P01	výmalba, W50	výmalba, C50	2,62	22,20
105.2	Předsíň	vinylová podlaha, P01	výmalba, W50	výmalba, C02	2,40	2,79
105.3	Koupelna	keramická dlažba, P02	keramický obklad, W51	výmalba, C01	2,40	7,99
105.4	Pokoj	vinylová podlaha, P01	výmalba, W50	výmalba, C50	2,62	12,26
						45,24
105.5	Terasa	keramická dlažba, P31	fasádní probarvená omítka, F01	fasádní probarvená omítka, F41	2,65	13,19
105.6	Přezahrádka	zahradní substrát, -	-	-	-	115,18
						128,37
C2.01.05						173,61
106.1	Obývací pokoj + kk	vinylová podlaha, P01	výmalba, W50	výmalba, C50	2,62	22,99
106.2	Předsíň	vinylová podlaha, P01	výmalba, W50	výmalba, C02	2,40	3,68
106.3	Koupelna	keramická dlažba, P02	keramický obklad, W51	výmalba, C01	2,40	7,23
						33,91
106.4	Terasa	keramická dlažba, P31	fasádní probarvená omítka, F01	fasádní probarvená omítka, F41	2,65	8,91
106.5	Přezahrádka	zahradní substrát, -	-	-	-	33,70
						42,61
C2.01.06						76,52
107.1	Obývací pokoj + kk	vinylová podlaha, P01	výmalba, W50	výmalba, C50	2,62	23,79
107.2	Předsíň	vinylová podlaha, P01	výmalba, W50	výmalba, C02	2,40	5,91
107.3	Koupelna	keramická dlažba, P02	keramický obklad, W51	výmalba, C01	2,40	4,79
107.4	Pokoj	vinylová podlaha, P01	výmalba, W50	výmalba, C50	2,62	14,51
107.5	WC	keramická dlažba, P02	keramický obklad/výmalba, W51/W50	výmalba, C01	2,40	2,28
						51,27
107.6	Terasa	keramická dlažba, P31	fasádní probarvená omítka, F01	fasádní probarvená omítka, F41	2,65	13,76
107.7	Přezahrádka	zahradní substrát, -	-	-	-	50,55
						64,31
C2.01.07						115,58
108.1	Obývací pokoj + kk	vinylová podlaha, P01	výmalba, W50	výmalba, C50	2,62	23,88
108.2	Předsíň	vinylová podlaha, P01	výmalba, W50	výmalba, C02	2,40	5,91
108.3	Koupelna	keramická dlažba, P02	keramický obklad, W51	výmalba, C01	2,40	4,83
108.4	Pokoj	vinylová podlaha, P01	výmalba, W50	výmalba, C50	2,62	14,51
108.5	WC	keramická dlažba, P02	keramický obklad/výmalba, W51/W50	výmalba, C01	2,40	2,26
						51,38
108.6	Terasa	keramická dlažba, P31	fasádní probarvená omítka, F01	fasádní probarvená omítka, F41	2,65	12,99
108.7	Přezahrádka	zahradní substrát, -	-	-	-	46,24
						59,23
C2.01.08						110,61
109.1	Obývací pokoj + kk	vinylová podlaha, P01	výmalba, W50	výmalba, C50	2,62	21,76
109.2	Předsíň	vinylová podlaha, P01	výmalba, W50	výmalba, C02	2,40	3,92
109.3	Koupelna	keramická dlažba, P02	keramický obklad, W51	výmalba, C01	2,40	5,46
109.4	Pokoj	vinylová podlaha, P01	výmalba, W50	výmalba, C50	2,62	13,76
109.5	WC	keramická dlažba, P02	keramický obklad/výmalba, W51/W50	výmalba, C01	2,40	2,35
						47,25
109.6	Terasa	keramická dlažba, P31	fasádní probarvená omítka, F01	fasádní probarvená omítka, F41	2,65	14,50
109.7	Přezahrádka	zahradní substrát, -	-	-	-	46,17
						60,67
C2.01.09						107,92
110.1	Obývací pokoj + kk	vinylová podlaha, P01	výmalba, W50	výmalba, C50	2,62	23,58
110.2	Předsíň	vinylová podlaha, P01	výmalba, W50	výmalba, C02	2,40	3,70
110.3	Koupelna	keramická dlažba, P02	keramický obklad, W51	výmalba, C01	2,40	7,22
						34,50
110.4	Terasa	keramická dlažba, P31	fasádní probarvená omítka, F01	fasádní probarvená omítka, F41	2,65	8,89
110.5	Přezahrádka	zahradní substrát, -	-	-	-	30,70
						39,59
C2.01.10						74,09
111.1	Obývací pokoj + kk	vinylová podlaha, P01	výmalba, W50	výmalba, C50	2,62	24,47
111.2	Předsíň	vinylová podlaha, P01	výmalba, W50	výmalba, C02	2,40	3,34
111.3	Koupelna	keramická dlažba, P02	keramický obklad, W51	výmalba, C01	2,40	7,34
111.4	Pokoj	vinylová podlaha, P01	výmalba, W50	výmalba, C50	2,62	15,27
111.5	Pokoj	vinylová podlaha, P01	výmalba, W50	výmalba, C50	2,62	10,12
111.6	Pokoj	vinylová podlaha, P01	výmalba, W50	výmalba, C50	2,62	15,30
111.7	WC	keramická dlažba, P02	keramický obklad/výmalba, W51/W50	výmalba, C01	2,40	2,39
111.8	Chodba	vinylová podlaha, P01	výmalba, W50/W01	výmalba, C02	2,40	5,83
						84,08
111.9	Terasa	keramická dlažba, P31	fasádní probarvená omítka, F01	fasádní probarvená omítka, F41	2,65	20,06
111.10	Přezahrádka	zahradní substrát, -	-	-	-	64,16
						84,22
C2.01.11						168,30
112.1	Obývací pokoj + kk	vinylová podlaha, P01	výmalba, W50	výmalba, C50	2,62	23,29
112.2	Předsíň	vinylová podlaha, P01	výmalba, W50	výmalba, C02	2,40	7,88
112.3	Koupelna	keramická dlažba, P02	keramický obklad, W51	výmalba, C01	2,40	7,79
112.4	Pokoj	vinylová podlaha, P01	výmalba, W50	výmalba, C50	2,62	16,28
112.5	Pokoj	vinylová podlaha, P01	výmalba, W50	výmalba, C50	2,62	16,25
112.6	WC	keramická dlažba, P02	keramický obklad/výmalba, W51/W50	výmalba, C01	2,40	3,32
						74,81
112.7	Terasa	keramická dlažba, P31	fasádní probarvená omítka, F01	fasádní probarvená omítka, F41	2,65	14,57
112.8	Přezahrádka	zahradní substrát, -	-	-	-	39,63
						54,20
C2.01.12						129,01
113.1	Obývací pokoj + kk	vinylová podlaha, P01	výmalba, W50	výmalba, C50	2,62	22,99
113.2	Předsíň	vinylová podlaha, P01	výmalba, W50	výmalba, C02	2,40	8,32
113.3	Koupelna	keramická dlažba, P02	keramický obklad, W51	výmalba, C01	2,40	6,32
113.4	Pokoj	vinylová podlaha, P01	výmalba, W50	výmalba, C50	2,62	17,48
113.5	WC	keramická dlažba, P02	keramický obklad/výmalba, W51/W50	výmalba, C01	2,40	2,24
						57,36
113.6	Terasa	keramická dlažba, P31	fasádní probarvená omítka, F01	fasádní probarvená omítka, F41	2,65	14,41
113.7	Přezahrádka	zahradní substrát, -	-	-	-	64,57
						78,98
C2.01.13						136,33
C2						1 517,06

Schéma kótování:

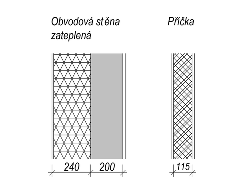

Legenda výrobků:

- L – Okna
- D – Dveře
- W – Skladby stěn
- P – Skladby podlah
- S – Skladby střech
- F – Skladby fasád a zateplení
- C – Skladby podhledů
- K – Klempířské prvky
- Z – Zámečnické prvky
- U – Truhlářské výrobky
- O – Ostatní prvky
- R – Překlady

Legenda materiálů:

- Železobeton, nosné konstrukce
- Zdivo, keramické tvárnice AKU 300 mm, nosné konstrukce
- Zdivo, keramické tvárnice 250 mm, nosné konstrukce
- Zdivo, keramické tvárnice, nenosné konstrukce
- Zdivo, betonové tvárnice, nenosné konstrukce
- Zdivo, pórobeton, instalační předstěny
- Tepelná izolace z expandovaného polystyrenu (EPS)
- Tepelná izolace z minerální vlny
- Tepelná izolace z tuhé fenolické pěny
- Tepelná izolace z extrudovaného polystyrenu (XPS)
- SDK podhled / zateplení stropu
- Zemina stávající
- Zásyp zeminou, substrát
- Kačírek

Poznámky:

- **Dokumentace je vypracována ve stupni dokumentace pro provádění stavby (DPS). Není náhradou za dílenskou dokumentaci.**
- Všechny prvky nosné konstrukce jsou dimenzovány v části D. 3 - Dokumentace stavebně konstrukčního řešení.
- Všechny konstrukce a prvky budou splňovat požadavky na požární odolnost dle části D.4 - Požárně bezpečnostní řešení (PBŘ). Styky konstrukcí budou utěsněny dle příslušných norem a PBŘ.
- Všechny skladby, prvky a jejich detaily budou řešeny kompletním systémovým řešením s garancí dodavatele.
- Instalační šachty tvoří požární úsek spolu s bytem, ke kterému náleží. V rovině stropů utěsnění rozvodů systémovým utěsněním se zabráněním akustického přeslechu.
- Keramické obklady budou v koupelnách provedeny do výšky po spodní hranu podhledu. Na samostatných WC budou provedeny do výšky 1200 mm.
- Pod keramický obklad bude aplikována hydroizolační stěrka, v podlaze vždy pod keramickou dlažbou, s vytažením min. 100 mm nad čistou podlahu a na stěnu v místě sprchového koutu nebo výlevky do výšky keramického obkladu. V rozích a koutech bude vždy použit systémový výztužný těsnicí pás dle technologického předpisu výrobce.
- Vykázaná plocha místností je orientační a vypočtená po povrch svislého průmětu ohraničujících stěn.
- Stěny a stropní desky v řezu jsou kótovány bez omítek a obkladů - viz schéma kótování.
- Světlé výšky v bytech obecně 2,62 m, v místnostech s podhledem 2,4 m. Světlé výšky ve společných chodbách 2, 38 m.
- Před výrobou jednotlivých stavebních prvků je nutné ověřit skutečné rozměry v místě osazení na stavbě a návaznosti na vybudované konstrukce.
- Rozměr otvoru pro obložkové zárubně bude určen dle konkrétního výrobku. Standardně o 50 mm vyšší a o 100 mm širší než požadovaný čistý otvor dveří.
- Prostupy v nenosných konstrukcích nejsou v půdorysech zakresleny.
- Dodávka prvků musí být vždy jako komplet, tzn. včetně kotvení, těsnění, pomocných konstrukcí apod.
- Při jakýchkoli nejasnostech nebo nových skutečnostech je nutné kontaktovat projektanta projektové dokumentace.

Revize	Popis revize	Datum
00	Vydání dokumentace	31.10.2025
01	Doplnění dokumentace - dle požadavků investora	6.2.2026
02	Kótování rozdělovačů ÚT a kemperů	6.3.2026
03	Kótování bytových rozvaděčů	17.3.2026
04	Změna orientace dveří	13.5.2026

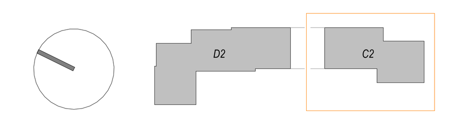

severka
schéma

± 0,000 = 224,62 m.n.m (BPV)

stavba
Na Mariánské cestě - 2. etapa

stupeň 50 - Dokumentace pro provádění stavby

zpracovatel
DC DVADVA
DC dvadva, s.r.o.
Hanusova 347/16,
140 00 Praha 4
+420 724 320 976
pro@dc22.cz
www.dc22.cz

zodpovědný projektant Ing. Libor Doležal

vypracoval Ing. arch. Jiří Šebek, Ing. Karel Martínek

stavební objekt SO03 - Bytový dům D2 a C2

část D.1.1 - Architektonicko - stavební řešení

profesní díl / členění části 01 - Stavební část

investor DOMOPLAN a.s., Trnitá 543/16, Brno, 602 00

generální projektant BK engineering project s.r.o., Hanusova 347/16, 140 00 Praha 4, info@bkproject.cz

hlavní inženýr projektu Ing. Libor Doležal

datum rev 04 - 14.5.2026

x A4 21

měřítko 1:50

číslo paré

Půdorys 1NP - sekce C2	zakázka	stupeň	s.objekt	část	členění	č. výkresu	revize
	365	50	SO03	D.1.1	01	102b	04