


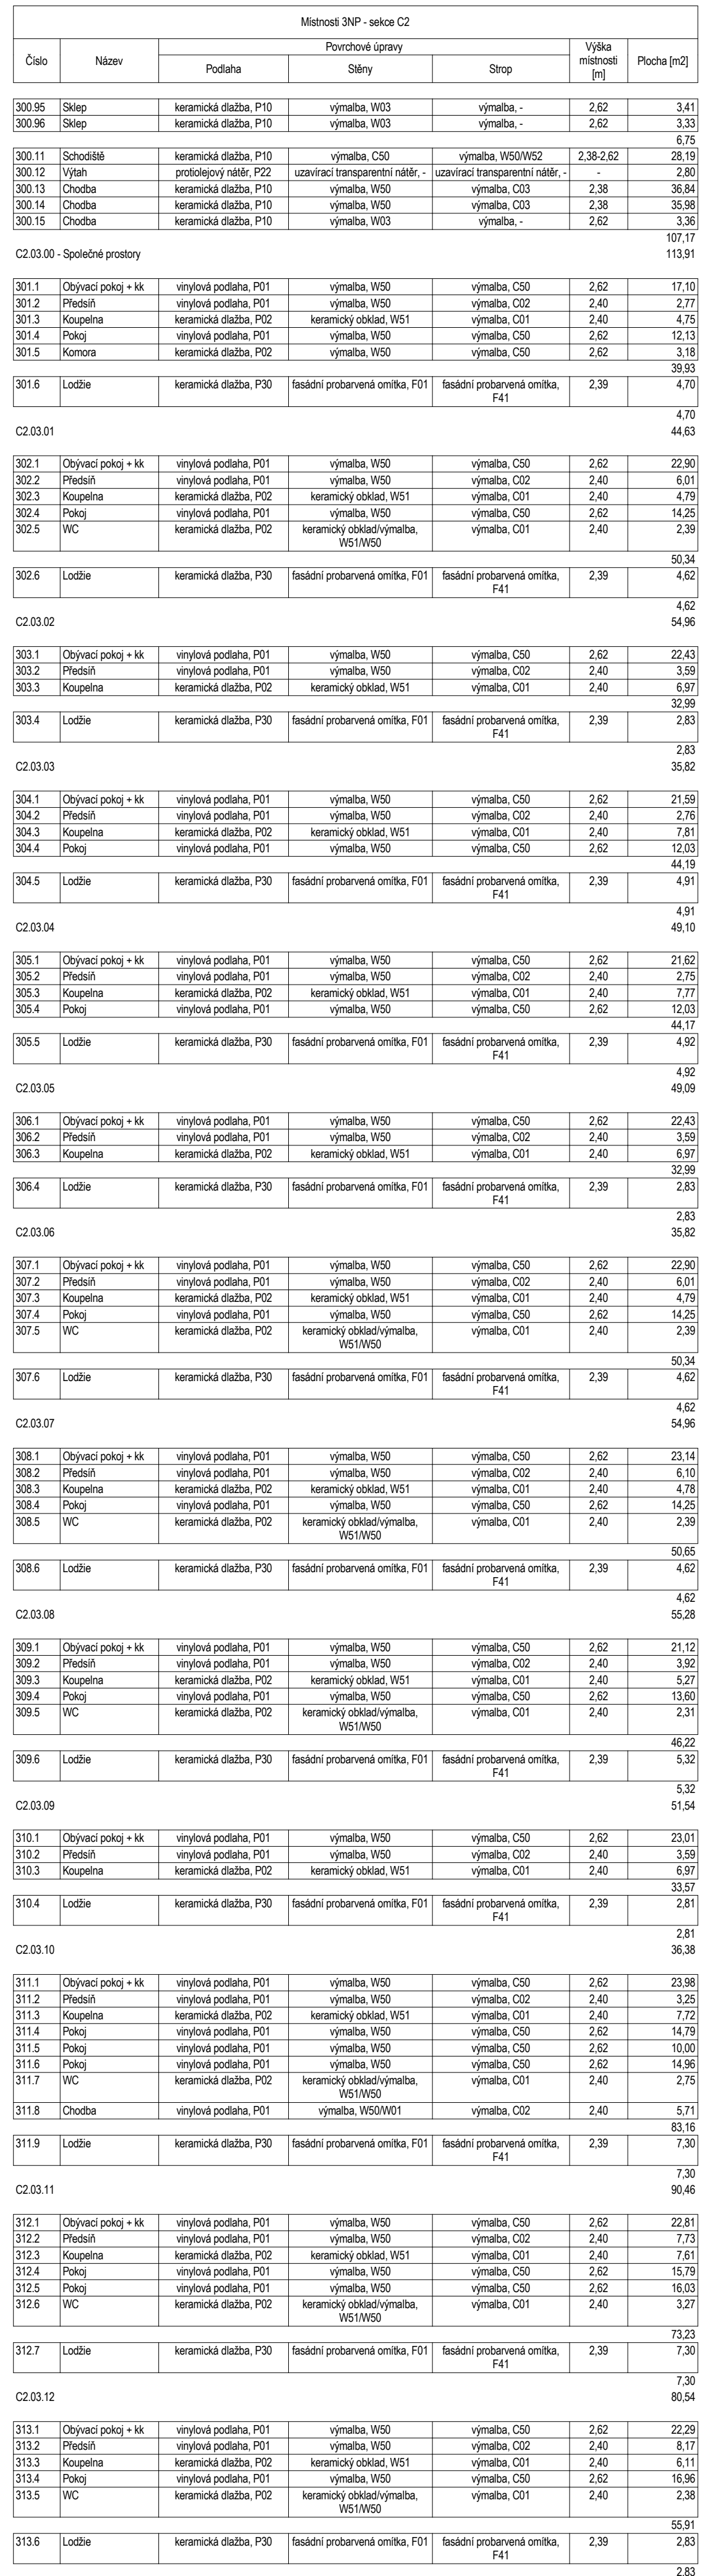


Obvodová stěna zateplená

Průřez


240 200

115

 One	4	Štěrpkovitý prvek	Zakalovací, nosná konstrukce		Teplotní izolace s minerální vlnou
Two	3	Zemělní prvek	Zuko, keramické tvárnice KAU 300 mm, nosná konstrukce		Teplotní izolace s tuhou fenolovou
Štěrpkovitý	4	Teplotní vlny	Zuko, keramické tvárnice 250 mm, nosná konstrukce		Teplotní izolace s akustickými polystyreny (XPS)
Štěrpkovitý	3	Ostřetv. prvek	Zuko, keramické tvárnice, nosná konstrukce		ŠOK podlahy, zateplení stropu
Štěrpkovitý	4	Průhledný	Zuko, betónové tvárnice, nosná konstrukce		Záma stávková
Štěrpkovitý (nosná zateplení)	3		Zuko, betonové tvárnice, nosná konstrukce		
Štěrpkovitý (podlahy)	3		Zuko, pískobeton, instalační předehřívání		Zásta, zeminná, subzistál

[illegible]

00	Vydání dokumentace	31.10.2019
01	Doplnění dokumentace - dle požadavků investora	6.2.2020
02	Kótování rozdělovačů ÚT a kemperů	6.3.2020
03	Změna orientace dveří	13.5.2020
04	Doplnění označení oken	07.07.2020
Revize	Popis revize	Datum

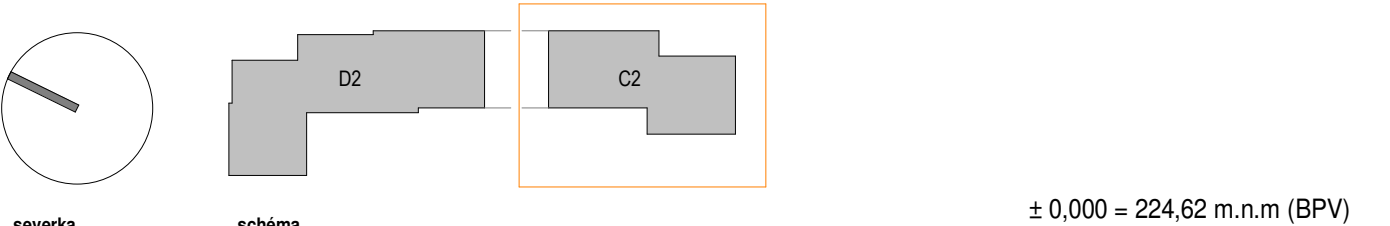

zpracovatel	zodpovědný projektant	stavby
		stavěbní objekt

DČ DVA/DVA vypracoval **Petr Štěrba** část
D.1.1 - Architektonicko-technická

investor	generální projektant	datum 2014.03.03.00000	číslo paré
----------	----------------------	---------------------------	------------

Ing. Libor Doležal				1:50			
	zakázka	stavební	soubor	číslo	žánr	č. výkresu	reviz

Pūdorys 3NP - sekce C2	365	50	SO03	D.1.1	01	104b	0
------------------------	-----	----	------	-------	----	------	---