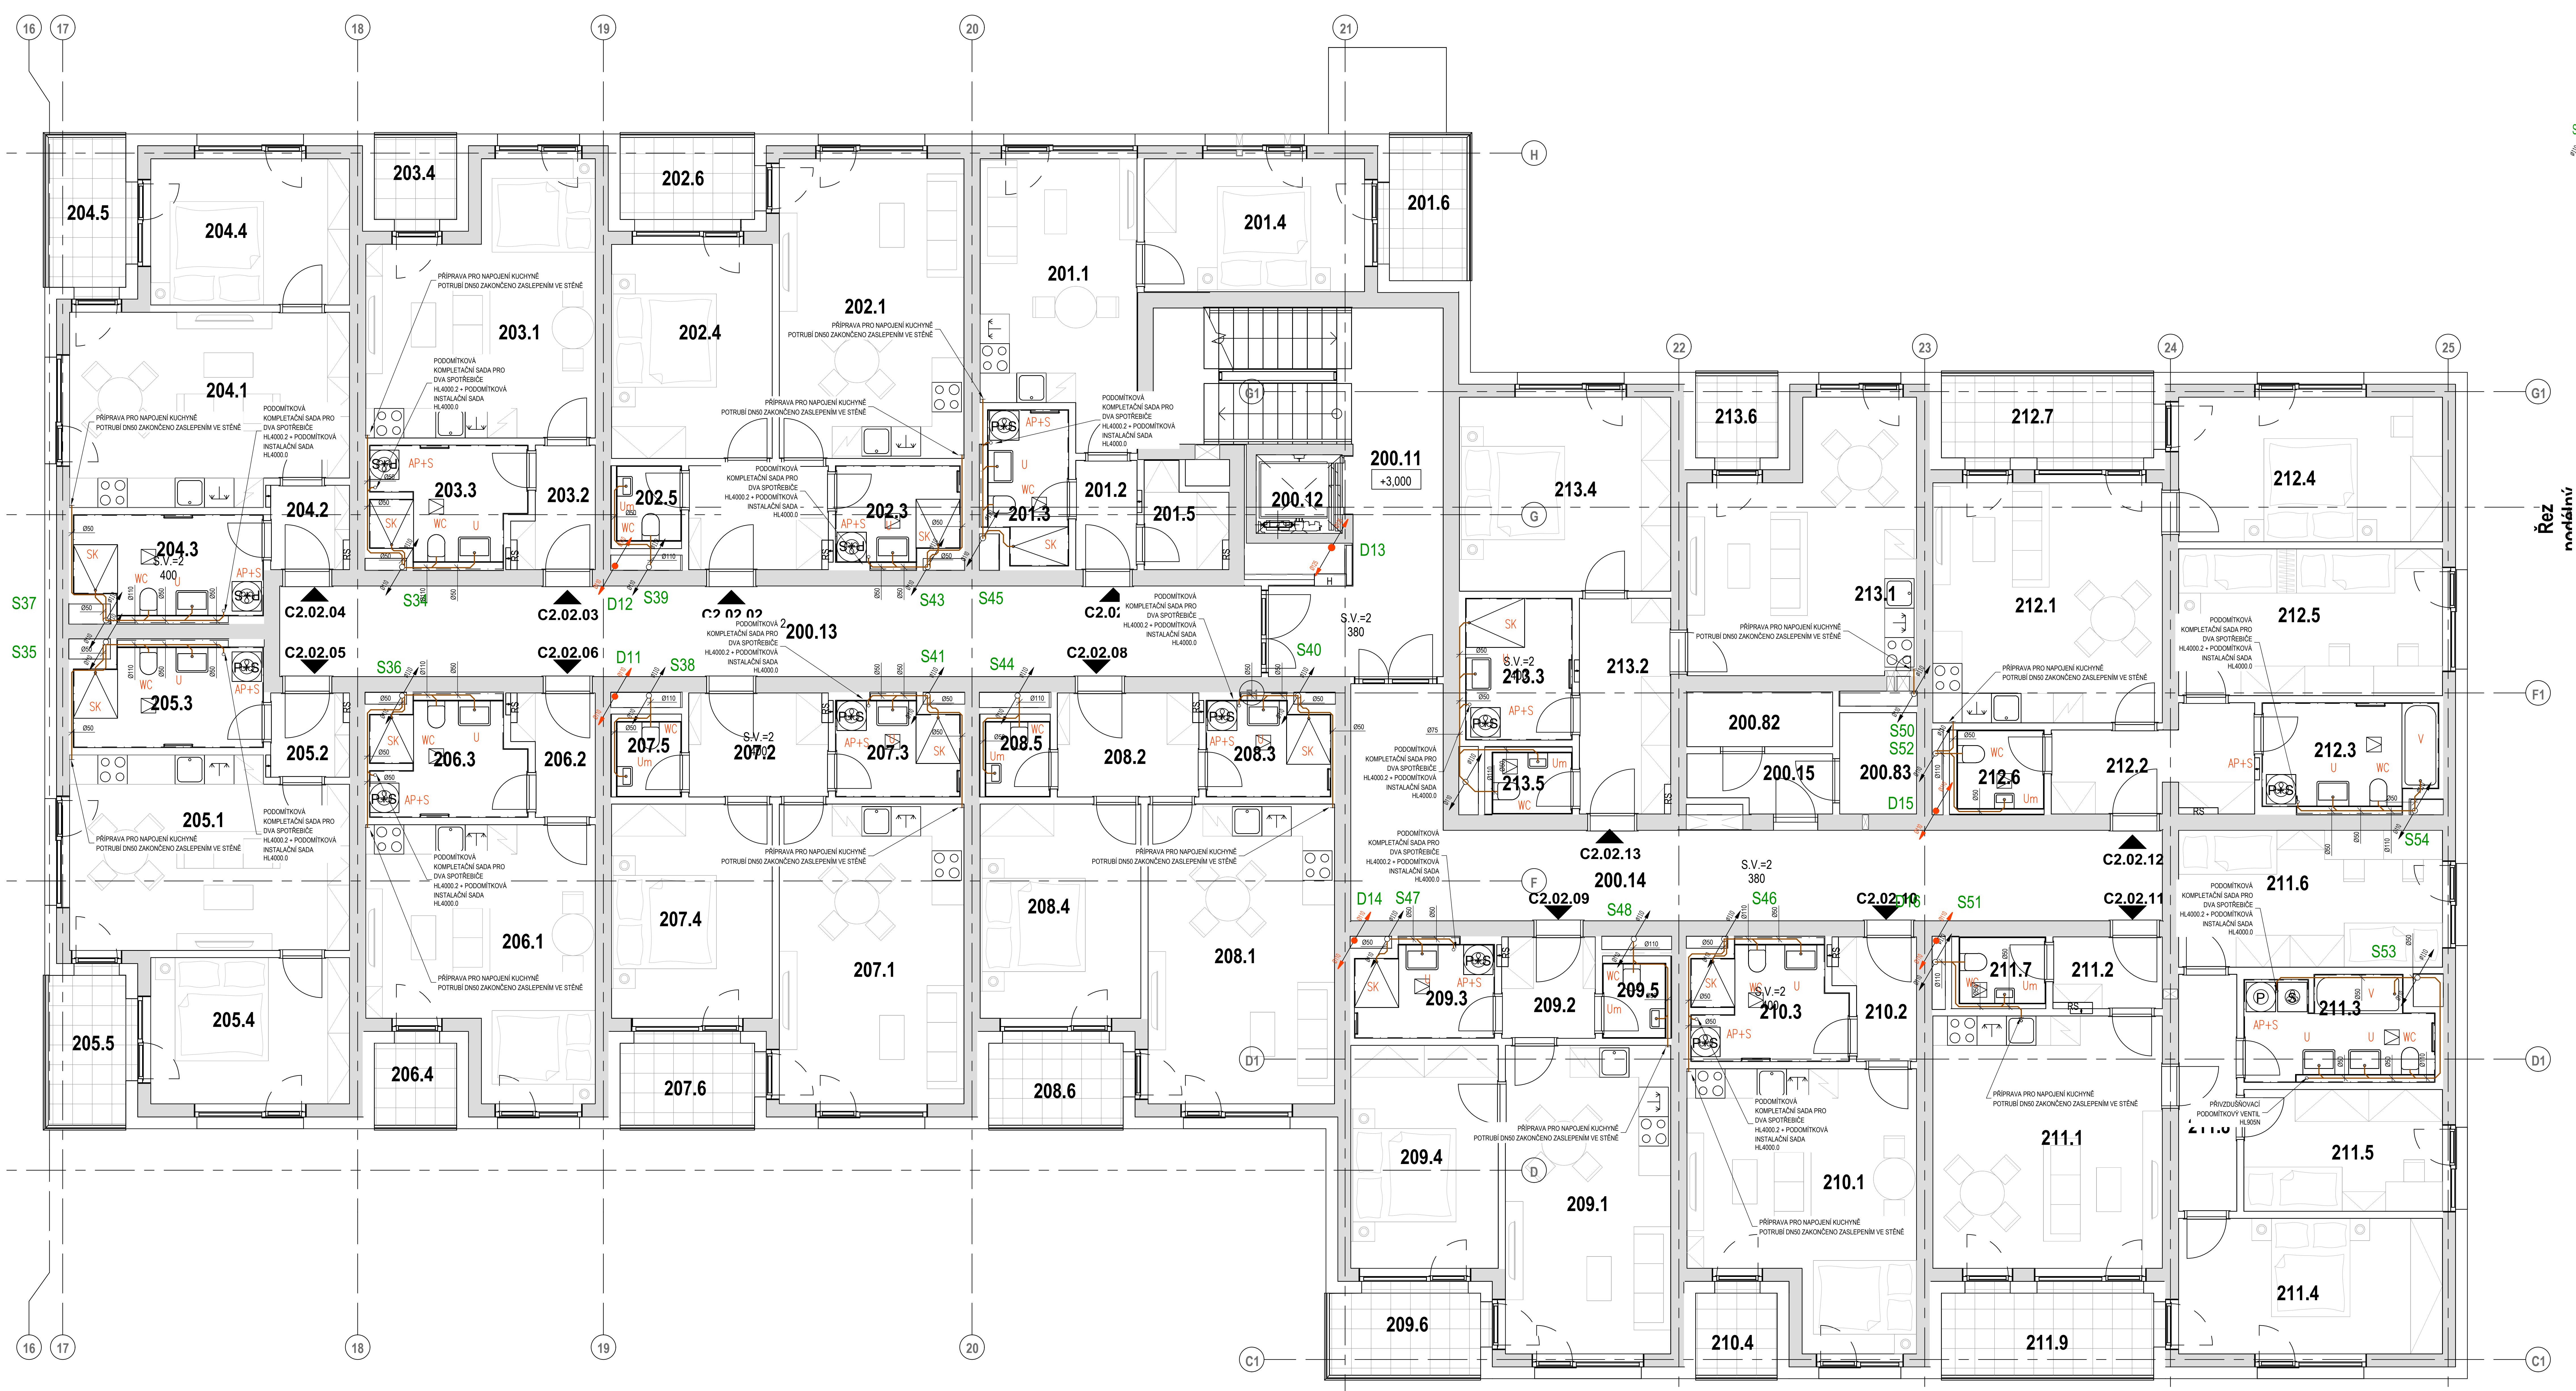

LEGENDA:

———————	SPLAŠKOVÁ KANALIZACE PŘIPOJOVACÍ POTRUBÍ (PP-HT)
— · · — · · —	SPLAŠKOVÁ KANALIZACE POD STROPEM (PP-HT)
— — — — —	SPLAŠKOVÁ KANALIZACE V PODLAZE (PP-HT)
—— · · — D — · · — D —	DEŠŤOVÁ KANALIZACE POD STROPEM (SVAŘOVANÉ PE, IZOLOVÁNO)
—— — — D — — — D —	DEŠŤOVÁ KANALIZACE V PODLAZE (SVAŘOVANÉ PE, IZOLOVÁNO)
Sx ○ Ø110 / Dx ● Ø110	SVISLÝ ODPAD KANALIZACE SPLAŠKOVÉ, DEŠŤOVÁ

LEGENDA zařizovacích předmětů

WC	ZÁVĚSNÝ KLOZET KERAMICKÝ BÍLÝ, SPLACHOVACÍ NÁDRŽKA VESTAVĚNÁ, OVLÁD. DESTIČKA S TLAČÍTKEM, ROHOVÝ VENTIL 1/2" SOUČÁSTÍ NÁDRŽKY
U	UMYVADLO KERAMICKÉ/ UMYVADLO KERAM. NA DESKU, SIFON UMYVADLOVÝ TRUBKOVÝ DN 40, SIFON UMYVADLOVÝ DN 40, UMYVADLOVÁ BATERIE STOJÁNKOVÁ PÁKOVÁ, 2x ROHOVÝ VENTIL S PŘIPOJOVACÍ HADICÍ
D	KUCH. DŘEZ, SIFON DŘEZOVÝ DN50 S PŘEPADEM, BATERIE DŘEZOVÁ STOJÁNKOVÁ PÁKOVÁ, DŘEZ NENÍ SOUČÁSTÍ DODÁVKY ZTI
SK	SPRCHOVÝ KOUT SE ZÁSTĚNOU, SPRCHA HLAVOVÁ, SPRCHOVÁ BAT. PODOMÍTKOVÝ SET, SPRCHOVÝ ŽLÁBEK SE SIFONEM DN 50
V	VANA AKRYLÁTOVÁ , SIFON VANOVÝ DN 50 S PŘEPADEM , BATERIE VANOVÁ NÁSTĚNNÁ SE SPRCHOVÝM SETEM
M	KUCHYŇSKÁ MYČKA PRAČKOVÝ SIFON HL400, PRAČKOVÝ KOHOUT 1/2" - KULOVÝ
AP+S	AUTOMATICKÁ PRAČKA + SUŠIČKA PRAČKOVÝ SIFON HL4000.2, PRAČKOVÝ KOHOUT 1/2" - KULOVÝ
VL	VÝLEVKA KERAMICKÁ STACIONÁRNÍ NEBO ZÁVĚSNÁ, BATERIE VÝLEVKOVÁ NÁSTĚNNÁ PÁKOVÁ
G	PODLAHOVÁ VPUST - např. HL310NPr se svislým odtokem nebo HL510NPr s vodorovným odtokem a přídavnou suchou uzávěrkou

POZNÁMKA: SPECIFIKACE ZAŘIZOVACÍCH PŘEDMĚTŮ PRO GASTRO PROVOZ VIZ PD GASTRO.
PŘESNÁ SPECIFIKACE OSTATNÍCH ZAŘIZOVACÍCH PŘEDMĚTŮ DLE INVESTORA A ARCHITEKTA.

Poznámky:
Sprcha:
- sprcha ve výšce 2100 mm zarovnaná na výšku svítidla u umyvadla,
- podomítková baterie ve výšce 1000 mm
- rohový ventil pro napojení sprchy 170 mm od směšovací podomítkové baterie směrem ke stěně

V případě rozporu v půdoryse platí schéma

SCHEMA PŘÍPRAVY PRO KUCHYŇSKOU LINKU

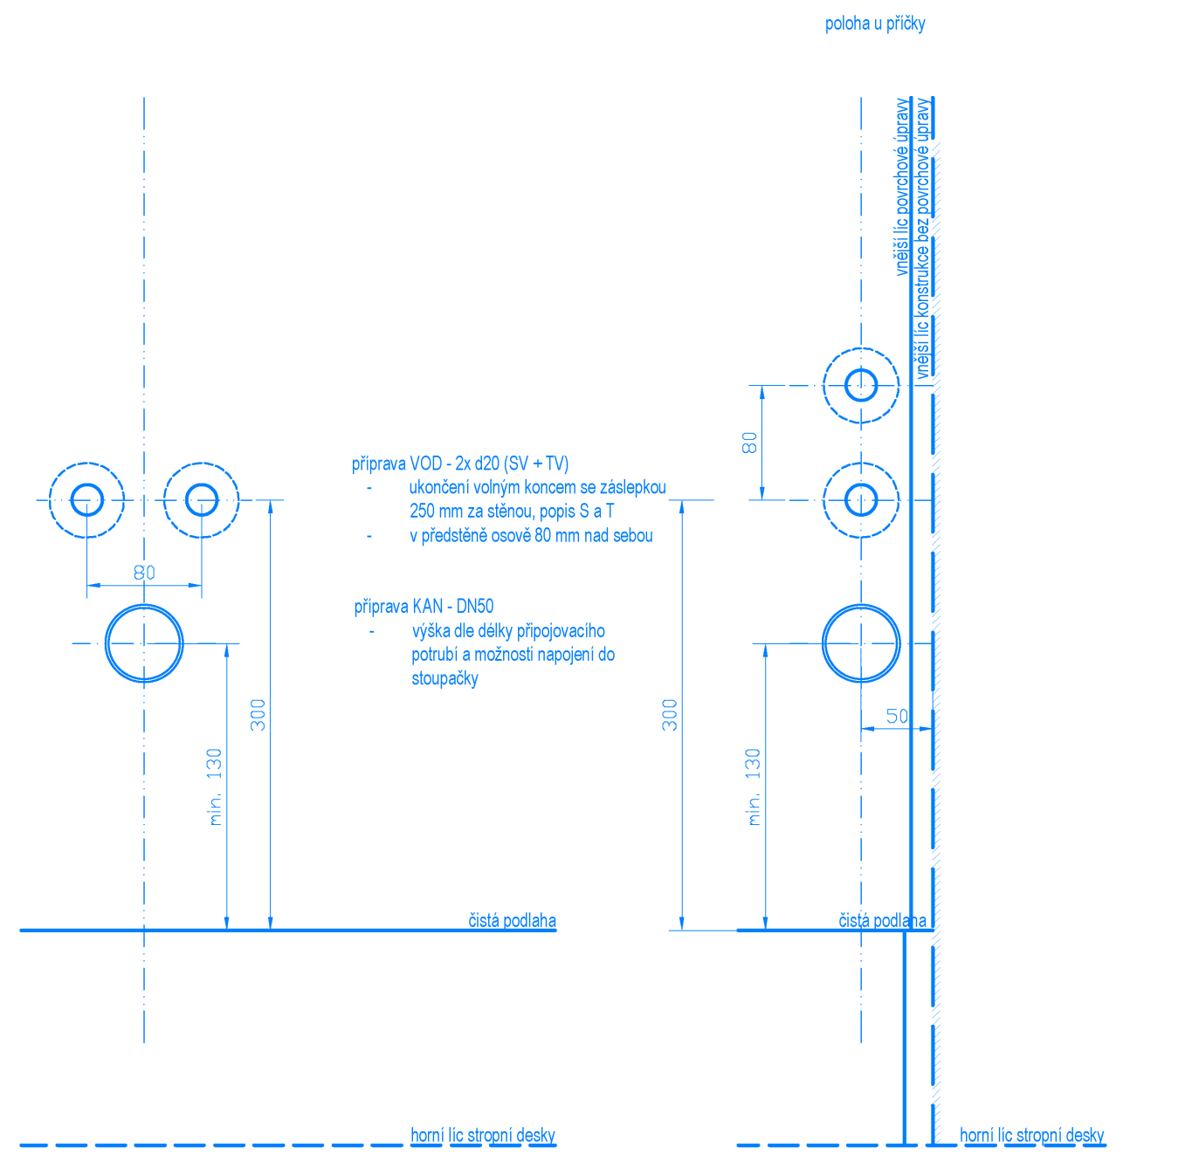
poloha u příčky
příprava VOD - 2x d20 (SV + TV)
- ukončení volným koncem se záslepkou 250 mm za stěnou, popis S a T
- v předstěně osově 80 mm nad sebou
příprava KAN - DN50
- výška dle délky připojovacího potrubí a možnosti napojení do stoupačky
80
300
min. 130
50
čistá podlaha
horní líc stropní desky
vnější líc povrchové úpravy
vnější líc konstrukce bez povrchové úpravy

SCHEMA PŘÍPRAVY PRO PRAČKU A SUŠIČKU

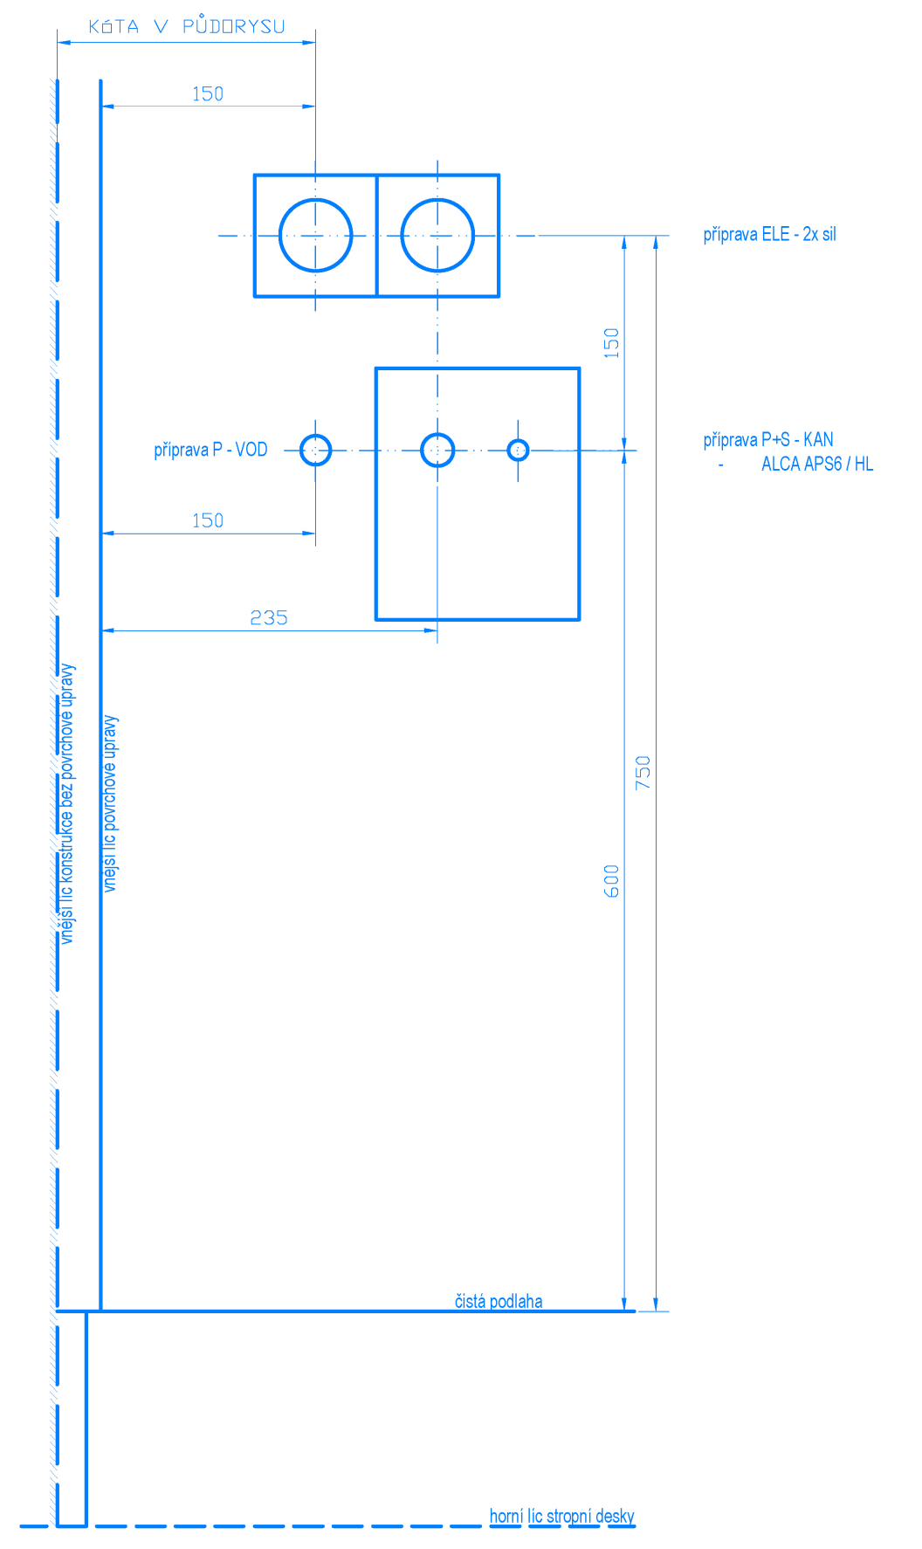

Revize	Popis revize	Datum

severka

± 0,000 = 224,62 m.n.m (BPV)

stavba **BD Na Mariánské cestě - 2. etapa**		stupeň Dokumentace pro provádění stavby
zpracovatel vodopro ing. Pavel Jakubů Hraničná 107, 468 11 Janov nad Nisou	zodpovědný projektant Ing. Pavel Jakubů vypracoval Ing. Sandra Nevímová Daria Tombegr	stavební objekt SO03 - Bytový dům D2 a C2 část D.1.2.2 - Zdravotně technické instalace profesní díl / členění části 02 - Zdravotně technické instalace - KANALIZACE
investor DOMOPLAN a.s. Trnitá 543/16, Brno, 602 00	generální projektant BK engineering project s.r.o. Hanusova 347/16 140 00 Praha 4 info@bkproject.cz hlavní inženýr projektu Ing. Libor Doležal	datum 10/2025 18 x A4 měřítko 1:50 číslo paré

	zakázka	stupeň	s.objekt	část	členění	č. výkresu	revize
PŮDORYS 2.NP - OBJEKT C2	365	50	SO03	D.1.2.2	02	005b	