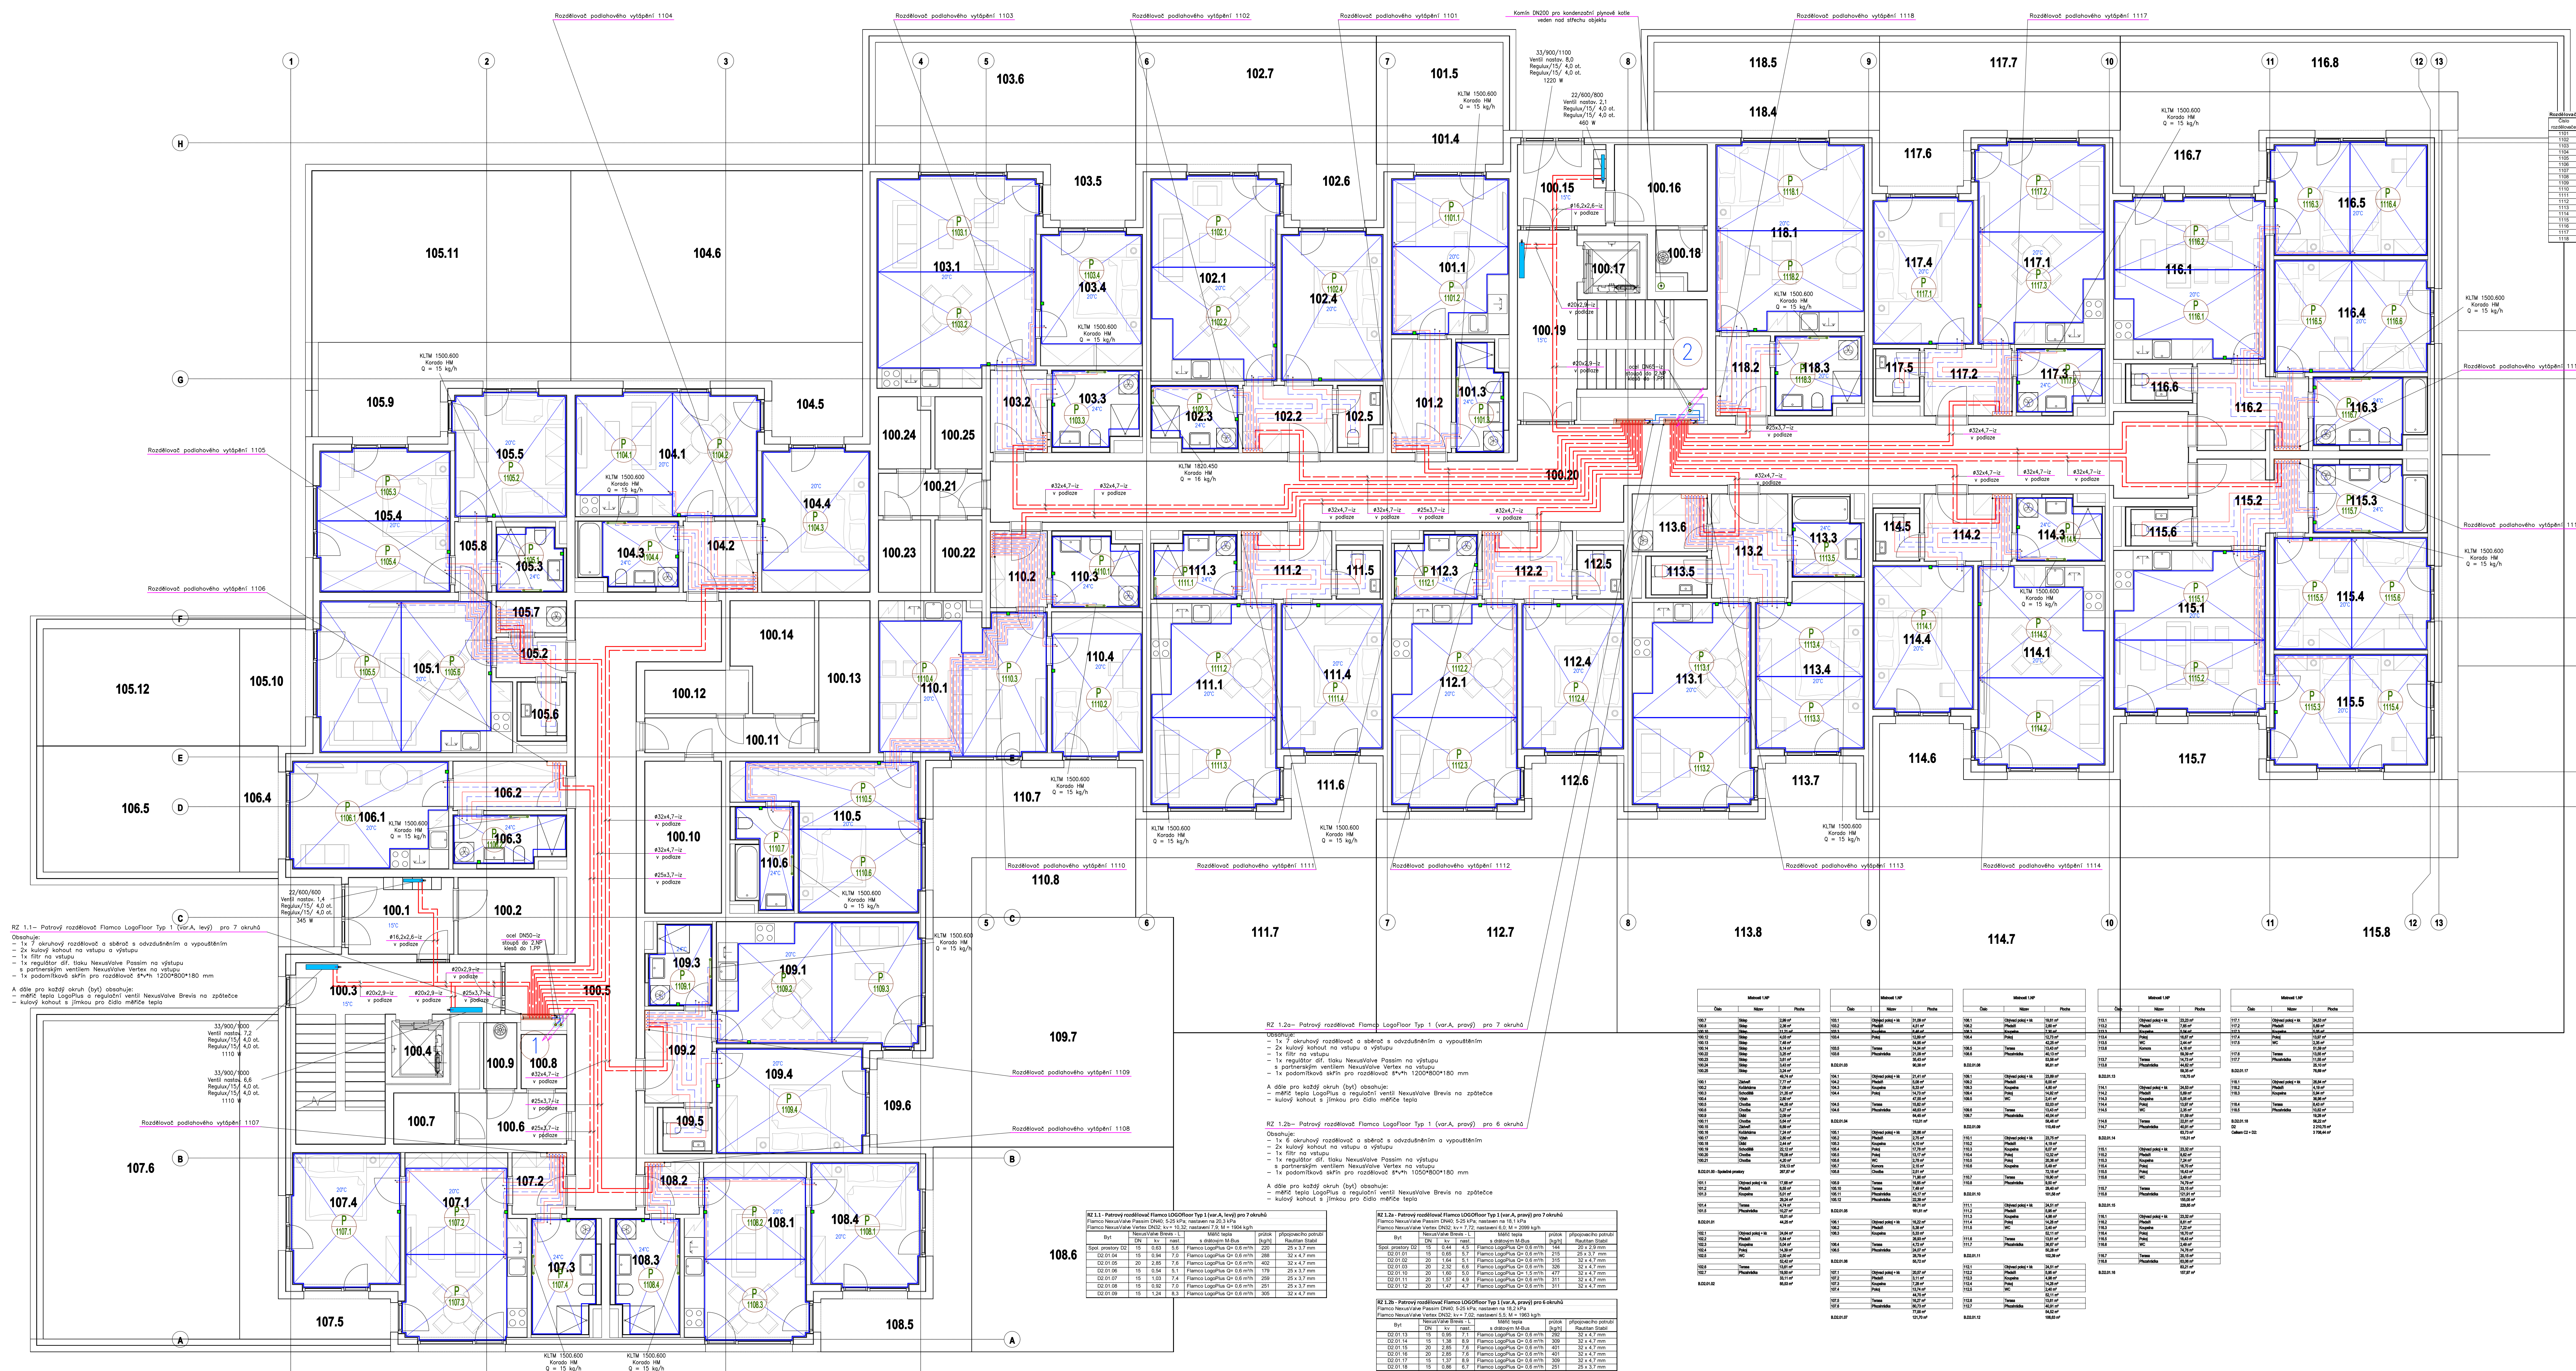
Rozdělovač podlahového vytápění 1101
Rozdělovač podlahového vytápění 1102
Komín DN200 pro kondenzační plynové kotle veden nad střechu objektu
33/900/1100 Ventil nastav. 8,0 Regulux/15/ 4,0 ot. Regulux/15/ 4,0 ot. 1220 W
22/600/800 Ventil nastav. 2,1 Regulux/15/ 4,0 ot. Regulux/15/ 4,0 ot. 460 W
22/600/600 Ventil nastav. 1,4 Regulux/15/ 4,0 ot. Regulux/15/ 4,0 ot. 345 W
33/900/1000 Ventil nastav. 7,2 Regulux/15/ 4,0 ot. Regulux/15/ 4,0 ot. 1110 W
33/900/1000 Ventil nastav. 6,6 Regulux/15/ 4,0 ot. Regulux/15/ 4,0 ot. 1110 W
KLTM 1500.600 Korado HM Q = 15 kg/h
KLTM 1820.450 Korado HM Q = 16 kg/h
ø16,2x2,6–iz v podlaze
ø20x2,9–iz v podlaze
ø25x3,7–iz v podlaze
ø32x4,7–iz v podlaze
ocel DN65–iz stoupá do 2.NP klesá do 1.PP
ocel DN50–iz stoupá do 2.NP klesá do 1.PP
1
2
100.1 100.2 100.3 100.4 100.5 100.6 100.7 100.8 100.9 100.10 100.11 100.12 100.13 100.14 100.15 100.16 100.17 100.18 100.19 100.20 100.21 100.22 100.23 100.24 100.25
15°C
20°C
24°C

RZ 1.1– Patrový rozdělovač Flamco LogoFloor Typ 1 (var.A, levý) pro 7 okruhů

Obsahuje:
- 1x 7 okruhový rozdělovač a sběrač s odvzdušněním a vypouštěním
- 2x kulový kohout na vstupu a výstupu
- 1x filtr na vstupu
- 1x regulátor dif. tlaku NexusValve Passim na výstupu s partnerským ventilem NexusValve Vertex na vstupu
- 1x podomítková skříň pro rozdělovač š*v*h 1200*800*180 mm

A dále pro každý okruh (byt) obsahuje:
- měřič tepla LogoPlus a regulační ventil NexusValve Brevis na zpátečce
- kulový kohout s jímkou pro čidlo měřiče tepla

RZ 1.2a– Patrový rozdělovač Flamco LogoFloor Typ 1 (var.A, pravý) pro 7 okruhů

Obsahuje:
- 1x 7 okruhový rozdělovač a sběrač s odvzdušněním a vypouštěním
- 2x kulový kohout na vstupu a výstupu
- 1x filtr na vstupu
- 1x regulátor dif. tlaku NexusValve Passim na výstupu s partnerským ventilem NexusValve Vertex na vstupu
- 1x podomítková skříň pro rozdělovač š*v*h 1200*800*180 mm

A dále pro každý okruh (byt) obsahuje:
- měřič tepla LogoPlus a regulační ventil NexusValve Brevis na zpátečce
- kulový kohout s jímkou pro čidlo měřiče tepla

RZ 1.2b– Patrový rozdělovač Flamco LogoFloor Typ 1 (var.A, pravý) pro 6 okruhů

Obsahuje:
- 1x 6 okruhový rozdělovač a sběrač s odvzdušněním a vypouštěním
- 2x kulový kohout na vstupu a výstupu
- 1x filtr na vstupu
- 1x regulátor dif. tlaku NexusValve Passim na výstupu s partnerským ventilem NexusValve Vertex na vstupu
- 1x podomítková skříň pro rozdělovač š*v*h 1050*800*180 mm

A dále pro každý okruh (byt) obsahuje:
- měřič tepla LogoPlus a regulační ventil NexusValve Brevis na zpátečce
- kulový kohout s jímkou pro čidlo měřiče tepla

RZ 1.1 - Patrový rozdělovač Flamco LOGOfloor Typ 1 (var.A, levý) pro 7 okruhů
Flamco NexusValve Passim DN40; 5-25 kPa; nastaven na 20,3 kPa
Flamco NexusValve Vertex DN32; kv = 10,32; nastavení 7,9; M = 1904 kg/h

Byt	NexusValve Brevis - L			Měřič tepla	průtok	připojovacího potrubí
	DN	kv	nast.	s drátovým M-Bus	[kg/h]	Rautitan Stabil
Spol. prostory D2	15	0,63	5,6	Flamco LogoPlus Q= 0,6 m³/h	220	25 x 3,7 mm
D2.01.04	15	0,94	7,0	Flamco LogoPlus Q= 0,6 m³/h	288	32 x 4,7 mm
D2.01.05	20	2,85	7,6	Flamco LogoPlus Q= 0,6 m³/h	402	32 x 4,7 mm
D2.01.06	15	0,54	5,1	Flamco LogoPlus Q= 0,6 m³/h	179	25 x 3,7 mm
D2.01.07	15	1,03	7,4	Flamco LogoPlus Q= 0,6 m³/h	259	25 x 3,7 mm
D2.01.08	15	0,92	7,0	Flamco LogoPlus Q= 0,6 m³/h	251	25 x 3,7 mm
D2.01.09	15	1,24	8,3	Flamco LogoPlus Q= 0,6 m³/h	305	32 x 4,7 mm

RZ 1.2a - Patrový rozdělovač Flamco LOGOfloor Typ 1 (var.A, pravý) pro 7 okruhů
Flamco NexusValve Passim DN40; 5-25 kPa; nastaven na 18,1 kPa
Flamco NexusValve Vertex DN32; kv = 7,72; nastavení 6,0; M = 2099 kg/h

Byt	NexusValve Brevis - L			Měřič tepla	průtok	připojovacího potrubí
	DN	kv	nast.	s drátovým M-Bus	[kg/h]	Rautitan Stabil
Spol. prostory D2	15	0,44	4,5	Flamco LogoPlus Q= 0,6 m³/h	144	20 x 2,9 mm
D2.01.01	15	0,65	5,7	Flamco LogoPlus Q= 0,6 m³/h	215	25 x 3,7 mm
D2.01.02	20	1,64	5,1	Flamco LogoPlus Q= 0,6 m³/h	315	32 x 4,7 mm
D2.01.03	20	2,32	6,6	Flamco LogoPlus Q= 0,6 m³/h	326	32 x 4,7 mm
D2.01.10	20	1,60	5,0	Flamco LogoPlus Q= 1,5 m³/h	477	32 x 4,7 mm
D2.01.11	20	1,57	4,9	Flamco LogoPlus Q= 0,6 m³/h	311	32 x 4,7 mm
D2.01.12	20	1,47	4,7	Flamco LogoPlus Q= 0,6 m³/h	311	32 x 4,7 mm

RZ 1.2b - Patrový rozdělovač Flamco LOGOfloor Typ 1 (var.A, pravý) pro 6 okruhů
Flamco NexusValve Passim DN40; 5-25 kPa; nastaven na 18,2 kPa
Flamco NexusValve Vertex DN32; kv = 7,02; nastavení 5,5; M = 1963 kg/h

Byt	NexusValve Brevis - L			Měřič tepla	průtok	připojovacího potrubí
	DN	kv	nast.	s drátovým M-Bus	[kg/h]	Rautitan Stabil
D2.01.13	15	0,95	7,1	Flamco LogoPlus Q= 0,6 m³/h	292	32 x 4,7 mm
D2.01.14	15	1,38	8,9	Flamco LogoPlus Q= 0,6 m³/h	309	32 x 4,7 mm
D2.01.15	20	2,85	7,6	Flamco LogoPlus Q= 0,6 m³/h	401	32 x 4,7 mm
D2.01.16	20	2,85	7,6	Flamco LogoPlus Q= 0,6 m³/h	401	32 x 4,7 mm
D2.01.17	15	1,37	8,9	Flamco LogoPlus Q= 0,6 m³/h	309	32 x 4,7 mm
D2.01.18	15	0,86	6,7	Flamco LogoPlus Q= 0,6 m³/h	251	25 x 3,7 mm

Místnosti 1.NP

Číslo	Název	Plocha
100.7	Sklep	2,99 m²
100.8	Sklep	2,36 m²
100.10	Sklep	11,21 m²
100.12	Sklep	4,03 m²
100.13	Sklep	7,48 m²
100.14	Sklep	8,14 m²
100.22	Sklep	3,25 m²
100.23	Sklep	3,61 m²
100.24	Sklep	3,43 m²
100.25	Sklep	3,24 m²
		49,74 m²
100.1	Zádveří	7,77 m²
100.2	Kočárkárna	7,09 m²
100.3	Schodiště	21,35 m²
100.4	Výtah	2,80 m²
100.5	Chodba	44,35 m²
100.6	Chodba	5,27 m²
100.9	Úklid	2,09 m²
100.11	Chodba	5,64 m²
100.15	Zádveří	6,89 m²
100.16	Kočárkárna	7,24 m²
100.17	Výtah	2,80 m²
100.18	Úklid	2,44 m²
100.19	Schodiště	22,12 m²
100.20	Chodba	76,08 m²
100.21	Chodba	4,20 m²
		218,13 m²
B.D2.01.00 - Společné prostory		267,87 m²
101.1	Obývací pokoj + kk	17,68 m²
101.2	Předsíň	6,55 m²
101.3	Koupelna	5,01 m²
		29,24 m²
101.4	Terasa	4,74 m²
101.5	Přezahrádka	10,27 m²
		15,01 m²
B.D2.01.01		44,25 m²
102.1	Obývací pokoj + kk	24,64 m²
102.2	Předsíň	5,84 m²
102.3	Koupelna	5,04 m²
102.4	Pokoj	14,39 m²
102.5	WC	2,50 m²
		52,42 m²
102.6	Terasa	13,61 m²
102.7	Přezahrádka	19,50 m²
		33,11 m²
B.D2.01.02		85,53 m²

Místnosti 1.NP

Číslo	Název	Plocha
103.1	Obývací pokoj + kk	31,09 m²
103.2	Předsíň	4,51 m²
103.3	Koupelna	6,46 m²
103.4	Pokoj	12,89 m²
		54,95 m²
103.5	Terasa	14,34 m²
103.6	Přezahrádka	21,09 m²
		35,43 m²
B.D2.01.03		90,38 m²
104.1	Obývací pokoj + kk	21,41 m²
104.2	Předsíň	5,08 m²
104.3	Koupelna	6,33 m²
104.4	Pokoj	14,73 m²
		47,55 m²
104.5	Terasa	15,82 m²
104.6	Přezahrádka	48,63 m²
		64,45 m²
B.D2.01.04		112,01 m²
105.1	Obývací pokoj + kk	26,66 m²
105.2	Předsíň	2,75 m²
105.3	Koupelna	4,10 m²
105.4	Pokoj	17,78 m²
105.5	Pokoj	13,17 m²
105.6	WC	2,78 m²
105.7	Komora	2,15 m²
105.8	Chodba	2,51 m²
		71,90 m²
105.9	Terasa	16,65 m²
105.10	Terasa	7,49 m²
105.11	Přezahrádka	43,17 m²
105.12	Přezahrádka	22,39 m²
		89,71 m²
B.D2.01.05		161,61 m²
106.1	Obývací pokoj + kk	16,22 m²
106.2	Předsíň	5,38 m²
106.3	Koupelna	5,33 m²
		26,93 m²
106.4	Terasa	4,72 m²
106.5	Přezahrádka	24,07 m²
		28,79 m²
B.D2.01.06		55,72 m²
107.1	Obývací pokoj + kk	20,57 m²
107.2	Předsíň	3,11 m²
107.3	Koupelna	7,28 m²
107.4	Pokoj	13,74 m²
		44,70 m²
107.5	Terasa	16,27 m²
107.6	Přezahrádka	60,73 m²
		77,00 m²
B.D2.01.07		121,70 m²

Místnosti 1.NP

Číslo	Název	Plocha
108.1	Obývací pokoj + kk	19,61 m²
108.2	Předsíň	2,60 m²
108.3	Koupelna	7,30 m²
108.4	Pokoj	12,73 m²
		42,25 m²
108.5	Terasa	13,43 m²
108.6	Přezahrádka	40,13 m²
		53,56 m²
B.D2.01.08		95,81 m²
109.1	Obývací pokoj + kk	23,89 m²
109.2	Předsíň	6,00 m²
109.3	Koupelna	4,80 m²
109.4	Pokoj	14,92 m²
109.5	WC	2,41 m²
		52,03 m²
109.6	Terasa	13,43 m²
109.7	Přezahrádka	45,04 m²
		58,46 m²
B.D2.01.09		110,49 m²
110.1	Obývací pokoj + kk	23,75 m²
110.2	Předsíň	4,19 m²
110.3	Koupelna	6,07 m²
110.4	Pokoj	12,32 m²
110.5	Pokoj	20,36 m²
110.6	Koupelna	5,49 m²
		72,18 m²
110.7	Terasa	19,90 m²
110.8	Přezahrádka	9,50 m²
		29,40 m²
B.D2.01.10		101,58 m²
111.1	Obývací pokoj + kk	24,51 m²
111.2	Předsíň	5,95 m²
111.3	Koupelna	4,98 m²
111.4	Pokoj	14,28 m²
111.5	WC	2,40 m²
		52,11 m²
111.6	Terasa	13,61 m²
111.7	Přezahrádka	36,67 m²
		50,28 m²
B.D2.01.11		102,39 m²
112.1	Obývací pokoj + kk	24,51 m²
112.2	Předsíň	5,95 m²
112.3	Koupelna	4,98 m²
112.4	Pokoj	14,28 m²
112.5	WC	2,40 m²
		52,11 m²
112.6	Terasa	13,61 m²
112.7	Přezahrádka	40,91 m²
		54,52 m²
B.D2.01.12		106,63 m²

Místnosti 1.NP

Číslo	Název	Plocha
113.1	Obývací pokoj + kk	23,23 m²
113.2	Předsíň	7,65 m²
113.3	Koupelna	5,04 m²
113.4	Pokoj	16,87 m²
113.5	WC	2,44 m²
113.6	Komora	4,16 m²
		59,39 m²
113.7	Terasa	14,73 m²
113.8	Přezahrádka	44,62 m²
		59,35 m²
B.D2.01.13		118,75 m²
114.1	Obývací pokoj + kk	24,53 m²
114.2	Předsíň	5,69 m²
114.3	Koupelna	5,05 m²
114.4	Pokoj	13,97 m²
114.5	WC	2,35 m²
		51,59 m²
114.6	Terasa	22,81 m²
114.7	Přezahrádka	40,91 m²
		63,73 m²
B.D2.01.14		115,31 m²
115.1	Obývací pokoj + kk	23,32 m²
115.2	Předsíň	8,62 m²
115.3	Koupelna	7,24 m²
115.4	Pokoj	16,70 m²
115.5	Pokoj	16,43 m²
115.6	WC	2,49 m²
		74,79 m²
115.7	Terasa	33,15 m²
115.8	Přezahrádka	121,91 m²
		155,05 m²
B.D2.01.15		229,85 m²
116.1	Obývací pokoj + kk	23,32 m²
116.2	Předsíň	8,61 m²
116.3	Koupelna	7,22 m²
116.4	Pokoj	16,70 m²
116.5	Pokoj	16,43 m²
116.6	WC	2,49 m²
		74,76 m²
116.7	Terasa	20,15 m²
116.8	Přezahrádka	63,06 m²
		83,21 m²
B.D2.01.16		157,97 m²

Místnosti 1.NP

Číslo	Název	Plocha
117.1	Obývací pokoj + kk	24,53 m²
117.2	Předsíň	5,69 m²
117.3	Koupelna	5,05 m²
117.4	Pokoj	13,97 m²
117.5	WC	2,35 m²
		51,59 m²
117.6	Terasa	13,55 m²
117.7	Přezahrádka	11,55 m²
		25,10 m²
B.D2.01.17		76,69 m²
118.1	Obývací pokoj + kk	26,84 m²
118.2	Předsíň	4,19 m²
118.3	Koupelna	5,94 m²
		36,96 m²
118.4	Terasa	8,43 m²
118.5	Přezahrádka	10,82 m²
		19,26 m²
B.D2.01.18		56,22 m²
D2		2 210,75 m²
Celkem C2 + D2:		3 708,44 m²

Rozdělovače podlahového vytápění REHAU v 1.NP:

Číslo rozdělovače	Přívodní teplota	Typ rozdělovače	Skříň rozdělovače	Tlaková ztráta [kPa]	Hmotnostní průtok [kg/h]
1101	43°C	HKV-D 4 nerez	AP 605	1,6	215
1102	43°C	HKV-D 5 nerez	AP 605	5,8	315
1103	43°C	HKV-D 5 nerez	AP 605	6,1	326
1104	43°C	HKV-D 5 nerez	AP 605	3,3	288
1105	43°C	HKV-D 7 nerez	AP 805	4,2	402
1106	43°C	HKV-D 3 nerez	AP 605	5,4	179
1107	43°C	HKV-D 5 nerez	AP 605	6,3	259
1108	43°C	HKV-D 5 nerez	AP 605	5,5	251
1109	43°C	HKV-D 5 nerez	AP 605	6,6	305
1110	43°C	HKV-D 9 nerez	AP 805	1,9	477
1111	43°C	HKV-D 5 nerez	AP 605	5,7	311
1112	43°C	HKV-D 5 nerez	AP 605	5,7	311
1113	43°C	HKV-D 6 nerez	AP 805	1,8	292
1114	43°C	HKV-D 5 nerez	AP 605	5,2	309
1115	43°C	HKV-D 8 nerez	AP 805	1,9	401
1116	43°C	HKV-D 8 nerez	AP 805	1,9	401
1117	43°C	HKV-D 5 nerez	AP 605	5,2	309
1118	43°C	HKV-D 4 nerez	AP 605	3,4	251

PODLAHOVÉ VYTÁPĚNÍ v 1.NP

Číslo rozdělovače	Okruh	Plocha celková [m2]	Rozteč [mm]	Délka celková [m]	Průtok [kg/h]
1101	P 1101.1	7,7	150	68	65
	P 1101.2	7,7	150	61	65
	P 1101.3	4,4	100	49	71
1102	P 1102.1	10,8	150	92	69
	P 1102.2	10,8	150	77	69
	P 1102.3	4,6	100	51	74
	P 1102.4	14,1	150	113	90
1103	P 1103.1	14,4	150	112	92
	P 1103.2	14,4	150	105	92
	P 1103.3	5,7	100	62	62
	P 1103.4	10,6	150	82	68
1104	P 1104.1	9,6	150	76	61
	P 1104.2	9,6	150	72	61
	P 1104.3	12,3	150	91	78
	P 1104.4	4,6	100	55	74
1105	P 1105.1	3,6	100	48	42
	P 1105.2	13,0	150	102	83
	P 1105.3	8,8	150	76	56
	P 1105.4	8,8	150	74	56
	P 1105.5	11,9	150	96	76
	P 1105.6	11,9	150	98	76
1106	P 1106.1	14,2	150	104	90
	P 1106.2	4,6	100	56	74
1107	P 1107.1	13,6	150	104	95
	P 1107.2	8,4	150	62	54
	P 1107.3	8,4	150	66	54
	P 1107.4	6,5	100	71	43
1108	P 1108.1	12,6	150	96	93
	P 1108.2	7,9	150	59	50
	P 1108.3	7,9	150	63	50
	P 1108.4	6,5	100	71	43
1109	P 1109.1	4,2	100	47	67
	P 1109.2	10,3	150	74	66
	P 1109.3	10,3	150	90	66
	P 1109.4	14,6	150	116	93
1110	P 1110.1	5,4	100	62	65
	P 1110.2	10,3	150	80	66
	P 1110.3	10,5	150	78	67
	P 1110.4	10,5	150	82	67
	P 1110.5	9,7	150	90	62
	P 1110.6	9,7	150	96	62
	P 1110.7	3,9	100	76	63
1111	P 1111.1	4,5	100	50	72
	P 1111.2	10,7	150	76	68
	P 1111.3	10,7	150	91	68
	P 1111.4	14,0	150	112	89
1112	P 1112.1	4,5	100	49	72
	P 1112.2	10,7	150	76	68
	P 1112.3	10,7	150	91	68
	P 1112.4	14,0	150	112	89
1113	P 1113.1	10,1	150	85	64
	P 1113.2	10,1	150	86	64
	P 1113.3	7,5	150	67	48
	P 1113.4	7,5	150	62	48
	P 1113.5	3,4	100	44	55
1114	P 1114.1	13,7	150	108	87
	P 1114.2	10,7	150	91	68
	P 1114.3	10,7	150	76	68
	P 1114.4	4,5	100	50	72
1115	P 1115.1	10,2	150	88	65
	P 1115.2	10,2	150	83	65
	P 1115.3	8,1	150	73	52
	P 1115.4	8,1	150	78	52
	P 1115.5	8,1	150	60	52
	P 1115.6	8,1	150	64	52
	P 1115.7	5,7	100	62	51
1116	P 1116.1	10,2	150	88	65
	P 1116.2	10,2	150	83	65
	P 1116.3	8,1	150	73	52
	P 1116.4	8,1	150	78	52
	P 1116.5	8,1	150	60	52
	P 1116.6	8,1	150	64	52
	P 1116.7	5,7	100	62	51
1117	P 1117.1	13,7	150	108	87
	P 1117.2	10,7	150	91	68
	P 1117.3	10,7	150	76	68
	P 1117.4	4,5	100	50	72
1118	P 1118.1	12,3	150	95	78
	P 1118.2	12,3	150	89	78
	P 1118.3	5,6	100	64	80

Rozdělovače podlahového vytápění REHAU v 1.NP:

Číslo rozdělovače	Přívodní teplota	Typ rozdělovače	Skříň rozdělovače	Tlaková ztráta [kPa]	Hmotnostní průtok [kg/h]
2101	43°C	HKV-D 4 nerez	AP 605	1,5	201
2102	43°C	HKV-D 5 nerez	AP 605	5,9	302
2103	43°C	HKV-D 4 nerez	AP 605	1,9	215
2104	43°C	HKV-D 5 nerez	AP 605	2,7	250
2105	43°C	HKV-D 5 nerez	AP 605	2,7	250
2106	43°C	HKV-D 4 nerez	AP 605	1,9	215
2107	43°C	HKV-D 5 nerez	AP 605	5,9	302
2108	43°C	HKV-D 5 nerez	AP 605	5,9	305
2109	43°C	HKV-D 5 nerez	AP 605	2,7	283
2110	43°C	HKV-D 4 nerez	AP 605	2,1	218
2111	43°C	HKV-D 8 nerez	AP 805	4,7	452
2112	43°C	HKV-D 8 nerez	AP 805	1,9	415
2113	43°C	HKV-D 5 nerez	AP 605	6,5	305

PODLAHOVÉ VYTÁPĚNÍ v 1.NP

Číslo rozdělovače	Okruh	Plocha celková [m2]	Rozteč [mm]	Délka celková [m]	Průtok [kg/h]
2101	P 2101.1	9,6	150	82	61
	P 2101.2	9,6	150	72	61
	P 2101.3	4,5	100	52	65
2102	P 2102.1	14,2	150	113	90
	P 2102.2	10,4	150	87	66
	P 2102.3	10,4	150	78	66
	P 2102.4	4,1	100	47	66
2103	P 2103.1	10,4	150	83	66
	P 2103.2	10,4	150	77	66
	P 2103.3	6,4	100	70	68
2104	P 2104.1	10,9	150	85	74
	P 2104.2	9,0	150	70	57
	P 2104.3	9,0	150	66	57
	P 2104.4	7,1	100	76	47
2105	P 2105.1	10,9	150	85	74
	P 2105.2	9,0	150	70	57
	P 2105.3	9,0	150	66	57
	P 2105.4	7,1	100	76	47
2106	P 2106.1	6,4	100	70	68
	P 2106.2	10,4	150	77	66
	P 2106.3	10,4	150	83	66
2107	P 2107.1	14,2	150	113	90
	P 2107.2	10,4	150	87	66
	P 2107.3	10,4	150	78	66
	P 2107.4	4,1	100	47	66
2108	P 2108.1	14,2	150	113	90
	P 2108.2	10,5	150	88	67
	P 2108.3	10,5	150	79	67
	P 2108.4	4,2	100	48	67
2109	P 2109.1	4,7	100	53	75
	P 2109.2	11,6	150	88	74
	P 2109.3	9,4	150	80	60
	P 2109.4	9,4	150	81	60
2110	P 2110.1	6,4	100	70	68
	P 2110.2	10,6	150	79	68
	P 2110.3	10,6	150	86	68
2111	P 2111.1	11,2	150	79	71
	P 2111.2	11,2	150	88	71
	P 2111.3	13,3	150	107	85
	P 2111.4	9,9	150	82	63
	P 2111.5	5,5	100	74	54
	P 2111.6	7,5	150	75	48
	P 2111.7	7,5	150	77	48
2112	P 2112.1	10,2	150	86	65
	P 2112.2	10,2	150	81	65
	P 2112.3	8,0	150	70	51
	P 2112.4	8,0	150	75	51
	P 2112.5	8,0	150	58	51
	P 2112.6	8,0	150	63	51
	P 2112.7	5,8	100	64	68
2113	P 2113.1	14,8	150	111	94
	P 2113.2	5,9	100	74	65
	P 2113.3	10,4	150	79	66
	P 2113.4	10,4	150	84	66

Místnosti 1.NP

Číslo	Název	Plocha
100.34	Sklep	3,45 m²
100.35	Sklep	3,37 m²
		6,82 m²
100.26	Zádveří	7,68 m²
100.27	Kočárkárna	4,81 m²
100.28	Schodiště	29,27 m²
100.29	Výtah	2,80 m²
100.30	Úklid	1,57 m²
100.31	Chodba	36,96 m²
100.32	Chodba	37,00 m²
100.33	Chodba	3,29 m²
		123,38 m²
B.C2.01.00 - Společné prostory		130,20 m²
101.1	Obývací pokoj + kk	21,50 m²
101.2	Předsíň	4,52 m²
101.3	Koupelna	4,98 m²
		31,00 m²
101.4	Terasa	6,53 m²
101.5	Přezahrádka	8,38 m²
		14,91 m²
B.C2.01.01		45,90 m²
102.1	Obývací pokoj + kk	23,76 m²
102.2	Předsíň	5,92 m²
102.3	Koupelna	4,77 m²
102.4	Pokoj	14,49 m²
102.5	WC	2,26 m²
		51,21 m²
102.6	Terasa	13,35 m²
102.7	Přezahrádka	11,03 m²
		24,38 m²
B.C2.01.02		75,59 m²
103.1	Obývací pokoj + kk	22,99 m²
103.2	Předsíň	3,68 m²
103.3	Koupelna	7,23 m²
		33,90 m²
103.4	Terasa	8,91 m²
103.5	Přezahrádka	7,70 m²
		16,61 m²
B.C2.01.03		50,52 m²
104.1	Obývací pokoj + kk	22,18 m²
104.2	Předsíň	2,78 m²
104.3	Koupelna	8,00 m²
104.4	Pokoj	12,26 m²
		45,22 m²
104.5	Terasa	13,19 m²
104.6	Přezahrádka	58,55 m²
		71,74 m²
B.C2.01.04		116,96 m²

Místnosti 1.NP

Číslo	Název	Plocha
105.1	Obývací pokoj + kk	22,21 m²
105.2	Předsíň	2,77 m²
105.3	Koupelna	8,00 m²
105.4	Pokoj	12,26 m²
		45,24 m²
105.5	Terasa	13,19 m²
105.6	Přezahrádka	112,25 m²
		125,44 m²
B.C2.01.05		170,68 m²
106.1	Obývací pokoj + kk	22,99 m²
106.2	Předsíň	3,68 m²
106.3	Koupelna	7,23 m²
		33,90 m²
106.4	Terasa	8,91 m²
106.5	Přezahrádka	32,95 m²
		41,86 m²
B.C2.01.06		75,77 m²
107.1	Obývací pokoj + kk	23,79 m²
107.2	Předsíň	5,91 m²
107.3	Koupelna	4,77 m²
107.4	Pokoj	14,51 m²
107.5	WC	2,26 m²
		51,23 m²
107.6	Terasa	13,76 m²
107.7	Přezahrádka	49,43 m²
		63,18 m²
B.C2.01.07		114,41 m²
108.1	Obývací pokoj + kk	23,88 m²
108.2	Předsíň	5,92 m²
108.3	Koupelna	4,81 m²
108.4	Pokoj	14,51 m²
108.5	WC	2,26 m²
		51,38 m²
108.6	Terasa	12,99 m²
108.7	Přezahrádka	45,21 m²
		58,20 m²
B.C2.01.08		109,58 m²
109.1	Obývací pokoj + kk	21,76 m²
109.2	Předsíň	3,92 m²
109.3	Koupelna	5,41 m²
109.4	Pokoj	13,76 m²
109.5	WC	2,23 m²
		47,08 m²
109.6	Terasa	14,50 m²
109.7	Přezahrádka	45,04 m²
		59,54 m²
B.C2.01.09		106,62 m²

Místnosti 1.NP

Číslo	Název	Plocha
110.1	Obývací pokoj + kk	23,58 m²
110.2	Předsíň	3,70 m²
110.3	Koupelna	7,23 m²
		34,51 m²
110.4	Terasa	8,89 m²
110.5	Přezahrádka	29,95 m²
		38,84 m²
B.C2.01.10		73,35 m²
111.1	Obývací pokoj + kk	24,47 m²
111.2	Předsíň	3,34 m²
111.3	Koupelna	7,82 m²
111.4	Pokoj	15,27 m²
111.5	Pokoj	10,12 m²
111.6	Pokoj	15,30 m²
111.7	WC	2,67 m²
111.8	Chodba	5,83 m²
		84,84 m²
111.9	Terasa	19,88 m²
111.10	Přezahrádka	61,70 m²
		81,57 m²
B.C2.01.11		166,41 m²
112.1	Obývací pokoj + kk	23,29 m²
112.2	Předsíň	7,88 m²
112.3	Koupelna	7,75 m²
112.4	Pokoj	16,28 m²
112.5	Pokoj	16,25 m²
112.6	WC	3,30 m²
		74,74 m²
112.7	Terasa	14,39 m²
112.8	Přezahrádka	37,76 m²
		52,15 m²
B.C2.01.12		126,90 m²
113.1	Obývací pokoj + kk	22,99 m²
113.2	Předsíň	8,32 m²
113.3	Koupelna	6,25 m²
113.4	Pokoj	17,48 m²
113.5	WC	2,21 m²
		57,26 m²
113.6	Terasa	14,41 m²
113.7	Přezahrádka	63,13 m²
		77,54 m²
B.C2.01.13		134,80 m²
C2		1 497,69 m²


Rozdělovač podlahového vytápění 2101
Rozdělovač podlahového vytápění 2102
Rozdělovač podlahového vytápění 2103
Rozdělovač podlahového vytápění 2104
Rozdělovač podlahového vytápění 2105
Rozdělovač podlahového vytápění 2106
Rozdělovač podlahového vytápění 2107
Rozdělovač podlahového vytápění 2108
Rozdělovač podlahového vytápění 2109
Rozdělovač podlahového vytápění 2110
Rozdělovač podlahového vytápění 2111
Rozdělovač podlahového vytápění 2112
Rozdělovač podlahového vytápění 2113
33/600/800 Ventil nastav. 3,8 Regulux/15/ 4,0 ot. Regulux/15/ 4,0 ot. 660 W
33/900/1100 Ventil nastav. 8,0 Regulux/15/ 4,0 ot. Regulux/15/ 4,0 ot. 1220 W
KLTM 1500.600 Korado HM Q = 15 kg/h
KLTM 1820.450 Korado HM Q = 16 kg/h
ø16,2x2,6–iz v podlaze
ø20x2,9–iz v podlaze
ø25x3,7–iz v podlaze
ø32x4,7–iz v podlaze
ocel DN50–iz stoupá do 2.NP klesá do 1.PP
3
4
100.26 100.27 100.28 100.29 100.30 100.31 100.32 100.33 100.34 100.35
15°C
20°C
24°C

RZ 1.3– Patrový rozdělovač Flamco LogoFloor Typ 1 (var.A, levý) pro 9 okruhů

Obsahuje:
- 1x 9 okruhový rozdělovač a sběrač s odvzdušněním a vypouštěním
- 2x kulový kohout na vstupu a výstupu
- 1x filtr na vstupu
- 1x regulátor dif. tlaku NexusValve Passim na výstupu s partnerským ventilem NexusValve Vertex na vstupu
- 1x podomítková skříň pro rozdělovač š*v*h 1450*800*180 mm

A dále pro každý okruh (byt) obsahuje:
- měřič tepla LogoPlus a regulační ventil NexusValve Brevis na zpátečce
- kulový kohout s jímkou pro čidlo měřiče tepla

RZ 1.4– Patrový rozdělovač Flamco LogoFloor Typ 1 (var.A, levý) pro 5 okruhů

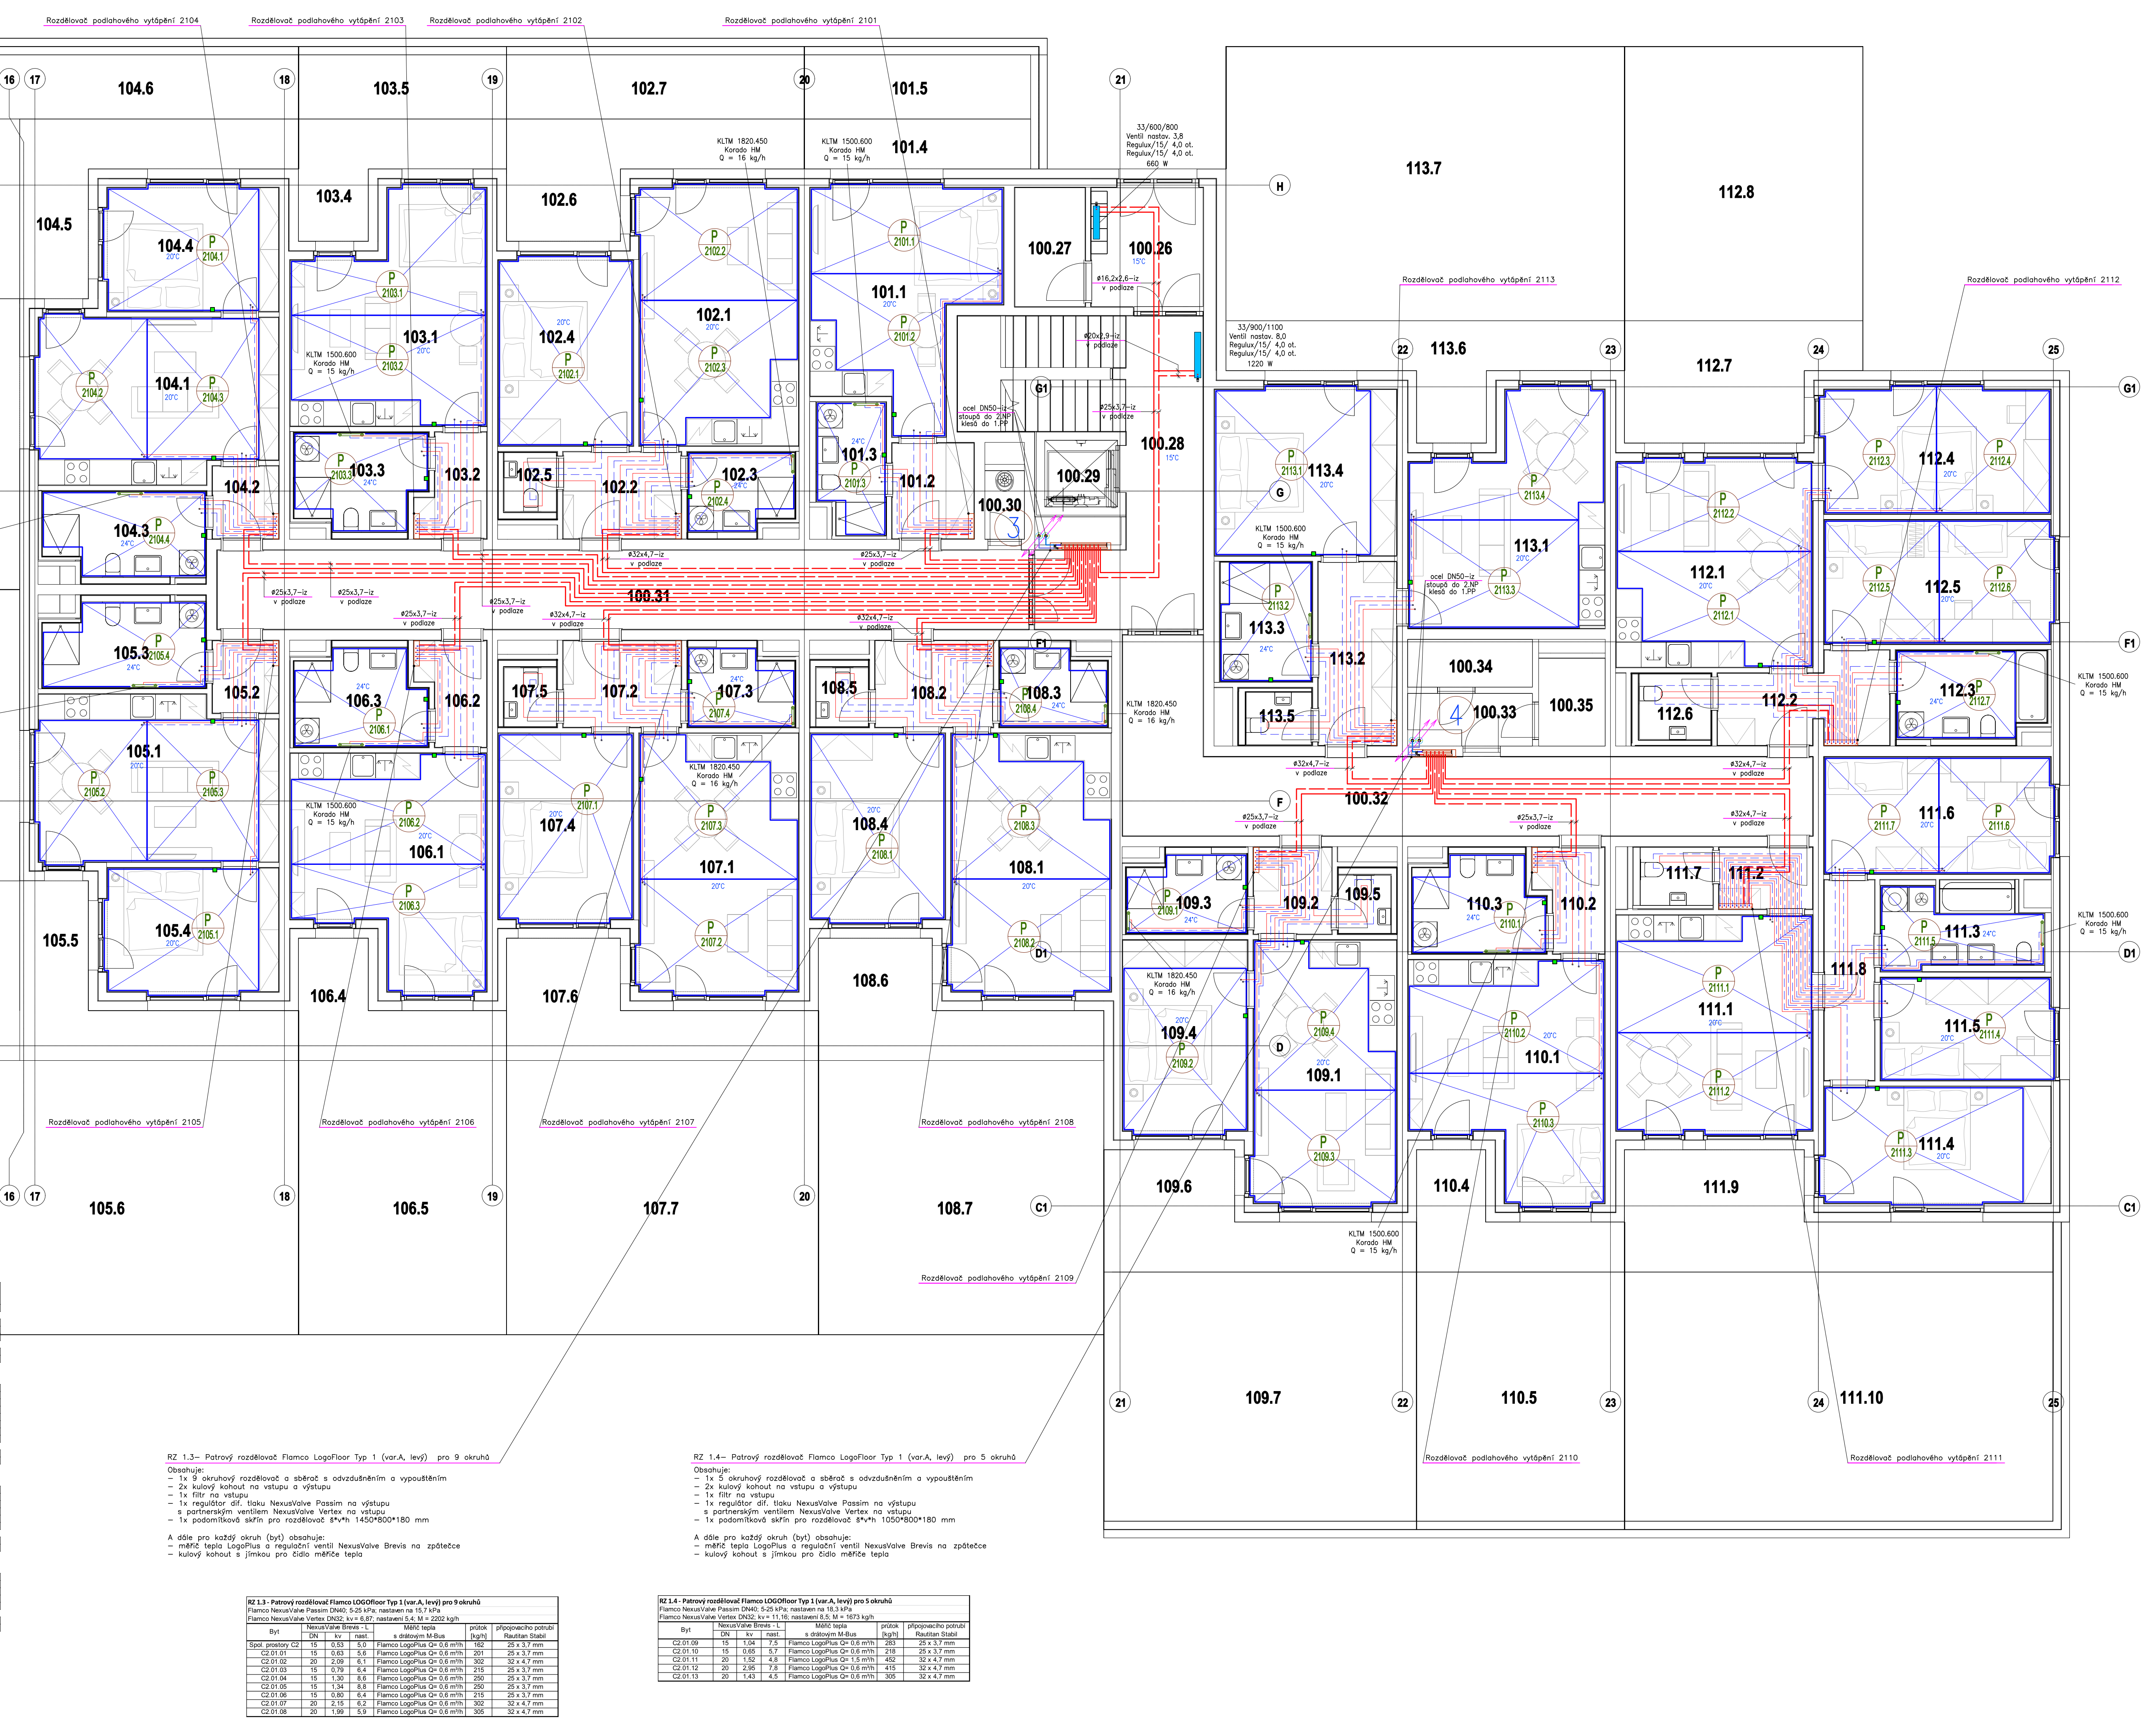Obsahuje:
- 1x 5 okruhový rozdělovač a sběrač s odvzdušněním a vypouštěním
- 2x kulový kohout na vstupu a výstupu
- 1x filtr na vstupu
- 1x regulátor dif. tlaku NexusValve Passim na výstupu s partnerským ventilem NexusValve Vertex na vstupu
- 1x podomítková skříň pro rozdělovač š*v*h 1050*800*180 mm

A dále pro každý okruh (byt) obsahuje:
- měřič tepla LogoPlus a regulační ventil NexusValve Brevis na zpátečce
- kulový kohout s jímkou pro čidlo měřiče tepla

RZ 1.3 - Patrový rozdělovač Flamco LOGOfloor Typ 1 (var.A, levý) pro 9 okruhů
Flamco NexusValve Passim DN40; 5-25 kPa; nastaven na 15,7 kPa
Flamco NexusValve Vertex DN32; kv = 6,87; nastavení 5,4; M = 2202 kg/h

Byt	NexusValve Brevis - L			Měřič tepla	průtok	připojovacího potrubí
	DN	kv	nast.	s drátovým M-Bus	[kg/h]	Rautitan Stabil
Spol. prostory C2	15	0,53	5,0	Flamco LogoPlus Q= 0,6 m³/h	162	25 x 3,7 mm
C2.01.01	15	0,63	5,6	Flamco LogoPlus Q= 0,6 m³/h	201	25 x 3,7 mm
C2.01.02	20	2,09	6,1	Flamco LogoPlus Q= 0,6 m³/h	302	32 x 4,7 mm
C2.01.03	15	0,79	6,4	Flamco LogoPlus Q= 0,6 m³/h	215	25 x 3,7 mm
C2.01.04	15	1,30	8,6	Flamco LogoPlus Q= 0,6 m³/h	250	25 x 3,7 mm
C2.01.05	15	1,34	8,8	Flamco LogoPlus Q= 0,6 m³/h	250	25 x 3,7 mm
C2.01.06	15	0,80	6,4	Flamco LogoPlus Q= 0,6 m³/h	215	25 x 3,7 mm
C2.01.07	20	2,15	6,2	Flamco LogoPlus Q= 0,6 m³/h	302	32 x 4,7 mm
C2.01.08	20	1,99	5,9	Flamco LogoPlus Q= 0,6 m³/h	305	32 x 4,7 mm

RZ 1.4 - Patrový rozdělovač Flamco LOGOfloor Typ 1 (var.A, levý) pro 5 okruhů
Flamco NexusValve Passim DN40; 5-25 kPa; nastaven na 18,3 kPa
Flamco NexusValve Vertex DN32; kv = 11,16; nastavení 8,5; M = 1673 kg/h

Byt	NexusValve Brevis - L			Měřič tepla	průtok	připojovacího potrubí
	DN	kv	nast.	s drátovým M-Bus	[kg/h]	Rautitan Stabil
C2.01.09	15	1,04	7,5	Flamco LogoPlus Q= 0,6 m³/h	283	25 x 3,7 mm
C2.01.10	15	0,65	5,7	Flamco LogoPlus Q= 0,6 m³/h	218	25 x 3,7 mm
C2.01.11	20	1,52	4,8	Flamco LogoPlus Q= 1,5 m³/h	452	32 x 4,7 mm
C2.01.12	20	2,95	7,8	Flamco LogoPlus Q= 0,6 m³/h	415	32 x 4,7 mm
C2.01.13	20	1,43	4,5	Flamco LogoPlus Q= 0,6 m³/h	305	32 x 4,7 mm

Legenda ÚT

- Hlavní rozvod otopné vody okruhu vytápění objektu. Rozvod z ocelového potrubí spojovaného svařováním s tepelnou izolací veden v šachtě není-li na výkrese vyznačeno jinak. Dimenze dopojení jednotlivých patrových rozdělovačů viz Schéma hlavních rozvodů.
- Rozvod otopné vody pro napojení jednotlivých bytů. Rozvod z plastového potrubí s kyslíkovou bariérou Rehau Rautitan stabil s tepelnou izolací veden v podlaze není-li na výkrese vyznačeno jinak. Nekótované úseky jsou ø32x4,7 mm.
- Ocelové deskové otopné těleso Korado Radik Plan VK (VKL). Značeno: typ/výška/délka (typ VK není-li na výkrese vyznačeno jinak) Na rozvod otopné vody napojeno ze zdi pomocí rohových regulačních šroubení IMI Heimeier Regulux. Vybaveno termostatickou hlavicí Danfoss Redia M30x1,5.
- Koupelnové otopné těleso Korado Koralux Linear Comfort–M. Na rozvod otopné vody napojeno ze zdi pomocí rohové připojovací sady Korado HM s termostatickou hlavicí. S PŘÍPRAVOU pro napojení el. topné patrony s regulátorem teploty Korado Z–KT7R–400. Značeno: typ výška.šířka
- Rozvod jednotlivých okruhů podlahového vytápění. Rozvod z plastového potrubí Rehau Rautherm S 17x2 veden v podlaze.
- P XY — Okruh podlahového vytápění číslo Y napojen na rozdělovač číslo X.
- Hranice prostoru vytápěného podlahovým vytápěním, hranice jednotlivých okruhů podlahového vytápění.
- Rozdělovač podlahového vytápění Rehau HKV–D. Umístěn ve skříni rozdělovače Rehau.
- Prostorový termostat podlahového vytápění s externím čidlem teploty podlahy – dodávka EL.

Poznámky:

- REALIZACE SYSTÉMU VYTÁPĚNÍ MUSÍ PROBÍHAT KOORDINOVANĚ S OSTATNÍMI PROFESEMI A POŽADAVKY STAVEBNĚ – ARCHITEKTONICKÉHO ŘEŠENÍ, A TO ZEJMÉNA S NOMINOVANÝMI PŘÍPRAVAMI PRO INTERIÉR A JEHO KONCOVÝMI PRVKY.
- PATROVÉ ROZVODY PRO VYTÁPĚNÍ BYTŮ A NEBYTOVÝCH PROSTOR BUDOU PROVEDENY Z PLASTOVÉHO POTRUBÍ S KYSLÍKOVOU BARIÉROU REHAU RAUTITAN STABIL. POTRUBÍ BUDE SPOJOVÁNO NEROZEBÍRATELNÝMI SPOJI PRO ULOŽENÍ V PODLAZE.
- HLAVNÍ ROZVODY VEDENÉ POD STROPEM V 1.PP, STOUPAČKY A DOPOJENÍ PATROVÝCH ROZDĚLOVAČŮ BUDOU VYTVOŘENY Z OCELOVÉHO POTRUBÍ (DO DN50 TRUBKY ZÁVITOVÉ BĚŽNÉ PODLE ČSN 42 5710, OD DN60 TRUBKY HLADKÉ PODLE ČSN 42 5715). POTRUBÍ DN65 JE 76x3,2 MM.
- PATROVÉ ROZDĚLOVAČE BUDOU DOPOJENY PANCÉŘOVANÝMI HADICEMI NEBO JINÝM PRVKEM, KTERÝ UMOŽNÍ KOMPENZACI DÉLKOVÉ ROZTAŽNOSTI STOUPAČKY.
- POTRUBÍ ÚT BUDE OPATŘENO PŘÍSLUŠNOU TLOUŠŤKOU TEPELNÉ IZOLACE. NA ROZVODY V PODLAZE BUDE POUŽITA POLYETYLENOVÁ IZOLACE. PRO VOLNÉ ROZVODY PAK MINERÁLNÍ IZOLACE S HLINÍKOVÝM POVRCHEM.
- ODVZDUŠNĚNÍ BUDE MOŽNÉ NA OTOPNÝCH TĚLESECH A NA NEJVYŠŠÍCH MÍSTECH SOUSTAVY (KDE MUSÍ BÝT OSAZENY ODVZDUŠŇOVACÍ VENTILY).
- VYPOUŠTĚNÍ BUDE MOŽNÉ NA VYPOUŠTĚCÍCH KOHOUTECH NA NEJNIŽŠÍCH MÍSTECH SOUSTAVY.
- KOTVENÍ POTRUBÍ BUDE ŘEŠENO DODAVATELSKOU DOKUMENTACÍ (STANDARD HILTI, SILKA).
- V MÍSTNOSTECH VYBAVENÝCH PODLAHOVÝM VYTÁPĚNÍM BUDOU INSTALOVÁNY PROSTOROVÉ TERMOSTATY S ČIDLEM TEPLOTY PODLAHY V DODÁVCE EL. EL. BUDE OVLÁDAT TERMOPOHONY VENTILŮ NA ROZDĚLOVAČI PODLAHOVÉHO VYTÁPĚNÍ. TERMOPOHONY S PŘIPOJOVACÍM ZÁVITEM M30X1,5, PROSTOROVÉ TERMOSTATY S ČIDLEM TEPLOTY PODLAHY A KABELOVÉ PROPOJENÍ – DODÁVKA EL. EL. ZAJISTÍ ŘÍZENÍ TEPLOTY V JEDNOTLIVÝCH MÍSTNOSTECH.
- PŘI NÁVRHU PODLAHOVÉHO VYTÁPĚNÍ BYLO UVAŽOVÁNO S TĚMITO NÁŠLAPNÝMI VRSTVAMI:
  - KERAMICKÁ DLAŽBA R_{max}= 0,015 m²K/W
  - VINYLOVÁ PODLAHA R_{max}= 0,05 m²K/W
- VŠECHNY NÁŠLAPNÉ VRSTVY MUSÍ BÝT URČENY PRO PODLAHOVÉ VYTÁPĚNÍ !!!

Teplotní spád otopné vody okruhu přípravy TV 70/30 °C
Teplotní spád otopné vody okruhu vytápění objektu 43/33 °C

MINIMÁLNÍ TLOUŠŤKY TEPELNÉ IZOLACE
(λ = 0,038 W/m2K)

VOLNĚ VEDENÉ POTRUBÍ

DIMENZE	TLOUŠŤKA
DN12	20 mm
DN15, ø16,2x2,6	30 mm
DN20, ø20x2,9	30 mm
DN25, ø25x3,7	40 mm
DN32, ø32x4,7	40 mm
DN40, ø40x6	40 mm
DN50	50 mm
DN65	60 mm

V MÍSTECH KŘÍŽENÍ A PROSTUPŮ JE MOŽNÉ TEPELNOU IZOLACI OSLABIT

POTRUBÍ VEDENÉ VE ZDI A V PODLAZE

DIMENZE	TLOUŠŤKA
DN12	13 mm
DN15, ø16,2x2,6	13 mm
DN20, ø20x2,9	13 mm
DN25, ø25x3,7	13 mm
DN32, ø32x4,7	9 mm
DN40, ø40x6	20 mm
DN50	20 mm
DN65	20 mm

V MÍSTECH KŘÍŽENÍ A PROSTUPŮ JE MOŽNÉ TEPELNOU IZOLACI OSLABIT

Revize	Popis revize	Datum

severka

± 0,000 = 224,62 m.n.m (BPV)

stavba
BD Na Mariánské cestě - 2. etapa

stupeň
Dokumentace pro provádění stavby

zpracovatel
TZB DESIGN
TZB design s.r.o.
projekční kancelář TZB
Malý Okrouhlík 7/1039, 182 00 Praha 8
e-mail: mysicka@tzb-design.cz
mobil: +420 732 933 758
www.tzb-design.cz

zodpovědný projektant
Ing. Jan Myšička

vypracoval
Jan Svatoň

stavební objekt
SO03 - Bytový dům D2 a C2

část
D.1.2.4 - Vytápění, chlazení a vzduchotechnika

profesní díl / členění části
01 - Vytápění

investor
DOMOPLAN a.s.
Trnitá 543/16, Brno, 602 00

generální projektant
BK engineering project s.r.o.
Hanusova 347/16
140 00 Praha 4
info@bkproject.cz

hlavní inženýr projektu
Ing. Libor Doležal

datum 09/2025
x A4 45
měřítko 1:50
číslo paré

PŮDORYS 1NP

zakázka	stupeň	s.objekt	část	členění	č. výkresu	revize
365	50	SO03	D.1.2.4	2.1	002	