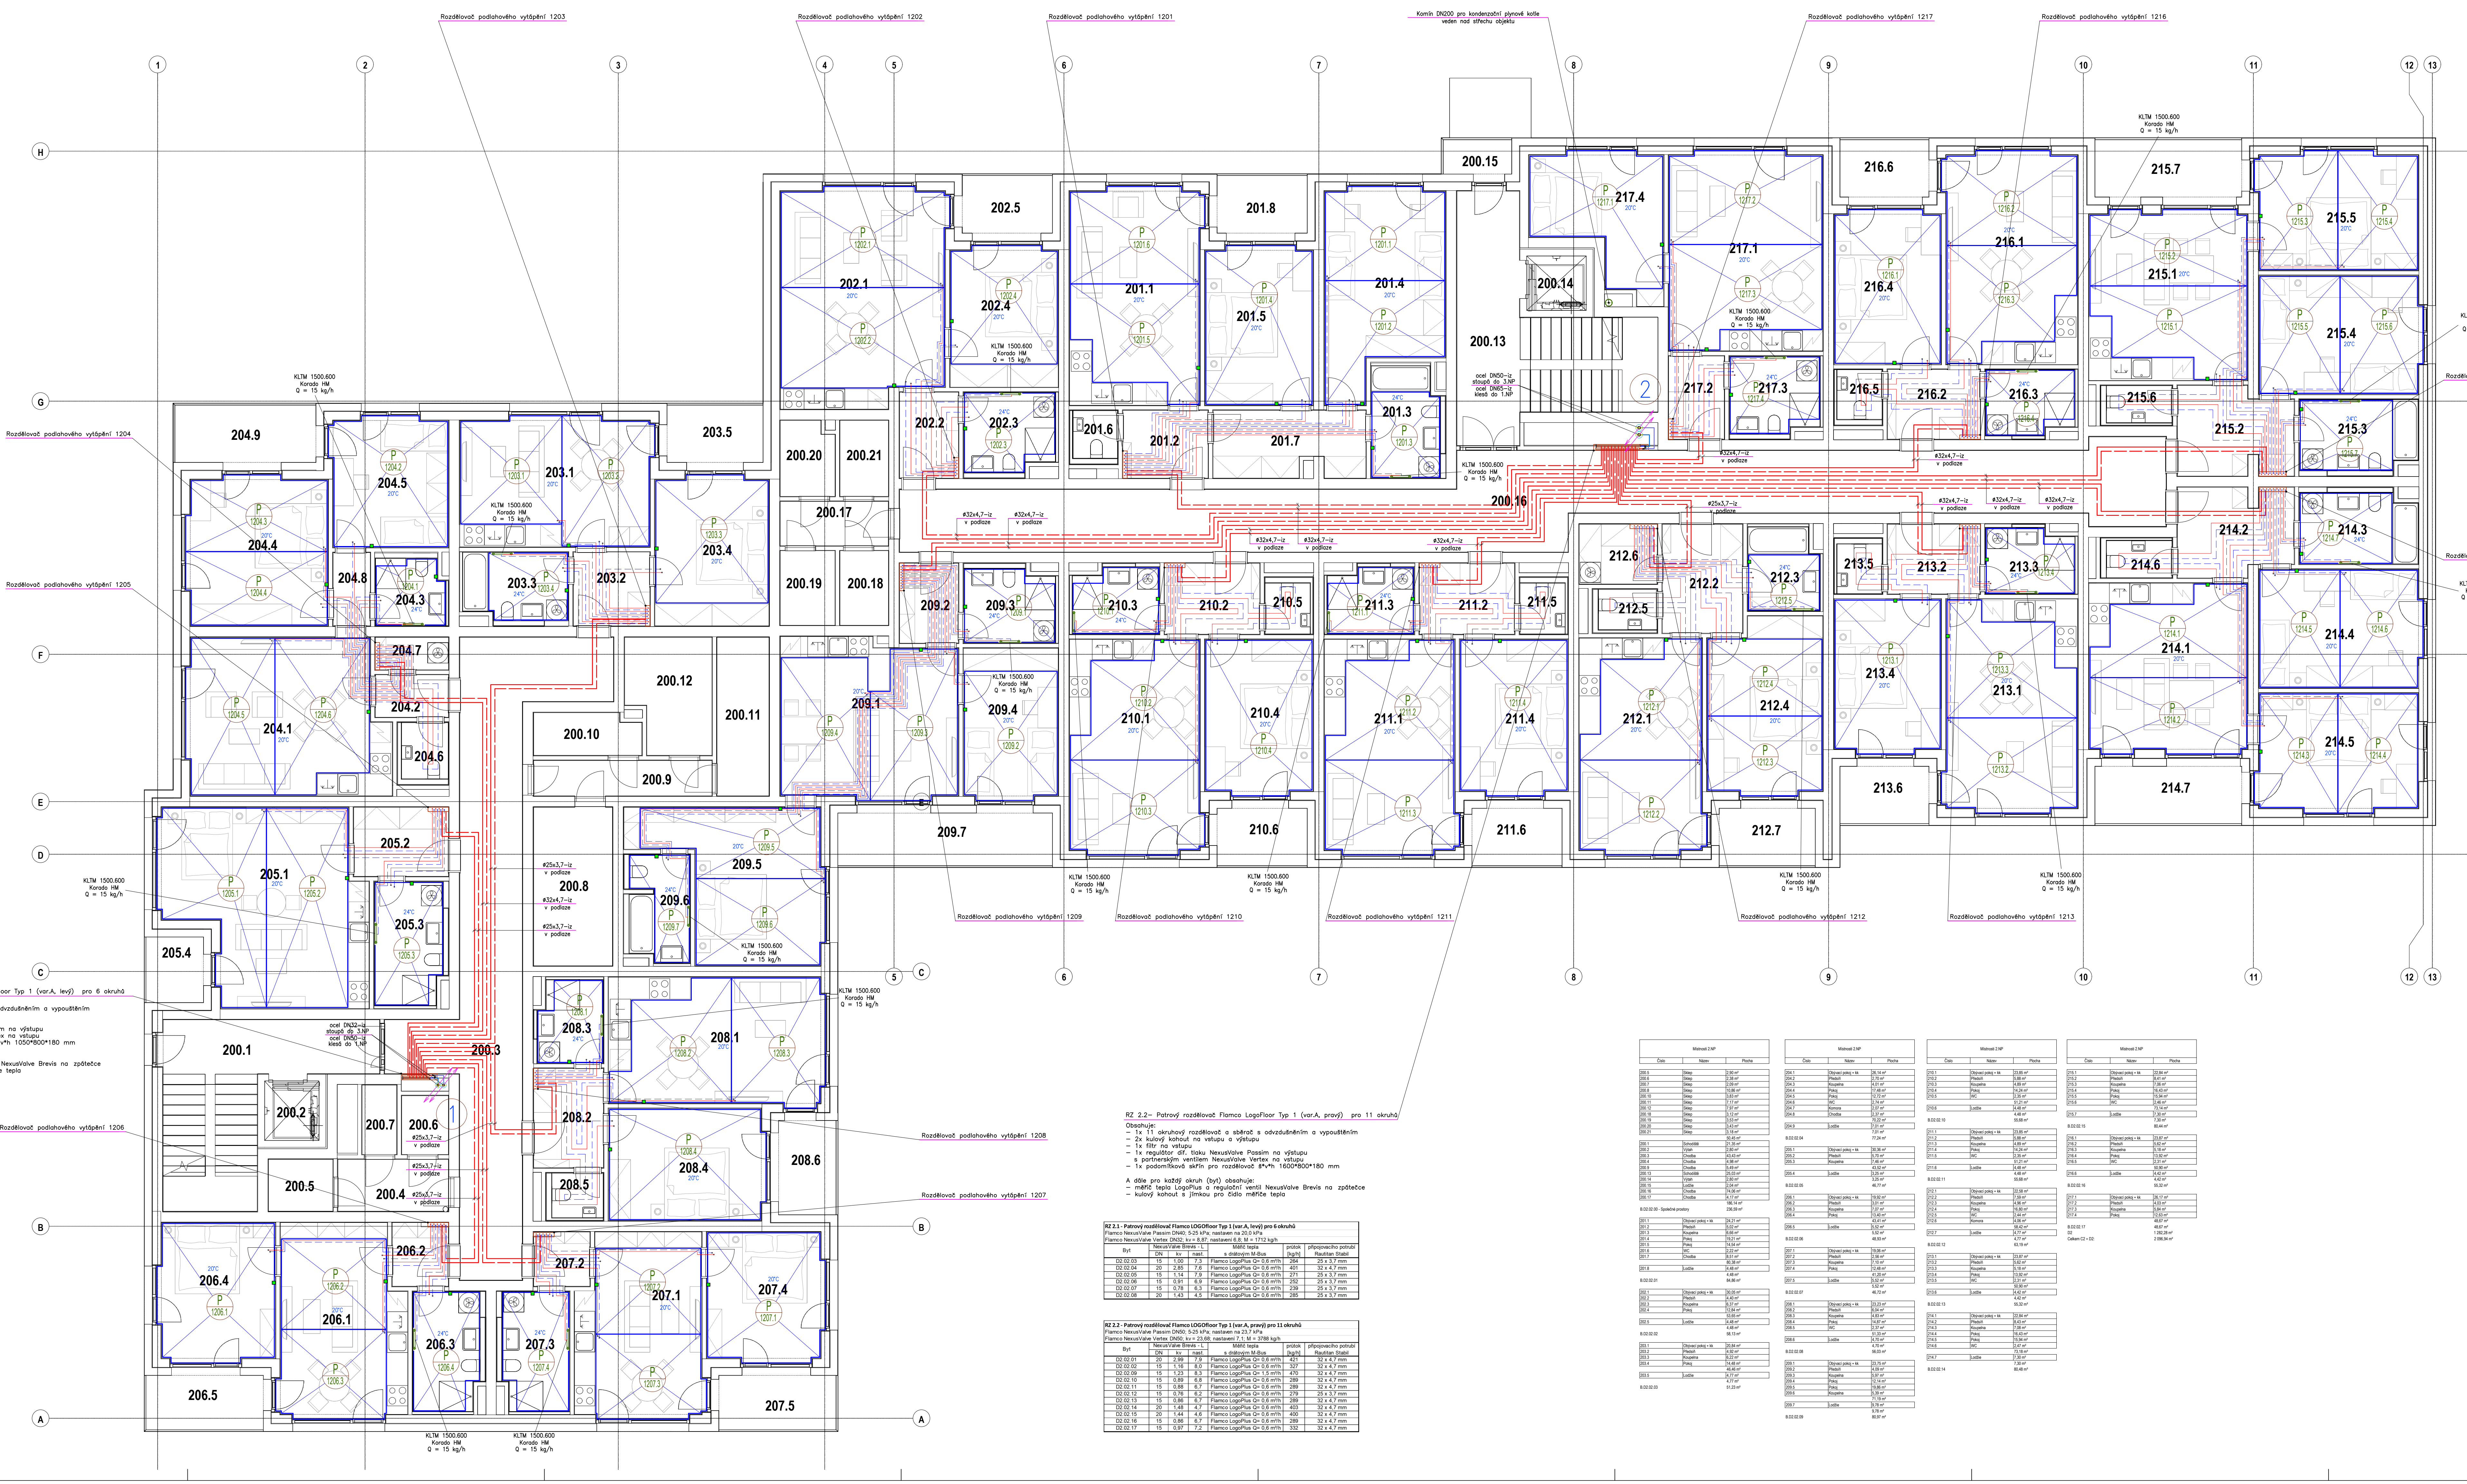
Rozdělovač podlahového vytápění 1203
Rozdělovač podlahového vytápění 1202
Rozdělovač podlahového vytápění 1201
Komín DN200 pro kondenzační plynové kotle veden nad střechu objektu
Rozdělovač podlahového vytápění 1217
Rozdělovač podlahového vytápění 1216
Rozdělovač podlahového vytápění 1215
Rozdělovač podlahového vytápění 1214
Rozdělovač podlahového vytápění 1204
Rozdělovač podlahového vytápění 1205
Rozdělovač podlahového vytápění 1206
Rozdělovač podlahového vytápění 1207
Rozdělovač podlahového vytápění 1208
Rozdělovač podlahového vytápění 1209
Rozdělovač podlahového vytápění 1210
Rozdělovač podlahového vytápění 1211
Rozdělovač podlahového vytápění 1212
Rozdělovač podlahového vytápění 1213
KLTM 1500.600 Korado HM Q = 15 kg/h
ocel DN50–iz stoupá do 3.NP ocel DN65–iz klesá do 1.NP
ocel DN32–iz stoupá do 3.NP ocel DN50–iz klesá do 1.NP
ø32x4,7–iz v podlaze
ø25x3,7–iz v podlaze
1
2
A
B
C
D
E
F
G
H
1
2
3
4
5
6
7
8
9
10
11
12
13

RZ 2.1– Patrový rozdělovač Flamco LogoFloor Typ 1 (var.A, levý) pro 6 okruhů

Obsahuje:
- 1x 6 okruhový rozdělovač a sběrač s odvzdušněním a vypouštěním
- 2x kulový kohout na vstupu a výstupu
- 1x filtr na vstupu
- 1x regulátor dif. tlaku NexusValve Passim na výstupu s partnerským ventilem NexusValve Vertex na vstupu
- 1x podomítková skříň pro rozdělovač š*v*h 1050*800*180 mm

A dále pro každý okruh (byt) obsahuje:
- měřič tepla LogoPlus a regulační ventil NexusValve Brevis na zpátečce
- kulový kohout s jímkou pro čidlo měřiče tepla

RZ 2.2– Patrový rozdělovač Flamco LogoFloor Typ 1 (var.A, pravý) pro 11 okruhů

Obsahuje:
- 1x 11 okruhový rozdělovač a sběrač s odvzdušněním a vypouštěním
- 2x kulový kohout na vstupu a výstupu
- 1x filtr na vstupu
- 1x regulátor dif. tlaku NexusValve Passim na výstupu s partnerským ventilem NexusValve Vertex na vstupu
- 1x podomítková skříň pro rozdělovač š*v*h 1050*800*180 mm

A dále pro každý okruh (byt) obsahuje:
- měřič tepla LogoPlus a regulační ventil NexusValve Brevis na zpátečce
- kulový kohout s jímkou pro čidlo měřiče tepla

RZ 2.1 - Patrový rozdělovač Flamco LOGOfloor Typ 1 (var.A, levý) pro 6 okruhů
Flamco NexusValve Passim DN40; 5-25 kPa; nastaven na 20,0 kPa
Flamco NexusValve Vertex DN32; kv = 8,87; nastavení 6,8; M = 1712 kg/h

Byt	NexusValve Brevis - L DN	kv	nast.	Měřič tepla s drátovým M-Bus	průtok [kg/h]	připojovacího potrubí Rautitan Stabil
D2.02.03	15	1,00	7,3	Flamco LogoPlus Q= 0,6 m³/h	264	25 x 3,7 mm
D2.02.04	20	2,85	7,6	Flamco LogoPlus Q= 0,6 m³/h	401	32 x 4,7 mm
D2.02.05	15	1,14	7,9	Flamco LogoPlus Q= 0,6 m³/h	271	25 x 3,7 mm
D2.02.06	15	0,91	6,9	Flamco LogoPlus Q= 0,6 m³/h	252	25 x 3,7 mm
D2.02.07	15	0,78	6,3	Flamco LogoPlus Q= 0,6 m³/h	239	25 x 3,7 mm
D2.02.08	20	1,43	4,5	Flamco LogoPlus Q= 0,6 m³/h	285	25 x 3,7 mm

RZ 2.2 - Patrový rozdělovač Flamco LOGOfloor Typ 1 (var.A, pravý) pro 11 okruhů
Flamco NexusValve Passim DN50; 5-25 kPa; nastaven na 23,7 kPa
Flamco NexusValve Vertex DN50; kv = 23,68; nastavení 7,1; M = 3788 kg/h

Byt	NexusValve Brevis - L DN	kv	nast.	Měřič tepla s drátovým M-Bus	průtok [kg/h]	připojovacího potrubí Rautitan Stabil
D2.02.01	20	2,99	7,9	Flamco LogoPlus Q= 0,6 m³/h	421	32 x 4,7 mm
D2.02.02	15	1,16	8,0	Flamco LogoPlus Q= 0,6 m³/h	327	32 x 4,7 mm
D2.02.09	15	1,23	8,3	Flamco LogoPlus Q= 1,5 m³/h	470	32 x 4,7 mm
D2.02.10	15	0,89	6,8	Flamco LogoPlus Q= 0,6 m³/h	289	32 x 4,7 mm
D2.02.11	15	0,88	6,7	Flamco LogoPlus Q= 0,6 m³/h	289	32 x 4,7 mm
D2.02.12	15	0,76	6,2	Flamco LogoPlus Q= 0,6 m³/h	279	25 x 3,7 mm
D2.02.13	15	0,86	6,7	Flamco LogoPlus Q= 0,6 m³/h	289	32 x 4,7 mm
D2.02.14	20	1,48	4,7	Flamco LogoPlus Q= 0,6 m³/h	403	32 x 4,7 mm
D2.02.15	20	1,44	4,6	Flamco LogoPlus Q= 0,6 m³/h	400	32 x 4,7 mm
D2.02.16	15	0,86	6,7	Flamco LogoPlus Q= 0,6 m³/h	289	32 x 4,7 mm
D2.02.17	15	0,97	7,2	Flamco LogoPlus Q= 0,6 m³/h	332	32 x 4,7 mm

Místnosti 2.NP		
Číslo	Název	Plocha
200.5	Sklep	2,90 m²
200.6	Sklep	2,38 m²
200.7	Sklep	2,09 m²
200.8	Sklep	10,86 m²
200.10	Sklep	3,83 m²
200.11	Sklep	7,17 m²
200.12	Sklep	7,97 m²
200.18	Sklep	3,12 m²
200.19	Sklep	3,53 m²
200.20	Sklep	3,43 m²
200.21	Sklep	3,18 m²
		50,45 m²
200.1	Schodiště	21,35 m²
200.2	Výtah	2,80 m²
200.3	Chodba	43,43 m²
200.4	Chodba	4,98 m²
200.9	Chodba	5,49 m²
200.13	Schodiště	25,03 m²
200.14	Výtah	2,80 m²
200.15	Lodžie	2,04 m²
200.16	Chodba	74,06 m²
200.17	Chodba	4,17 m²
		186,14 m²
B.D2.02.00 - Společné prostory		236,59 m²
201.1	Obývací pokoj + kk	24,21 m²
201.2	Předsíň	5,02 m²
201.3	Koupelna	6,66 m²
201.4	Pokoj	19,21 m²
201.5	Pokoj	14,54 m²
201.6	WC	2,22 m²
201.7	Chodba	8,51 m²
		80,38 m²
201.8	Lodžie	4,48 m²
		4,48 m²
B.D2.02.01		84,86 m²
202.1	Obývací pokoj + kk	30,05 m²
202.2	Předsíň	4,40 m²
202.3	Koupelna	6,37 m²
202.4	Pokoj	12,84 m²
		53,65 m²
202.5	Lodžie	4,48 m²
		4,48 m²
B.D2.02.02		58,13 m²
203.1	Obývací pokoj + kk	20,84 m²
203.2	Předsíň	4,92 m²
203.3	Koupelna	6,22 m²
203.4	Pokoj	14,48 m²
		46,46 m²
203.5	Lodžie	4,77 m²
		4,77 m²
B.D2.02.03		51,23 m²

Místnosti 2.NP		
Číslo	Název	Plocha
204.1	Obývací pokoj + kk	26,14 m²
204.2	Předsíň	2,70 m²
204.3	Koupelna	4,01 m²
204.4	Pokoj	17,48 m²
204.5	Pokoj	12,72 m²
204.6	WC	2,74 m²
204.7	Komora	2,07 m²
204.8	Chodba	2,37 m²
		70,22 m²
204.9	Lodžie	7,01 m²
		7,01 m²
B.D2.02.04		77,24 m²
205.1	Obývací pokoj + kk	30,36 m²
205.2	Předsíň	5,70 m²
205.3	Koupelna	7,46 m²
		43,52 m²
205.4	Lodžie	3,25 m²
		3,25 m²
B.D2.02.05		46,77 m²
206.1	Obývací pokoj + kk	19,92 m²
206.2	Předsíň	3,01 m²
206.3	Koupelna	7,07 m²
206.4	Pokoj	13,40 m²
		43,41 m²
206.5	Lodžie	5,52 m²
		5,52 m²
B.D2.02.06		48,93 m²
207.1	Obývací pokoj + kk	19,06 m²
207.2	Předsíň	2,56 m²
207.3	Koupelna	7,10 m²
207.4	Pokoj	12,48 m²
		41,20 m²
207.5	Lodžie	5,52 m²
		5,52 m²
B.D2.02.07		46,72 m²
208.1	Obývací pokoj + kk	23,23 m²
208.2	Předsíň	6,04 m²
208.3	Koupelna	4,83 m²
208.4	Pokoj	14,87 m²
208.5	WC	2,37 m²
		51,33 m²
208.6	Lodžie	4,70 m²
		4,70 m²
B.D2.02.08		56,03 m²
209.1	Obývací pokoj + kk	23,75 m²
209.2	Předsíň	4,09 m²
209.3	Koupelna	5,97 m²
209.4	Pokoj	12,14 m²
209.5	Pokoj	19,86 m²
209.6	Koupelna	5,39 m²
		71,19 m²
209.7	Lodžie	9,78 m²
		9,78 m²
B.D2.02.09		80,97 m²

Místnosti 2.NP		
Číslo	Název	Plocha
210.1	Obývací pokoj + kk	23,85 m²
210.2	Předsíň	5,88 m²
210.3	Koupelna	4,89 m²
210.4	Pokoj	14,24 m²
210.5	WC	2,35 m²
		51,21 m²
210.6	Lodžie	4,48 m²
		4,48 m²
B.D2.02.10		55,68 m²
211.1	Obývací pokoj + kk	23,85 m²
211.2	Předsíň	5,88 m²
211.3	Koupelna	4,89 m²
211.4	Pokoj	14,24 m²
211.5	WC	2,35 m²
		51,21 m²
211.6	Lodžie	4,48 m²
		4,48 m²
B.D2.02.11		55,68 m²
212.1	Obývací pokoj + kk	22,58 m²
212.2	Předsíň	7,59 m²
212.3	Koupelna	4,96 m²
212.4	Pokoj	16,80 m²
212.5	WC	2,44 m²
212.6	Komora	4,06 m²
		58,42 m²
212.7	Lodžie	4,77 m²
		4,77 m²
B.D2.02.12		63,19 m²
213.1	Obývací pokoj + kk	23,87 m²
213.2	Předsíň	5,62 m²
213.3	Koupelna	5,18 m²
213.4	Pokoj	13,92 m²
213.5	WC	2,31 m²
		50,90 m²
213.6	Lodžie	4,42 m²
		4,42 m²
B.D2.02.13		55,32 m²
214.1	Obývací pokoj + kk	22,84 m²
214.2	Předsíň	8,43 m²
214.3	Koupelna	7,08 m²
214.4	Pokoj	16,43 m²
214.5	Pokoj	15,94 m²
214.6	WC	2,47 m²
		73,18 m²
214.7	Lodžie	7,30 m²
		7,30 m²
B.D2.02.14		80,48 m²

Místnosti 2.NP		
Číslo	Název	Plocha
215.1	Obývací pokoj + kk	22,84 m²
215.2	Předsíň	8,41 m²
215.3	Koupelna	7,06 m²
215.4	Pokoj	16,43 m²
215.5	Pokoj	15,94 m²
215.6	WC	2,46 m²
		73,14 m²
215.7	Lodžie	7,30 m²
		7,30 m²
B.D2.02.15		80,44 m²
216.1	Obývací pokoj + kk	23,87 m²
216.2	Předsíň	5,62 m²
216.3	Koupelna	5,18 m²
216.4	Pokoj	13,92 m²
216.5	WC	2,31 m²
		50,90 m²
216.6	Lodžie	4,42 m²
		4,42 m²
B.D2.02.16		55,32 m²
217.1	Obývací pokoj + kk	26,17 m²
217.2	Předsíň	4,03 m²
217.3	Koupelna	5,84 m²
217.4	Pokoj	12,63 m²
		48,67 m²
B.D2.02.17		48,67 m²
D2		1 282,28 m²
Celkem C2 + D2:		2 096,94 m²

Rozdělovače podlahového vytápění REHAU v 2.NP:

Číslo rozdělovače	Přívodní teplota	Typ rozdělovače	Skříň rozdělovače	Tlaková ztráta [kPa]	Hmotnostní průtok [kg/h]
1201	43°C	HKV-D 7 nerez	AP 805	6,4	421
1202	43°C	HKV-D 5 nerez	AP 605	5,8	327
1203	43°C	HKV-D 5 nerez	AP 605	3,2	264
1204	43°C	HKV-D 7 nerez	AP 805	4,1	401
1205	43°C	HKV-D 4 nerez	AP 605	5,8	271
1206	43°C	HKV-D 5 nerez	AP 605	5,1	252
1207	43°C	HKV-D 5 nerez	AP 605	4,0	239
1208	43°C	HKV-D 5 nerez	AP 605	6,9	285
1209	43°C	HKV-D 9 nerez	AP 805	2,0	470
1210	43°C	HKV-D 5 nerez	AP 605	6,0	289
1211	43°C	HKV-D 5 nerez	AP 605	6,0	289
1212	43°C	HKV-D 6 nerez	AP 805	1,8	279
1213	43°C	HKV-D 5 nerez	AP 605	5,4	289
1214	43°C	HKV-D 8 nerez	AP 805	2,0	403
1215	43°C	HKV-D 8 nerez	AP 805	1,8	400
1216	43°C	HKV-D 5 nerez	AP 605	5,6	289
1217	43°C	HKV-D 5 nerez	AP 605	3,5	332

PODLAHOVÉ VYTÁPĚNÍ v 2.NP

Číslo rozdělovače	Okruh	Plocha celková [m2]	Rozteč [mm]	Délka celková [m]	Průtok [kg/h]
1201	P 1201.1	9,4	150	89	61
	P 1201.2	9,4	150	81	61
	P 1201.3	4,9	100	67	54
	P 1201.4	14,4	150	111	93
	P 1201.5	10,7	150	78	70
	P 1201.6	10,7	150	86	70
1202	P 1202.1	14,0	150	109	91
	P 1202.2	14,0	150	102	91
	P 1202.3	5,7	100	62	63
	P 1202.4	10,7	150	82	70
1203	P 1203.1	9,4	150	75	61
	P 1203.2	9,4	150	71	61
	P 1203.3	12,1	150	90	79
	P 1203.4	4,5	100	54	50
1204	P 1204.1	3,6	100	48	40
	P 1204.2	12,7	150	100	82
	P 1204.3	8,8	150	76	57
	P 1204.4	8,8	150	74	57
	P 1204.5	11,7	150	95	76
	P 1204.6	11,7	150	97	76
1205	P 1205.1	14,0	150	108	91
	P 1205.2	14,0	150	102	91
	P 1205.3	6,7	100	75	76
1206	P 1206.1	13,6	150	104	88
	P 1206.2	8,2	150	61	53
	P 1206.3	8,2	150	65	53
	P 1206.4	6,3	100	69	43
1207	P 1207.1	12,7	150	97	82
	P 1207.2	7,7	150	57	50
	P 1207.3	7,7	150	61	50
	P 1207.4	6,3	100	69	43
1208	P 1208.1	4,1	100	46	45
	P 1208.2	10,1	150	72	66
	P 1208.3	10,1	150	88	66
	P 1208.4	14,6	150	116	95
1209	P 1209.1	5,3	100	61	58
	P 1209.2	10,2	150	79	66
	P 1209.3	10,5	150	78	68
	P 1209.4	10,5	150	82	68
	P 1209.5	9,5	150	88	62
	P 1209.6	9,5	150	94	62
	P 1209.7	3,9	100	76	58
1210	P 1210.1	4,4	100	49	49
	P 1210.2	10,5	150	75	68
	P 1210.3	10,5	150	90	68
	P 1210.4	14,0	150	112	91
1211	P 1211.1	4,4	100	48	49
	P 1211.2	10,5	150	75	68
	P 1211.3	10,5	150	90	68
	P 1211.4	14,0	150	112	91
1212	P 1212.1	9,8	150	83	64
	P 1212.2	9,8	150	84	64
	P 1212.3	7,5	150	67	49
	P 1212.4	7,5	150	62	49
	P 1212.5	3,4	100	44	41
1213	P 1213.1	13,7	150	108	89
	P 1213.2	10,5	150	90	68
	P 1213.3	10,5	150	75	68
	P 1213.4	4,5	100	50	50
1214	P 1214.1	10,1	150	87	66
	P 1214.2	10,1	150	82	66
	P 1214.3	7,9	150	72	51
	P 1214.4	7,9	150	77	51
	P 1214.5	8,1	150	60	53
	P 1214.6	8,1	150	64	53
	P 1214.7	5,5	100	60	51
1215	P 1215.1	9,9	150	86	64
	P 1215.2	9,9	150	81	64
	P 1215.3	7,9	150	72	51
	P 1215.4	7,9	150	77	51
	P 1215.5	8,1	150	60	53
	P 1215.6	8,1	150	64	53
	P 1215.7	5,5	100	60	51
1216	P 1216.1	13,8	150	109	90
	P 1216.2	10,5	150	90	68
	P 1216.3	10,5	150	75	68
	P 1216.4	4,5	100	50	50
1217	P 1217.1	12,0	150	91	80
	P 1217.2	12,1	150	94	79
	P 1217.3	12,1	150	88	79
	P 1217.4	5,5	100	63	81

Rozdělovače podlahového vytápění REHAU v 2.NP:

Číslo rozdělovače	Přívodní teplota	Typ rozdělovače	Skříň rozdělovače	Tlaková ztráta [kPa]	Hmotnostní průtok [kg/h]
2201	43°C	HKV-D 5 nerez	AP 605	3,9	224
2202	43°C	HKV-D 5 nerez	AP 605	6,1	280
2203	43°C	HKV-D 4 nerez	AP 605	1,8	206
2204	43°C	HKV-D 5 nerez	AP 605	2,3	245
2205	43°C	HKV-D 5 nerez	AP 605	2,3	245
2206	43°C	HKV-D 4 nerez	AP 605	1,8	206
2207	43°C	HKV-D 5 nerez	AP 605	6,1	280
2208	43°C	HKV-D 5 nerez	AP 605	6,4	285
2209	43°C	HKV-D 5 nerez	AP 605	2,9	258
2210	43°C	HKV-D 4 nerez	AP 605	2,0	210
2211	43°C	HKV-D 7 nerez	AP 805	7,6	459
2212	43°C	HKV-D 8 nerez	AP 805	1,9	410
2213	43°C	HKV-D 5 nerez	AP 605	6,4	298

PODLAHOVÉ VYTÁPĚNÍ v 2.NP

Číslo rozdělovače	Okruh	Plocha celková [m2]	Rozteč [mm]	Délka celková [m]	Průtok [kg/h]
2201	P 2201.1	12,2	150	98	82
	P 2201.2	7,5	150	67	49
	P 2201.3	7,5	150	60	49
	P 2201.4	4,5	100	55	31
2202	P 2202.1	14,1	150	112	91
	P 2202.2	10,0	150	85	65
	P 2202.3	10,0	150	76	65
	P 2202.4	4,1	100	47	45
2203	P 2203.1	10,1	150	81	66
	P 2203.2	10,1	150	75	66
	P 2203.3	6,0	100	66	61
2204	P 2204.1	10,9	150	85	71
	P 2204.2	8,8	150	69	57
	P 2204.3	8,8	150	65	57
	P 2204.4	6,8	100	73	46
2205	P 2205.1	10,9	150	85	71
	P 2205.2	8,8	150	69	57
	P 2205.3	8,8	150	65	57
	P 2205.4	6,8	100	73	46
2206	P 2206.1	6,0	100	66	61
	P 2206.2	10,1	150	75	66
	P 2206.3	10,1	150	81	66
2207	P 2207.1	14,1	150	112	91
	P 2207.2	10,0	150	85	65
	P 2207.3	10,0	150	76	65
	P 2207.4	4,1	100	47	45
2208	P 2208.1	14,3	150	113	93
	P 2208.2	10,3	150	87	67
	P 2208.3	10,3	150	78	67
	P 2208.4	4,1	100	47	45
2209	P 2209.1	4,5	100	51	50
	P 2209.2	11,6	150	88	75
	P 2209.3	9,2	150	78	60
	P 2209.4	9,2	150	79	60
2210	P 2210.1	6,0	100	66	61
	P 2210.2	10,4	150	77	68
	P 2210.3	10,4	150	84	68
2211	P 2211.1	11,0	150	77	71
	P 2211.2	11,0	150	86	71
	P 2211.3	13,0	150	105	84
	P 2211.4	9,8	150	81	64
	P 2211.5	5,4	100	73	60
	P 2211.6	14,8	150	124	96
2212	P 2212.1	10,0	150	85	65
	P 2212.2	10,0	150	80	65
	P 2212.3	7,9	150	70	51
	P 2212.4	7,9	150	75	51
	P 2212.5	7,9	150	58	51
	P 2212.6	7,9	150	63	51
	P 2212.7	5,6	100	62	62
2213	P 2213.1	14,5	150	109	94
	P 2213.2	5,7	100	72	58
	P 2213.3	10,2	150	78	66
	P 2213.4	10,2	150	83	66

Místnosti 2.NP		
Číslo	Název	Plocha
200.27	Sklep	3,36 m²
200.28	Sklep	3,28 m²
		6,64 m²
200.22	Schodiště	28,21 m²
200.23	Výtah	2,80 m²
200.24	Chodba	36,83 m²
200.25	Chodba	35,98 m²
200.26	Chodba	3,26 m²
		107,08 m²
B.C2.02.00 - Společné prostory		113,71 m²
201.1	Obývací pokoj + kk	17,27 m²
201.2	Předsíň	2,79 m²
201.3	Koupelna	5,15 m²
201.4	Pokoj	12,31 m²
201.5	Komora	3,22 m²
		40,74 m²
201.6	Lodžie	4,70 m²
		4,70 m²
B.C2.02.01		45,44 m²
202.1	Obývací pokoj + kk	23,06 m²
202.2	Předsíň	6,06 m²
202.3	Koupelna	4,75 m²
202.4	Pokoj	14,35 m²
202.5	WC	2,37 m²
		50,59 m²
202.6	Lodžie	4,62 m²
		4,62 m²
B.C2.02.02		55,21 m²
203.1	Obývací pokoj + kk	22,43 m²
203.2	Předsíň	3,59 m²
203.3	Koupelna	6,93 m²
		32,95 m²
203.4	Lodžie	2,83 m²
		2,83 m²
B.C2.02.03		35,78 m²
204.1	Obývací pokoj + kk	21,58 m²
204.2	Předsíň	2,77 m²
204.3	Koupelna	7,72 m²
204.4	Pokoj	12,03 m²
		44,11 m²
204.5	Lodžie	4,91 m²
		4,91 m²
B.C2.02.04		49,02 m²
205.1	Obývací pokoj + kk	21,61 m²
205.2	Předsíň	2,76 m²
205.3	Koupelna	7,76 m²
205.4	Pokoj	12,03 m²
		44,17 m²
205.5	Lodžie	4,91 m²
		4,91 m²
B.C2.02.05		49,09 m²

Místnosti 2.NP		
Číslo	Název	Plocha
206.1	Obývací pokoj + kk	22,43 m²
206.2	Předsíň	3,59 m²
206.3	Koupelna	6,93 m²
		32,95 m²
206.4	Lodžie	2,83 m²
		2,83 m²
B.C2.02.06		35,78 m²
207.1	Obývací pokoj + kk	23,07 m²
207.2	Předsíň	6,06 m²
207.3	Koupelna	4,75 m²
207.4	Pokoj	14,36 m²
207.5	WC	2,37 m²
		50,60 m²
207.6	Lodžie	4,62 m²
		4,62 m²
B.C2.02.07		55,23 m²
208.1	Obývací pokoj + kk	23,55 m²
208.2	Předsíň	5,81 m²
208.3	Koupelna	4,76 m²
208.4	Pokoj	14,57 m²
208.5	WC	2,28 m²
		50,96 m²
208.6	Lodžie	4,62 m²
		4,62 m²
B.C2.02.08		55,59 m²
209.1	Obývací pokoj + kk	21,28 m²
209.2	Předsíň	3,97 m²
209.3	Koupelna	5,21 m²
209.4	Pokoj	13,72 m²
209.5	WC	2,20 m²
		46,37 m²
209.6	Lodžie	5,32 m²
		5,32 m²
B.C2.02.09		51,69 m²
210.1	Obývací pokoj + kk	23,26 m²
210.2	Předsíň	3,65 m²
210.3	Koupelna	6,94 m²
		33,86 m²
210.4	Lodžie	2,81 m²
		2,81 m²
B.C2.02.10		36,66 m²
211.1	Obývací pokoj + kk	24,21 m²
211.2	Předsíň	3,30 m²
211.3	Koupelna	7,73 m²
211.4	Pokoj	14,96 m²
211.5	Pokoj	10,04 m²
211.6	Pokoj	15,12 m²
211.7	WC	2,74 m²
211.8	Chodba	5,78 m²
		83,88 m²
211.9	Lodžie	7,30 m²
		7,30 m²
B.C2.02.11		91,18 m²

Místnosti 2.NP		
Číslo	Název	Plocha
212.1	Obývací pokoj + kk	23,03 m²
212.2	Předsíň	7,83 m²
212.3	Koupelna	7,57 m²
212.4	Pokoj	15,96 m²
212.5	Pokoj	16,12 m²
212.6	WC	3,25 m²
		73,75 m²
212.7	Lodžie	7,30 m²
		7,30 m²
B.C2.02.12		81,05 m²
213.1	Obývací pokoj + kk	22,60 m²
213.2	Předsíň	8,26 m²
213.3	Koupelna	6,07 m²
213.4	Pokoj	17,15 m²
213.5	WC	2,33 m²
		56,41 m²
213.6	Lodžie	2,83 m²
		2,83 m²
B.C2.02.13		59,24 m²
C2		814,66 m²


Rozdělovač podlahového vytápění 2204
Rozdělovač podlahového vytápění 2203
Rozdělovač podlahového vytápění 2202
Rozdělovač podlahového vytápění 2201
Rozdělovač podlahového vytápění 2213
Rozdělovač podlahového vytápění 2212
Rozdělovač podlahového vytápění 2205
Rozdělovač podlahového vytápění 2206
Rozdělovač podlahového vytápění 2207
Rozdělovač podlahového vytápění 2208
Rozdělovač podlahového vytápění 2209
Rozdělovač podlahového vytápění 2210
Rozdělovač podlahového vytápění 2211
KLTM 1500.600 Korado HM Q = 15 kg/h
KLTM 1820.450 Korado HM Q = 16 kg/h
ocel DN40–iz stoupá do 3.NP ocel DN50–iz klesá do 1.NP
ocel DN32–iz stoupá do 3.NP ocel DN50–iz klesá do 1.NP
ø32x4,7–iz v podlaze
ø25x3,7–iz v podlaze
3
4
C1
D1
F
F1
G
G1
H
14
15
16
17
18
19
20
21
22
23
24
25

RZ 2.3– Patrový rozdělovač Flamco LogoFloor Typ 1 (var.A, levý) pro 8 okruhů

Obsahuje:
- 1x 8 okruhový rozdělovač a sběrač s odvzdušněním a vypouštěním
- 2x kulový kohout na vstupu a výstupu
- 1x filtr na vstupu
- 1x regulátor dif. tlaku NexusValve Passim na výstupu s partnerským ventilem NexusValve Vertex na vstupu
- 1x podomítková skříň pro rozdělovač š*v*h 1450*800*180 mm

A dále pro každý okruh (byt) obsahuje:
- měřič tepla LogoPlus a regulační ventil NexusValve Brevis na zpátečce
- kulový kohout s jímkou pro čidlo měřiče tepla

RZ 2.4– Patrový rozdělovač Flamco LogoFloor Typ 1 (var.A, levý) pro 5 okruhů

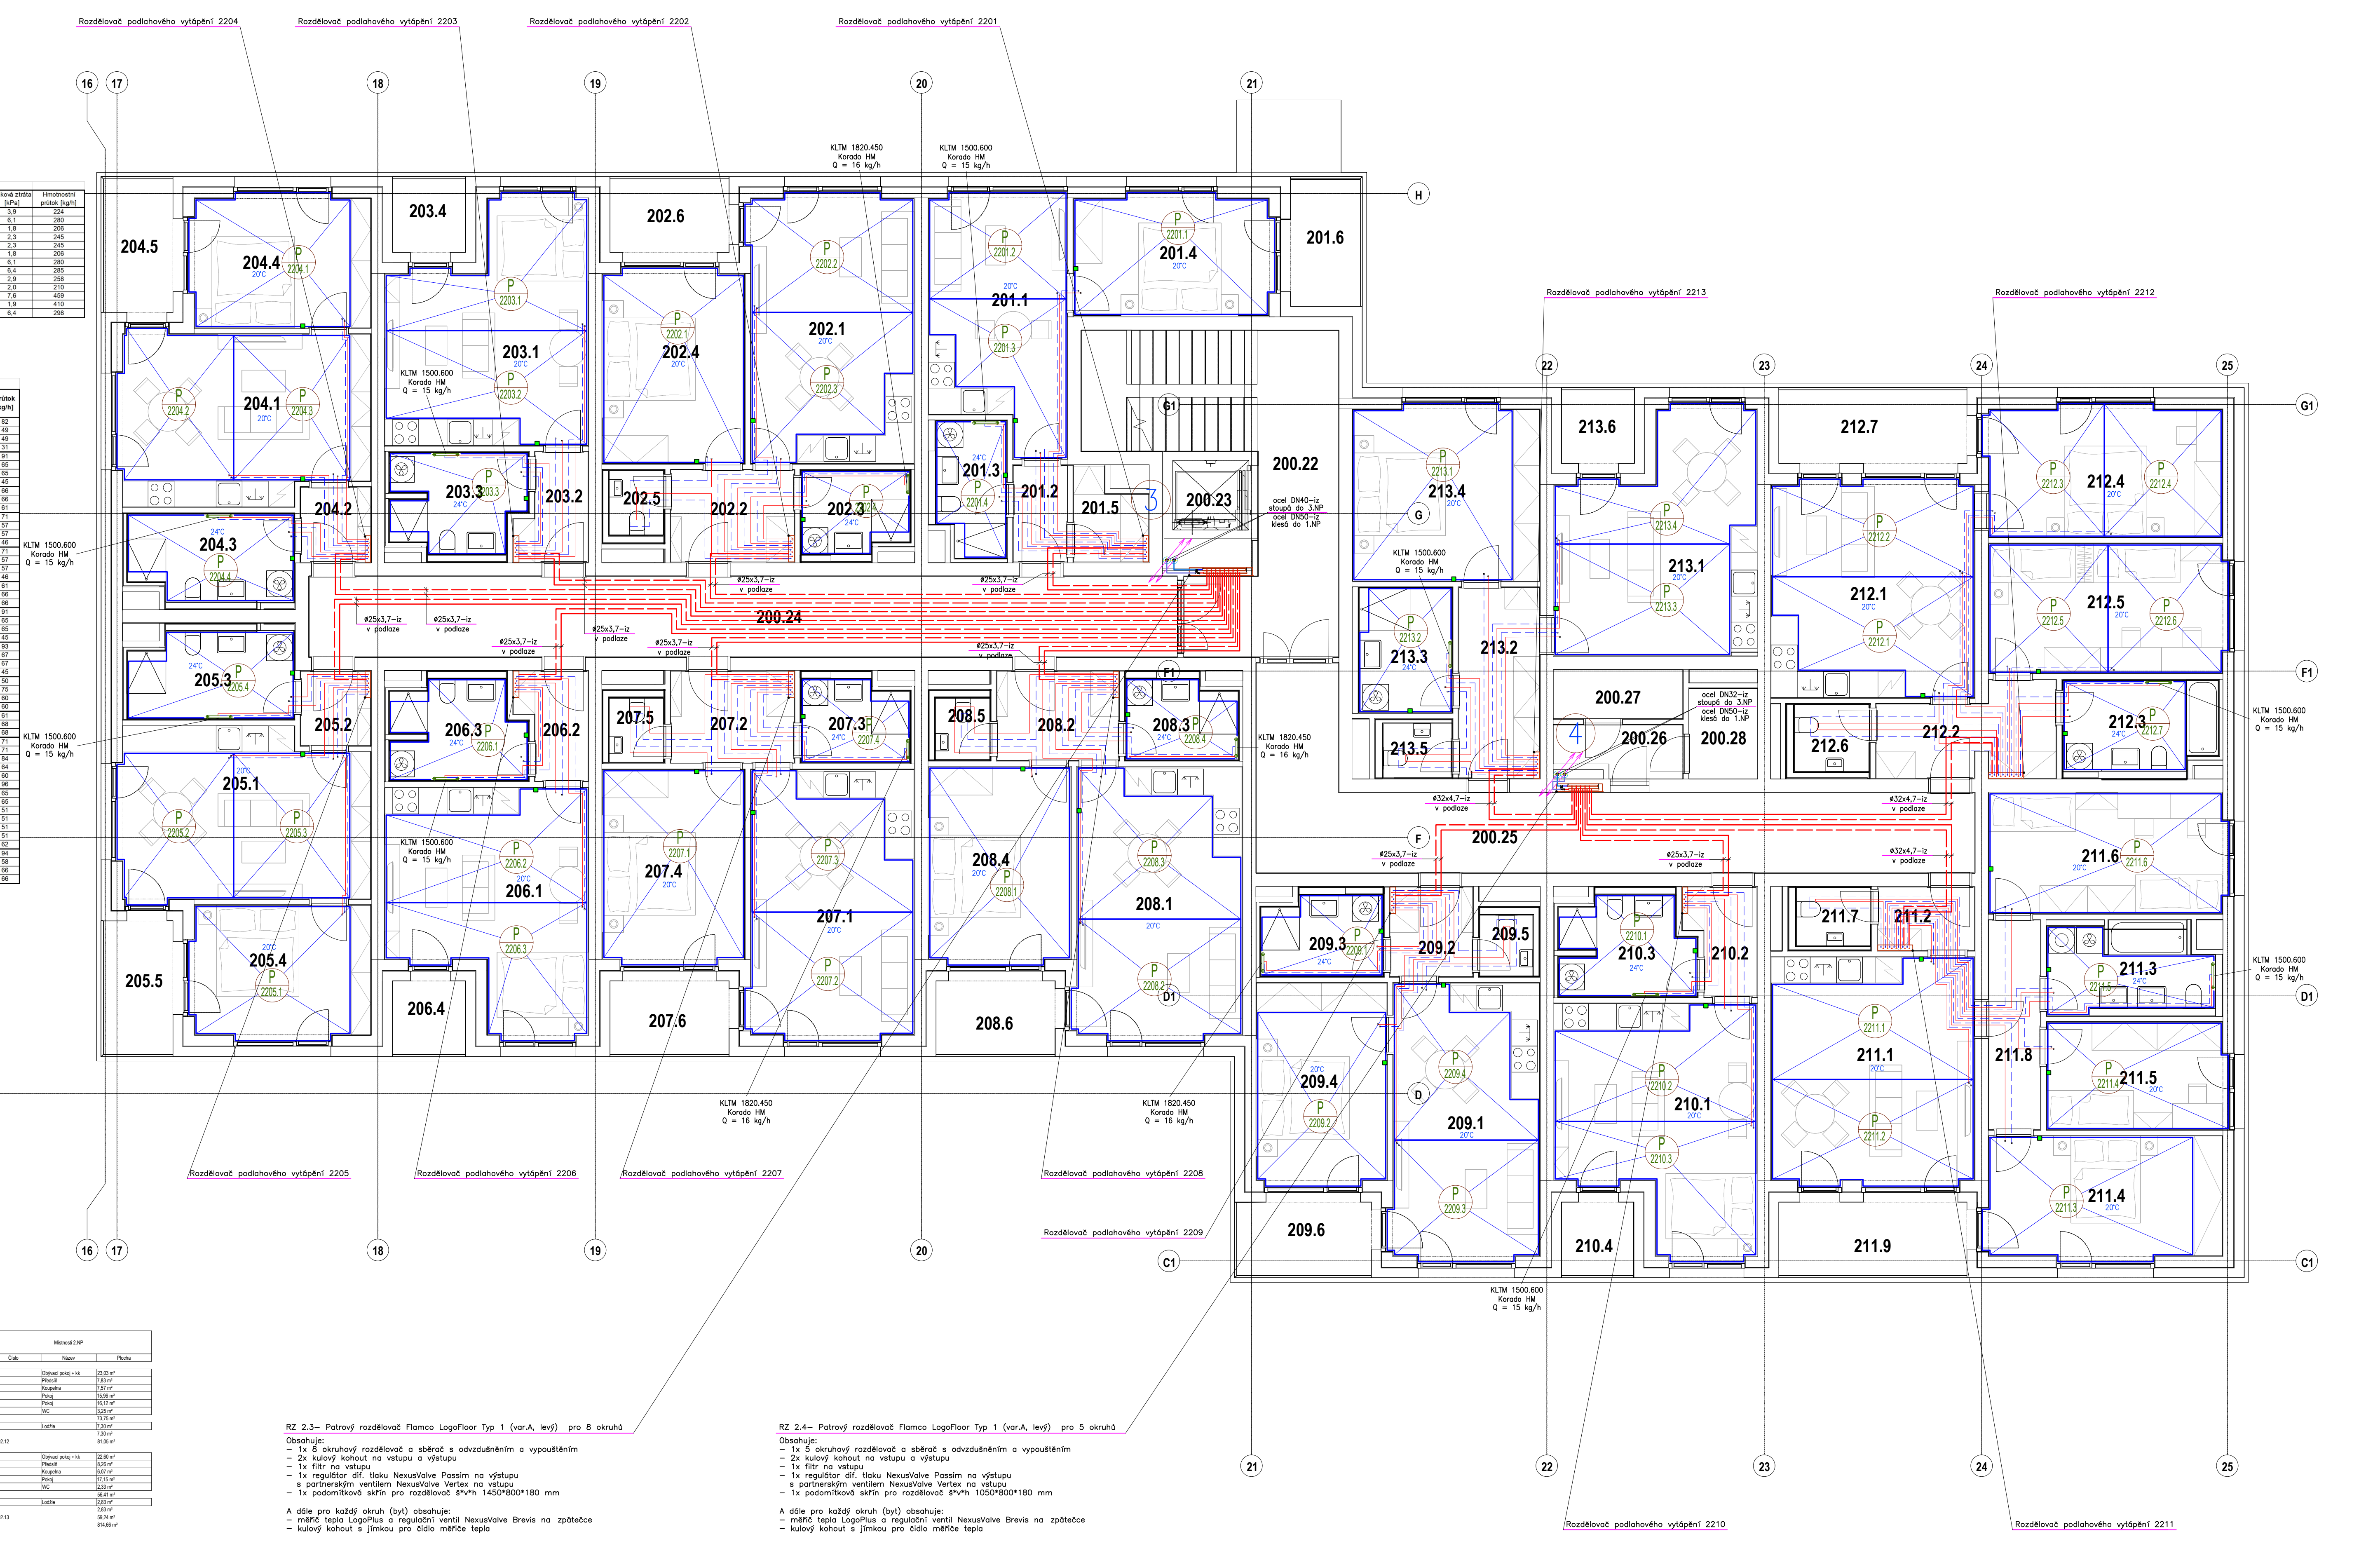Obsahuje:
- 1x 5 okruhový rozdělovač a sběrač s odvzdušněním a vypouštěním
- 2x kulový kohout na vstupu a výstupu
- 1x filtr na vstupu
- 1x regulátor dif. tlaku NexusValve Passim na výstupu s partnerským ventilem NexusValve Vertex na vstupu
- 1x podomítková skříň pro rozdělovač š*v*h 1050*800*180 mm

A dále pro každý okruh (byt) obsahuje:
- měřič tepla LogoPlus a regulační ventil NexusValve Brevis na zpátečce
- kulový kohout s jímkou pro čidlo měřiče tepla

RZ 2.3 - Patrový rozdělovač Flamco LOGOfloor Typ 1 (var.A, levý) pro 8 okruhů
Flamco NexusValve Passim DN40; 5-25 kPa; nastaven na 17,9 kPa
Flamco NexusValve Vertex DN32; kv = 6,75; nastavení 5,3; M = 1971 kg/h

Byt	NexusValve Brevis - L DN	kv	nast.	Měřič tepla s drátovým M-Bus	průtok [kg/h]	připojovacího potrubí Rautitan Stabil
C2.02.01	15	0,76	6,2	Flamco LogoPlus Q= 0,6 m³/h	224	25 x 3,7 mm
C2.02.02	20	1,90	5,7	Flamco LogoPlus Q= 0,6 m³/h	280	25 x 3,7 mm
C2.02.03	15	0,65	5,7	Flamco LogoPlus Q= 0,6 m³/h	206	25 x 3,7 mm
C2.02.04	15	0,96	7,1	Flamco LogoPlus Q= 0,6 m³/h	245	25 x 3,7 mm
C2.02.05	15	0,97	7,2	Flamco LogoPlus Q= 0,6 m³/h	245	25 x 3,7 mm
C2.02.06	15	0,65	5,7	Flamco LogoPlus Q= 0,6 m³/h	206	25 x 3,7 mm
C2.02.07	20	1,99	5,9	Flamco LogoPlus Q= 0,6 m³/h	280	25 x 3,7 mm
C2.02.08	20	1,77	5,4	Flamco LogoPlus Q= 0,6 m³/h	285	25 x 3,7 mm

RZ 2.4 - Patrový rozdělovač Flamco LOGOfloor Typ 1 (var.A, levý) pro 5 okruhů
Flamco NexusValve Passim DN40; 5-25 kPa; nastaven na 17,9 kPa
Flamco NexusValve Vertex DN32; kv = 10,49; nastavení 8,0; M = 1635 kg/h

Byt	NexusValve Brevis - L DN	kv	nast.	Měřič tepla s drátovým M-Bus	průtok [kg/h]	připojovacího potrubí Rautitan Stabil
C2.02.09	15	0,90	6,9	Flamco LogoPlus Q= 0,6 m³/h	258	25 x 3,7 mm
C2.02.10	15	0,63	5,6	Flamco LogoPlus Q= 0,6 m³/h	210	25 x 3,7 mm
C2.02.11	20	1,97	5,9	Flamco LogoPlus Q= 1,5 m³/h	459	32 x 4,7 mm
C2.02.12	20	2,91	7,7	Flamco LogoPlus Q= 0,6 m³/h	410	32 x 4,7 mm
C2.02.13	15	1,38	8,9	Flamco LogoPlus Q= 0,6 m³/h	298	32 x 4,7 mm

Legenda ÚT

▬ ▬	Hlavní rozvod otopné vody okruhu vytápění objektu. Rozvod z ocelového potrubí spojovaného svařováním s tepelnou izolací veden v šachtě není–li na výkrese vyznačeno jinak. Dimenze dopojení jednotlivých patrových rozdělovačů viz Schéma hlavních rozvodů.
▬ ▬	Rozvod otopné vody pro napojení jednotlivých bytů. Rozvod z plastového potrubí s kyslíkovou bariérou Rehau Rautitan stabil s tepelnou izolací veden v podlaze není–li na výkrese vyznačeno jinak. Nekótované úseky jsou ø32x4,7 mm.
⊕═⊕	Koupelnové otopné těleso Korado Koralux Linear Comfort–M. Na rozvod otopné vody napojeno ze zdi pomocí rohové připojovací sady Korado HM s termostatickou hlavicí. S PŘÍPRAVOU pro napájení el. topné patrony s regulátorem teploty Korado Z–KT7R–400. Značeno: typ výška.šířka
– –	Rozvod jednotlivých okruhů podlahového vytápění. Rozvod z plastového potrubí Rehau Rautherm S 17x2 veden v podlaze.
P X.Y	Okruh podlahového vytápění číslo Y napojen na rozdělovač číslo X.
▬	Hranice prostoru vytápěného podlahovým vytápěním, hranice jednotlivých okruhů podlahového vytápění.
▭	Rozdělovač podlahového vytápění Rehau HKV–D. Umístěn ve skříni rozdělovače Rehau.
🟩	Prostorový termostat podlahového vytápění s externím čidlem teploty podlahy – dodávka EL.

Poznámky:

- REALIZACE SYSTÉMU VYTÁPĚNÍ MUSÍ PROBÍHAT KOORDINOVANĚ S OSTATNÍMI PROFESEMI A POŽADAVKY STAVEBNĚ – ARCHITEKTONICKÉHO ŘEŠENÍ, A TO ZEJMÉNA S NOMINOVANÝMI PŘÍPRAVAMI PRO INTERIÉR A JEHO KONCOVÝMI PRVKY.
- PATROVÉ ROZVODY PRO VYTÁPĚNÍ BYTŮ A NEBYTOVÝCH PROSTOR BUDOU PROVEDENY Z PLASTOVÉHO POTRUBÍ S KYSLÍKOVOU BARIÉROU REHAU RAUTITAN STABIL. POTRUBÍ BUDE SPOJOVÁNO NEROZEBÍRATELNÝMI SPOJI PRO ULOŽENÍ V PODLAZE.
- HLAVNÍ ROZVODY VEDENÉ POD STROPEM V 1.PP, STOUPAČKY A DOPOJENÍ PATROVÝCH ROZDĚLOVAČŮ BUDOU VYTVOŘENY Z OCELOVÉHO POTRUBÍ (DO DN50 TRUBKY ZÁVITOVÉ BĚŽNÉ PODLE ČSN 42 5710, OD DN60 TRUBKY HLADKÉ PODLE ČSN 42 5715). POTRUBÍ DN65 JE 76x3,2 MM.
- PATROVÉ ROZDĚLOVAČE BUDOU DOPOJENY PANCÉŘOVANÝMI HADICEMI NEBO JINÝM PRVKEM, KTERÝ UMOŽNÍ KOMPENZACI DÉLKOVÉ ROZTAŽNOSTI STOUPAČKY.
- POTRUBÍ ÚT BUDE OPATŘENO PŘÍSLUŠNOU TLOUŠŤKOU TEPELNÉ IZOLACE. NA ROZVODY V PODLAZE BUDE POUŽITA POLYETYLENOVÁ IZOLACE. PRO VOLNÉ ROZVODY PAK MINERÁLNÍ IZOLACE S HLINÍKOVÝM POVRCHEM.
- ODVZDUŠNĚNÍ BUDE MOŽNÉ NA OTOPNÝCH TĚLESECH A NA NEJVYŠŠÍCH MÍSTECH SOUSTAVY (KDE MUSÍ BÝT OSAZENY ODVZDUŠŇOVACÍ VENTILY).
- VYPOUŠTĚNÍ BUDE MOŽNÉ NA VYPOUŠTĚCÍCH KOHOUTECH NA NEJNIŽŠÍCH MÍSTECH SOUSTAVY.
- KOTVENÍ POTRUBÍ BUDE ŘEŠENO DODAVATELSKOU DOKUMENTACÍ (STANDARD HILTI, SIKLA).
- V MÍSTNOSTECH VYBAVENÝCH PODLAHOVÝM VYTÁPĚNÍM BUDOU INSTALOVÁNY PROSTOROVÉ TERMOSTATY S ČIDLEM TEPLOTY PODLAHY V DODÁVCE EL. EL. BUDE OVLÁDAT TERMOPOHONY VENTILŮ NA ROZDĚLOVAČI PODLAHOVÉHO VYTÁPĚNÍ. TERMOPOHONY S PŘIPOJOVACÍM ZÁVITEM M30X1,5, PROSTOROVÉ TERMOSTATY S ČIDLEM TEPLOTY PODLAHY A KABELOVÉ PROPOJENÍ – DODÁVKA EL. EL. ZAJISTÍ ŘÍZENÍ TEPLOTY V JEDNOTLIVÝCH MÍSTNOSTECH.
- PŘI NÁVRHU PODLAHOVÉHO VYTÁPĚNÍ BYLO UVAŽOVÁNO S TĚMITO NÁŠLAPNÝMI VRSTVAMI:
  - KERAMICKÁ DLAŽBA R_{max}= 0,015 m²K/W
  - VINYLOVÁ PODLAHA R_{max}= 0,05 m²K/W
- VŠECHNY NÁŠLAPNÉ VRSTVY MUSÍ BÝT URČENY PRO PODLAHOVÉ VYTÁPĚNÍ !!!

Teplotní spád otopné vody okruhu přípravy TV 70/30 °C
Teplotní spád otopné vody okruhu vytápění objektu 43/33 °C

MINIMÁLNÍ TLOUŠŤKY TEPELNÉ IZOLACE

(λ = 0,038 W/m2K)

VOLNĚ VEDENÉ POTRUBÍ

DIMENZE	TLOUŠŤKA
DN12	20 mm
DN15, ø16,2x2,6	30 mm
DN20, ø20x2,9	30 mm
DN25, ø25x3,7	40 mm
DN32, ø32x4,7	40 mm
DN40, ø40x6	40 mm
DN50	50 mm
DN65	60 mm

V MÍSTECH KŘÍŽENÍ A PROSTUPŮ JE MOŽNÉ TEPELNOU IZOLACI OSLABIT

POTRUBÍ VEDENÉ VE ZDI A V PODLAZE

DIMENZE	TLOUŠŤKA
DN12	13 mm
DN15, ø16,2x2,6	13 mm
DN20, ø20x2,9	13 mm
DN25, ø25x3,7	13 mm
DN32, ø32x4,7	9 mm
DN40, ø40x6	20 mm
DN50	20 mm
DN65	20 mm

V MÍSTECH KŘÍŽENÍ A PROSTUPŮ JE MOŽNÉ TEPELNOU IZOLACI OSLABIT

Revize	Popis revize	Datum

severka

± 0,000 = 224,62 m.n.m (BPV)

stavba **BD Na Mariánské cestě - 2. etapa**		stupeň Dokumentace pro provádění stavby
zpracovatel TZB DESIGN TZB design s.r.o. projekční kancelář TZB Malý Okrouhlík 7/1039, 182 00 Praha 8 e-mail: mysicka@tzb-design.cz mobil: +420 732 933 758 www.tzb-design.cz	zodpovědný projektant Ing. Jan Myšička vypracoval Jan Svatoň	stavební objekt SO03 - Bytový dům D2 a C2 část D.1.2.4 - Vytápění, chlazení a vzduchotechnika profesní díl / členění části 01 - Vytápění
investor DOMOPLAN a.s. Trnitá 543/16, Brno, 602 00	generální projektant BK engineering project s.r.o. Hanusova 347/16 140 00 Praha 4 info@bkproject.cz hlavní inženýr projektu Ing. Libor Doležal	datum 09/2025 x A4 45 měřítko 1:50 číslo paré

	zakázka	stupeň	s.objekt	část	členění	č. výkresu	revize
PŮDORYS 2NP	365	50	SO03	D.1.2.4	2.1	003	