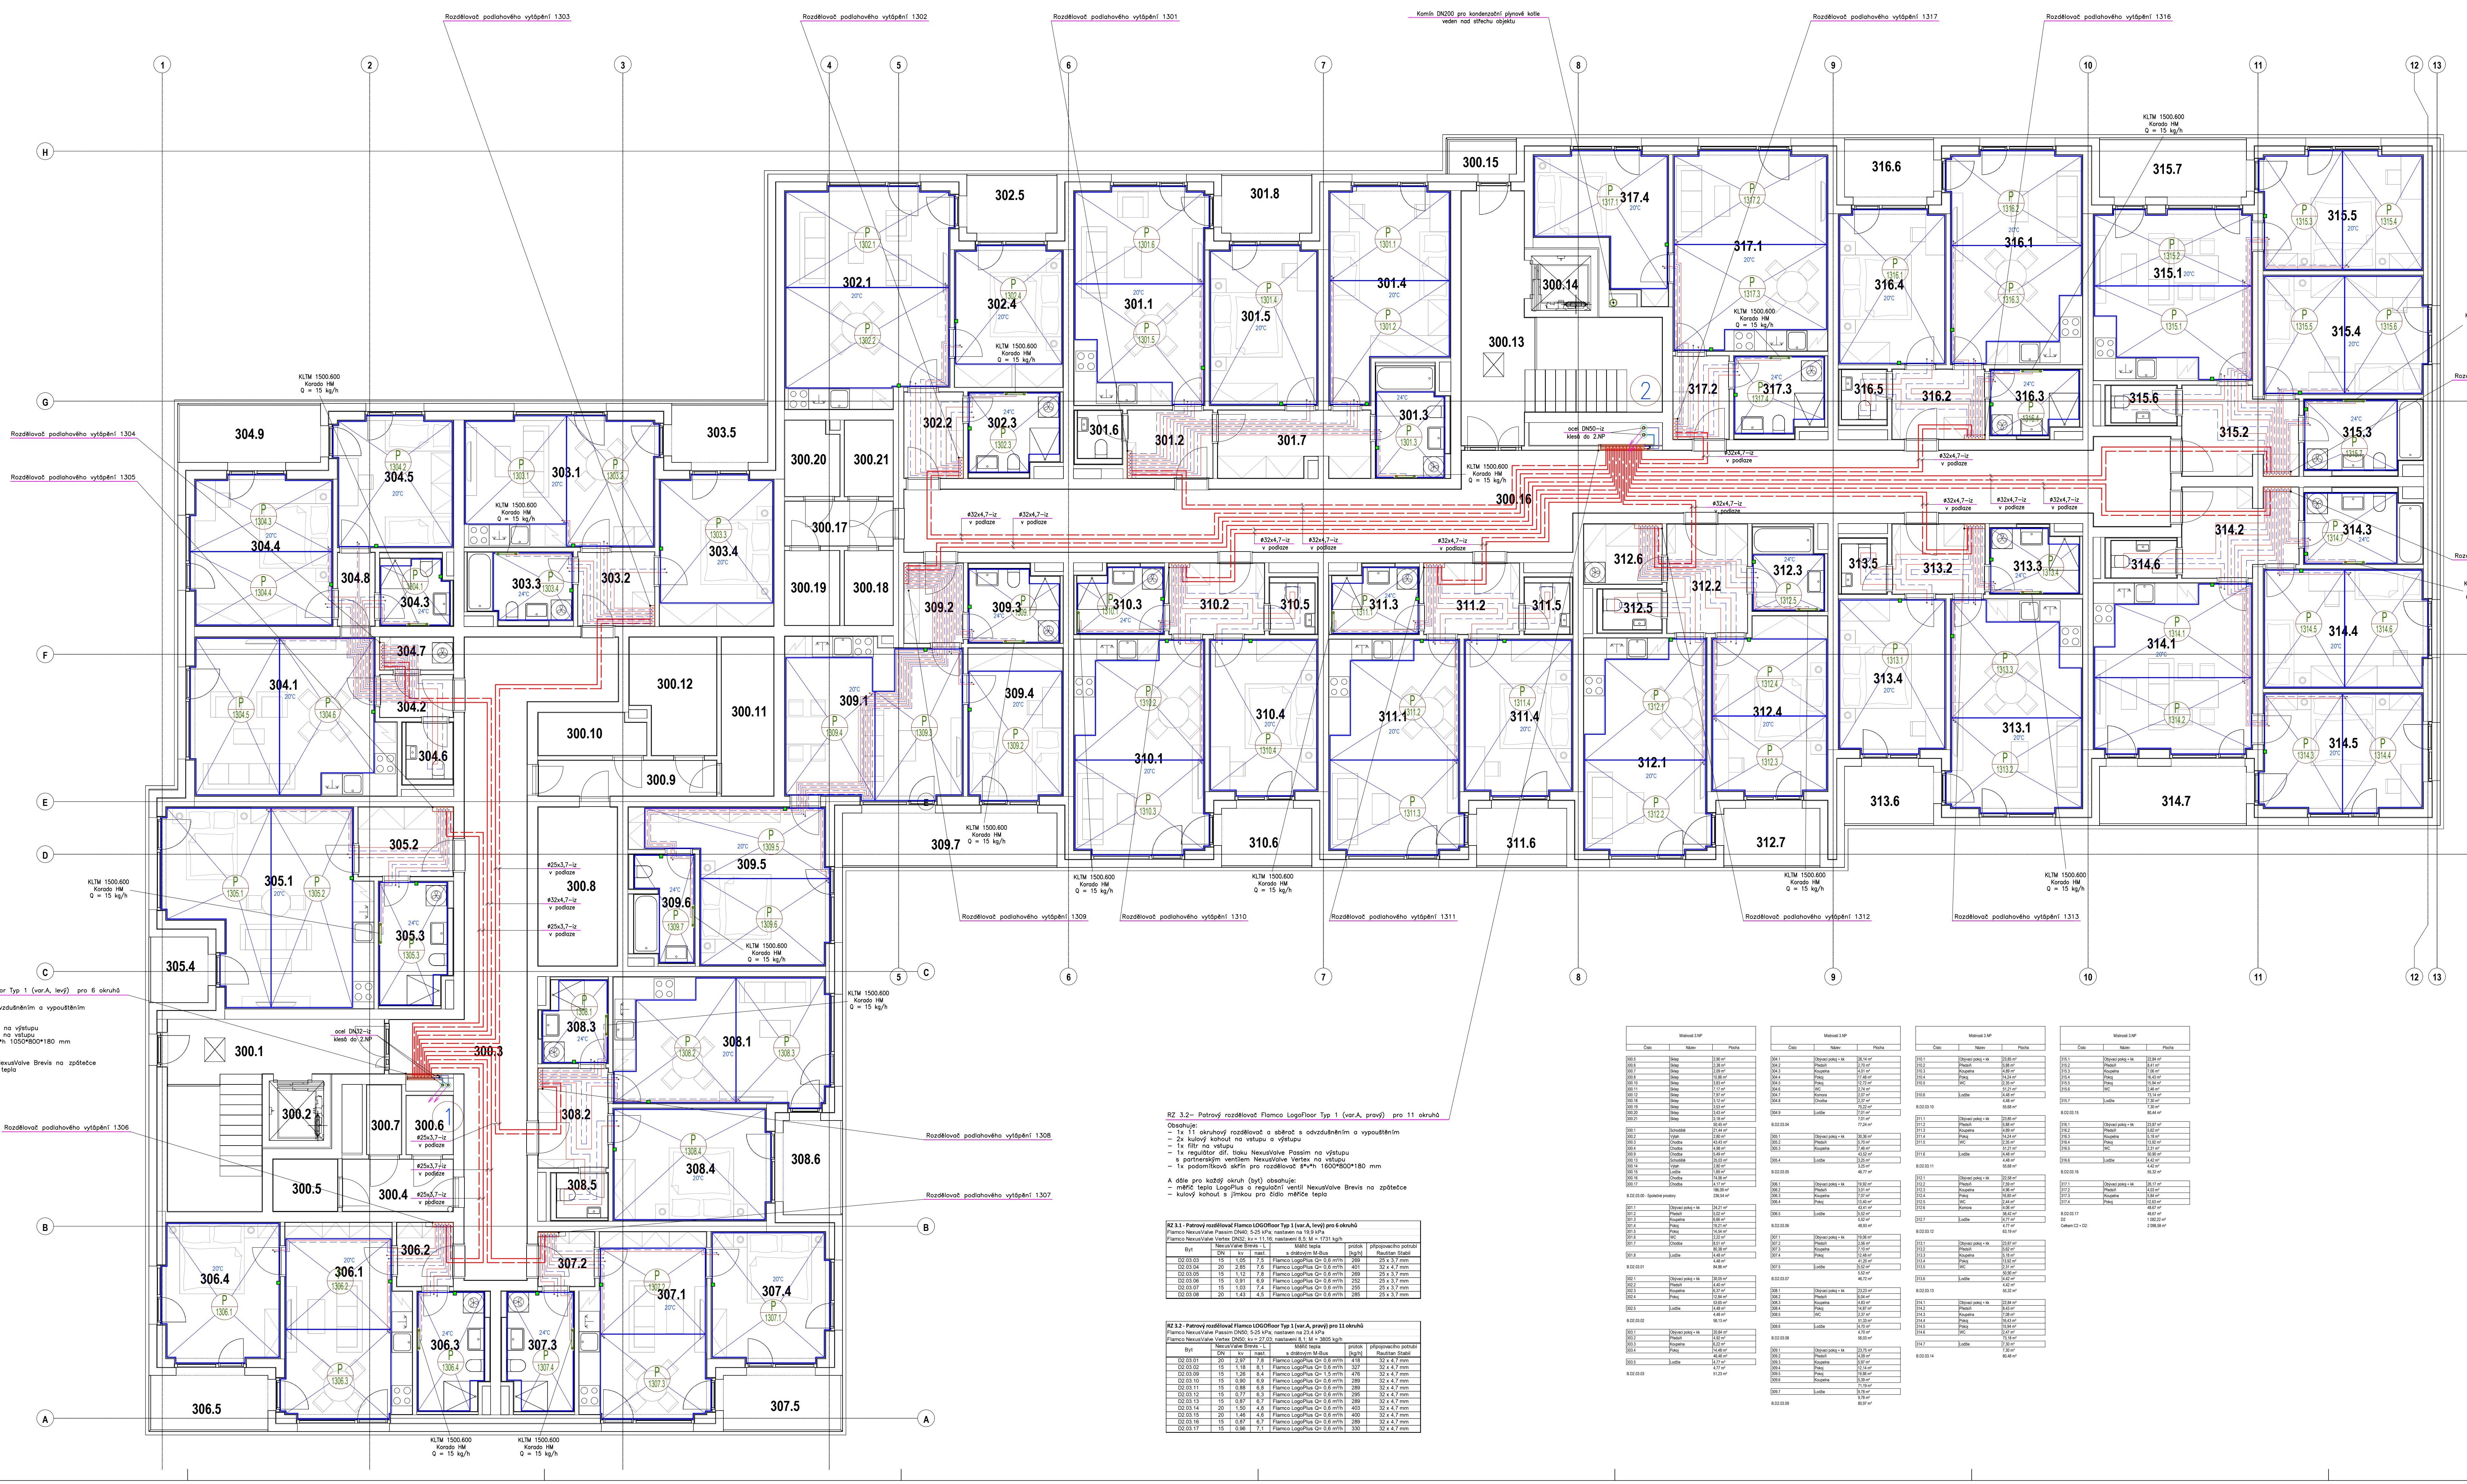
Rozdělovač podlahového vytápění 1303
Rozdělovač podlahového vytápění 1302
Rozdělovač podlahového vytápění 1301
Komín DN200 pro kondenzační plynové kotle veden nad střechu objektu
Rozdělovač podlahového vytápění 1317
Rozdělovač podlahového vytápění 1316
Rozdělovač podlahového vytápění 1304
Rozdělovač podlahového vytápění 1305
Rozdělovač podlahového vytápění 1315
Rozdělovač podlahového vytápění 1314
Rozdělovač podlahového vytápění 1306
Rozdělovač podlahového vytápění 1308
Rozdělovač podlahového vytápění 1307
Rozdělovač podlahového vytápění 1309
Rozdělovač podlahového vytápění 1310
Rozdělovač podlahového vytápění 1311
Rozdělovač podlahového vytápění 1312
Rozdělovač podlahového vytápění 1313
KLTM 1500.600 Korado HM Q = 15 kg/h
ocel DN50–iz klesá do 2.NP
ocel DN32–iz klesá do 2.NP
ø32x4,7–iz v podlaze
ø25x3,7–iz v podlaze
1
2
3
4
5
6
7
8
9
10
11
12
13
A
B
C
D
E
F
G
H
300.1
300.2
300.3
300.4
300.5
300.6
300.7
300.8
300.9
300.10
300.11
300.12
300.13
300.14
300.15
300.16
300.17
300.18
300.19
300.20
300.21
20°C
24°C

RZ 3.1– Patrový rozdělovač Flamco LogoFloor Typ 1 (var.A, levý) pro 6 okruhů

Obsahuje:
- 1x 6 okruhový rozdělovač a sběrač s odvzdušněním a vypouštěním
- 2x kulový kohout na vstupu a výstupu
- 1x filtr na vstupu
- 1x regulátor dif. tlaku NexusValve Passim na výstupu s partnerským ventilem NexusValve Vertex na vstupu
- 1x podomítková skříň pro rozdělovač š*v*h 1050*800*180 mm

A dále pro každý okruh (byt) obsahuje:
- měřič tepla LogoPlus a regulační ventil NexusValve Brevis na zpátečce
- kulový kohout s jímkou pro čidlo měřiče tepla

RZ 3.2– Patrový rozdělovač Flamco LogoFloor Typ 1 (var.A, pravý) pro 11 okruhů

Obsahuje:
- 1x 11 okruhový rozdělovač a sběrač s odvzdušněním a vypouštěním
- 2x kulový kohout na vstupu a výstupu
- 1x filtr na vstupu
- 1x regulátor dif. tlaku NexusValve Passim na výstupu s partnerským ventilem NexusValve Vertex na vstupu
- 1x podomítková skříň pro rozdělovač š*v*h 1600*800*180 mm

A dále pro každý okruh (byt) obsahuje:
- měřič tepla LogoPlus a regulační ventil NexusValve Brevis na zpátečce
- kulový kohout s jímkou pro čidlo měřiče tepla

RZ 3.1 - Patrový rozdělovač Flamco LOGOfloor Typ 1 (var.A, levý) pro 6 okruhů
Flamco NexusValve Passim DN40; 5-25 kPa; nastaven na 19,9 kPa
Flamco NexusValve Vertex DN32; kv = 11,16; nastavení 8,5; M = 1731 kg/h

Byt	NexusValve Brevis - L			Měřič tepla s drátovým M-Bus	průtok [kg/h]	připojovacího potrubí Rautitan Stabil
	DN	kv	nast.			
D2.03.03	15	1,05	7,5	Flamco LogoPlus Q= 0,6 m³/h	269	25 x 3,7 mm
D2.03.04	20	2,85	7,6	Flamco LogoPlus Q= 0,6 m³/h	401	32 x 4,7 mm
D2.03.05	15	1,12	7,8	Flamco LogoPlus Q= 0,6 m³/h	269	25 x 3,7 mm
D2.03.06	15	0,91	6,9	Flamco LogoPlus Q= 0,6 m³/h	252	25 x 3,7 mm
D2.03.07	15	1,03	7,4	Flamco LogoPlus Q= 0,6 m³/h	255	25 x 3,7 mm
D2.03.08	20	1,43	4,5	Flamco LogoPlus Q= 0,6 m³/h	285	25 x 3,7 mm

RZ 3.2 - Patrový rozdělovač Flamco LOGOfloor Typ 1 (var.A, pravý) pro 11 okruhů
Flamco NexusValve Passim DN50; 5-25 kPa; nastaven na 23,4 kPa
Flamco NexusValve Vertex DN50; kv = 27,03; nastavení 8,1; M = 3805 kg/h

Byt	NexusValve Brevis - L			Měřič tepla s drátovým M-Bus	průtok [kg/h]	připojovacího potrubí Rautitan Stabil
	DN	kv	nast.			
D2.03.01	20	2,97	7,8	Flamco LogoPlus Q= 0,6 m³/h	418	32 x 4,7 mm
D2.03.02	15	1,18	8,1	Flamco LogoPlus Q= 0,6 m³/h	327	32 x 4,7 mm
D2.03.09	15	1,26	8,4	Flamco LogoPlus Q= 1,5 m³/h	476	32 x 4,7 mm
D2.03.10	15	0,90	6,9	Flamco LogoPlus Q= 0,6 m³/h	289	32 x 4,7 mm
D2.03.11	15	0,88	6,8	Flamco LogoPlus Q= 0,6 m³/h	289	32 x 4,7 mm
D2.03.12	15	0,77	6,3	Flamco LogoPlus Q= 0,6 m³/h	295	32 x 4,7 mm
D2.03.13	15	0,87	6,7	Flamco LogoPlus Q= 0,6 m³/h	289	32 x 4,7 mm
D2.03.14	20	1,50	4,8	Flamco LogoPlus Q= 0,6 m³/h	403	32 x 4,7 mm
D2.03.15	20	1,46	4,6	Flamco LogoPlus Q= 0,6 m³/h	400	32 x 4,7 mm
D2.03.16	15	0,87	6,7	Flamco LogoPlus Q= 0,6 m³/h	289	32 x 4,7 mm
D2.03.17	15	0,96	7,1	Flamco LogoPlus Q= 0,6 m³/h	330	32 x 4,7 mm

Místnosti 3.NP		
Číslo	Název	Plocha
300.5	Sklep	2,90 m²
300.6	Sklep	2,38 m²
300.7	Sklep	2,09 m²
300.8	Sklep	10,86 m²
300.10	Sklep	3,83 m²
300.11	Sklep	7,17 m²
300.12	Sklep	7,97 m²
300.18	Sklep	3,12 m²
300.19	Sklep	3,53 m²
300.20	Sklep	3,43 m²
300.21	Sklep	3,18 m²
		50,45 m²
300.1	Schodiště	21,44 m²
300.2	Výtah	2,80 m²
300.3	Chodba	43,43 m²
300.4	Chodba	4,98 m²
300.9	Chodba	5,49 m²
300.13	Schodiště	25,03 m²
300.14	Výtah	2,80 m²
300.15	Lodžie	1,89 m²
300.16	Chodba	74,06 m²
300.17	Chodba	4,17 m²
		186,09 m²
B.D2.03.00 - Společné prostory		236,54 m²
301.1	Obývací pokoj + kk	24,21 m²
301.2	Předsíň	5,02 m²
301.3	Koupelna	6,66 m²
301.4	Pokoj	19,21 m²
301.5	Pokoj	14,54 m²
301.6	WC	2,22 m²
301.7	Chodba	8,51 m²
		80,38 m²
301.8	Lodžie	4,48 m²
		4,48 m²
B.D2.03.01		84,86 m²
302.1	Obývací pokoj + kk	30,05 m²
302.2	Předsíň	4,40 m²
302.3	Koupelna	6,37 m²
302.4	Pokoj	12,84 m²
		53,65 m²
302.5	Lodžie	4,48 m²
		4,48 m²
B.D2.03.02		58,13 m²
303.1	Obývací pokoj + kk	20,84 m²
303.2	Předsíň	4,92 m²
303.3	Koupelna	6,22 m²
303.4	Pokoj	14,48 m²
		46,46 m²
303.5	Lodžie	4,77 m²
		4,77 m²
B.D2.03.03		51,23 m²

Místnosti 3.NP		
Číslo	Název	Plocha
304.1	Obývací pokoj + kk	26,14 m²
304.2	Předsíň	2,70 m²
304.3	Koupelna	4,01 m²
304.4	Pokoj	17,48 m²
304.5	Pokoj	12,72 m²
304.6	WC	2,74 m²
304.7	Komora	2,07 m²
304.8	Chodba	2,37 m²
		70,22 m²
304.9	Lodžie	7,01 m²
		7,01 m²
B.D2.03.04		77,24 m²
305.1	Obývací pokoj + kk	30,36 m²
305.2	Předsíň	5,70 m²
305.3	Koupelna	7,46 m²
		43,52 m²
305.4	Lodžie	3,25 m²
		3,25 m²
B.D2.03.05		46,77 m²
306.1	Obývací pokoj + kk	19,92 m²
306.2	Předsíň	3,01 m²
306.3	Koupelna	7,07 m²
306.4	Pokoj	13,40 m²
		43,41 m²
306.5	Lodžie	5,52 m²
		5,52 m²
B.D2.03.06		48,93 m²
307.1	Obývací pokoj + kk	19,06 m²
307.2	Předsíň	2,56 m²
307.3	Koupelna	7,10 m²
307.4	Pokoj	12,48 m²
		41,20 m²
307.5	Lodžie	5,52 m²
		5,52 m²
B.D2.03.07		46,72 m²
308.1	Obývací pokoj + kk	23,23 m²
308.2	Předsíň	6,04 m²
308.3	Koupelna	4,83 m²
308.4	Pokoj	14,87 m²
308.5	WC	2,37 m²
		51,33 m²
308.6	Lodžie	4,70 m²
		4,70 m²
B.D2.03.08		56,03 m²
309.1	Obývací pokoj + kk	23,75 m²
309.2	Předsíň	4,09 m²
309.3	Koupelna	5,97 m²
309.4	Pokoj	12,14 m²
309.5	Pokoj	19,86 m²
309.6	Koupelna	5,39 m²
		71,19 m²
309.7	Lodžie	9,78 m²
		9,78 m²
B.D2.03.09		80,97 m²

Místnosti 3.NP		
Číslo	Název	Plocha
310.1	Obývací pokoj + kk	23,85 m²
310.2	Předsíň	5,88 m²
310.3	Koupelna	4,89 m²
310.4	Pokoj	14,24 m²
310.5	WC	2,35 m²
		51,21 m²
310.6	Lodžie	4,48 m²
		4,48 m²
B.D2.03.10		55,68 m²
311.1	Obývací pokoj + kk	23,85 m²
311.2	Předsíň	5,88 m²
311.3	Koupelna	4,89 m²
311.4	Pokoj	14,24 m²
311.5	WC	2,35 m²
		51,21 m²
311.6	Lodžie	4,48 m²
		4,48 m²
B.D2.03.11		55,68 m²
312.1	Obývací pokoj + kk	22,58 m²
312.2	Předsíň	7,59 m²
312.3	Koupelna	4,96 m²
312.4	Pokoj	16,80 m²
312.5	WC	2,44 m²
312.6	Komora	4,06 m²
		58,42 m²
312.7	Lodžie	4,77 m²
		4,77 m²
B.D2.03.12		63,19 m²
313.1	Obývací pokoj + kk	23,87 m²
313.2	Předsíň	5,62 m²
313.3	Koupelna	5,18 m²
313.4	Pokoj	13,92 m²
313.5	WC	2,31 m²
		50,90 m²
313.6	Lodžie	4,42 m²
		4,42 m²
B.D2.03.13		55,32 m²
314.1	Obývací pokoj + kk	22,84 m²
314.2	Předsíň	8,43 m²
314.3	Koupelna	7,08 m²
314.4	Pokoj	16,43 m²
314.5	Pokoj	15,94 m²
314.6	WC	2,47 m²
		73,18 m²
314.7	Lodžie	7,30 m²
		7,30 m²
B.D2.03.14		80,48 m²

Místnosti 3.NP		
Číslo	Název	Plocha
315.1	Obývací pokoj + kk	22,84 m²
315.2	Předsíň	8,41 m²
315.3	Koupelna	7,06 m²
315.4	Pokoj	16,43 m²
315.5	Pokoj	15,94 m²
315.6	WC	2,46 m²
		73,14 m²
315.7	Lodžie	7,30 m²
		7,30 m²
B.D2.03.15		80,44 m²
316.1	Obývací pokoj + kk	23,87 m²
316.2	Předsíň	5,62 m²
316.3	Koupelna	5,18 m²
316.4	Pokoj	13,92 m²
316.5	WC	2,31 m²
		50,90 m²
316.6	Lodžie	4,42 m²
		4,42 m²
B.D2.03.16		55,32 m²
317.1	Obývací pokoj + kk	26,17 m²
317.2	Předsíň	4,03 m²
317.3	Koupelna	5,84 m²
317.4	Pokoj	12,63 m²
		48,67 m²
B.D2.03.17		48,67 m²
D2		1 282,22 m²
Celkem C2 + D2:		2 098,58 m²

Rozdělovače podlahového vytápění REHAU v 3.NP:

Číslo rozdělovače	Přívodní teplota	Typ rozdělovače	Skříň rozdělovače	Tlaková ztráta [kPa]	Hmotnostní průtok [kg/h]
1301	43°C	HKV-D 7 nerez	AP 805	6,4	418
1302	43°C	HKV-D 5 nerez	AP 605	5,8	327
1303	43°C	HKV-D 5 nerez	AP 605	3,2	269
1304	43°C	HKV-D 7 nerez	AP 805	4,1	401
1305	43°C	HKV-D 4 nerez	AP 605	5,8	269
1306	43°C	HKV-D 5 nerez	AP 605	5,1	252
1307	43°C	HKV-D 5 nerez	AP 605	6,5	255
1308	43°C	HKV-D 5 nerez	AP 605	6,9	285
1309	43°C	HKV-D 9 nerez	AP 805	2,0	476
1310	43°C	HKV-D 5 nerez	AP 605	6,0	289
1311	43°C	HKV-D 5 nerez	AP 605	6,0	289
1312	43°C	HKV-D 6 nerez	AP 805	1,8	295
1313	43°C	HKV-D 5 nerez	AP 605	5,4	289
1314	43°C	HKV-D 8 nerez	AP 805	2,0	403
1315	43°C	HKV-D 8 nerez	AP 805	1,8	400
1316	43°C	HKV-D 5 nerez	AP 605	5,6	289
1317	43°C	HKV-D 5 nerez	AP 605	3,4	330

PODLAHOVÉ VYTÁPĚNÍ v 3.NP

Číslo rozdělovače	Okruh	Plocha celková [m2]	Rozteč [mm]	Délka celková [m]	Průtok [kg/h]
1301	P 1301.1	9,4	150	89	61
	P 1301.2	9,4	150	81	61
	P 1301.3	4,9	100	67	51
	P 1301.4	14,4	150	111	93
	P 1301.5	10,7	150	78	70
	P 1301.6	10,7	150	86	70
1302	P 1302.1	14,0	150	109	91
	P 1302.2	14,0	150	102	91
	P 1302.3	5,7	100	62	63
	P 1302.4	10,7	150	82	70
1303	P 1303.1	9,4	150	75	61
	P 1303.2	9,4	150	71	61
	P 1303.3	12,1	150	90	79
	P 1303.4	4,5	100	54	54
1304	P 1304.1	3,6	100	48	40
	P 1304.2	12,7	150	100	82
	P 1304.3	8,8	150	76	57
	P 1304.4	8,8	150	74	57
	P 1304.5	11,7	150	95	76
	P 1304.6	11,7	150	97	76
1305	P 1305.1	14,0	150	108	91
	P 1305.2	14,0	150	102	91
	P 1305.3	6,7	100	75	74
1306	P 1306.1	13,6	150	104	88
	P 1306.2	8,2	150	61	53
	P 1306.3	8,2	150	65	53
	P 1306.4	6,3	100	69	43
1307	P 1307.1	12,7	150	97	98
	P 1307.2	7,7	150	57	50
	P 1307.3	7,7	150	61	50
	P 1307.4	6,3	100	69	43
1308	P 1308.1	4,1	100	46	46
	P 1308.2	10,1	150	72	66
	P 1308.3	10,1	150	88	66
	P 1308.4	14,6	150	116	95
1309	P 1309.1	5,3	100	61	58
	P 1309.2	10,2	150	79	66
	P 1309.3	10,5	150	78	68
	P 1309.4	10,5	150	82	68
	P 1309.5	9,5	150	88	62
	P 1309.6	9,5	150	94	62
	P 1309.7	3,9	100	76	65
1310	P 1310.1	4,4	100	49	49
	P 1310.2	10,5	150	75	68
	P 1310.3	10,5	150	90	68
	P 1310.4	14,0	150	112	91
1311	P 1311.1	4,4	100	48	49
	P 1311.2	10,5	150	75	68
	P 1311.3	10,5	150	90	68
	P 1311.4	14,0	150	112	91
1312	P 1312.1	9,8	150	83	64
	P 1312.2	9,8	150	84	64
	P 1312.3	7,5	150	67	49
	P 1312.4	7,5	150	62	49
	P 1312.5	3,4	100	44	56
1313	P 1313.1	13,7	150	108	89
	P 1313.2	10,5	150	90	68
	P 1313.3	10,5	150	75	68
	P 1313.4	4,5	100	50	50
1314	P 1314.1	10,1	150	87	66
	P 1314.2	10,1	150	82	66
	P 1314.3	7,9	150	72	51
	P 1314.4	7,9	150	77	51
	P 1314.5	8,1	150	60	53
	P 1314.6	8,1	150	64	53
	P 1314.7	5,5	100	60	51
1315	P 1315.1	9,9	150	86	64
	P 1315.2	9,9	150	81	64
	P 1315.3	7,9	150	72	51
	P 1315.4	7,9	150	77	51
	P 1315.5	8,1	150	60	53
	P 1315.6	8,1	150	64	53
	P 1315.7	5,5	100	60	51
1316	P 1316.1	13,8	150	109	90
	P 1316.2	10,5	150	90	68
	P 1316.3	10,5	150	75	68
	P 1316.4	4,5	100	50	50
1317	P 1317.1	12,0	150	91	78
	P 1317.2	12,1	150	94	79
	P 1317.3	12,1	150	88	79
	P 1317.4	5,5	100	63	81

Rozdělovače podlahového vytápění REHAU v 3.NP:

Číslo rozdělovače	Přívodní teplota	Typ rozdělovače	Skříň rozdělovače	Tlaková ztráta [kPa]	Hmotnostní průtok [kg/h]
2301	43°C	HKV-D 5 nerez	AP 605	3,6	232
2302	43°C	HKV-D 5 nerez	AP 605	6,1	280
2303	43°C	HKV-D 4 nerez	AP 605	1,8	206
2304	43°C	HKV-D 5 nerez	AP 605	11,3	319
2305	43°C	HKV-D 5 nerez	AP 605	11,5	320
2306	43°C	HKV-D 4 nerez	AP 605	1,8	206
2307	43°C	HKV-D 5 nerez	AP 605	6,1	280
2308	43°C	HKV-D 5 nerez	AP 605	6,4	295
2309	43°C	HKV-D 5 nerez	AP 605	2,9	258
2310	43°C	HKV-D 4 nerez	AP 605	2,0	210
2311	43°C	HKV-D 7 nerez	AP 805	7,6	478
2312	43°C	HKV-D 8 nerez	AP 805	1,9	393
2313	43°C	HKV-D 5 nerez	AP 605	6,4	303

PODLAHOVÉ VYTÁPĚNÍ v 3.NP

Číslo rozdělovače	Okruh	Plocha celková [m2]	Rozteč [mm]	Délka celková [m]	Průtok [kg/h]
2301	P 2301.1	12,2	150	98	79
	P 2301.2	7,5	150	67	49
	P 2301.3	7,5	150	60	49
	P 2301.4	4,5	100	55	42
2302	P 2302.1	14,1	150	112	91
	P 2302.2	10,0	150	85	65
	P 2302.3	10,0	150	76	65
	P 2302.4	4,1	100	47	45
2303	P 2303.1	10,1	150	81	66
	P 2303.2	10,1	150	75	66
	P 2303.3	6,0	100	66	61
2304	P 2304.1	10,9	150	85	144
	P 2304.2	8,8	150	69	57
	P 2304.3	8,8	150	65	57
	P 2304.4	6,8	100	73	46
2305	P 2305.1	10,9	150	85	146
	P 2305.2	8,8	150	69	57
	P 2305.3	8,8	150	65	57
	P 2305.4	6,8	100	73	46
2306	P 2306.1	6,0	100	66	61
	P 2306.2	10,1	150	75	66
	P 2306.3	10,1	150	81	66
2307	P 2307.1	14,1	150	112	91
	P 2307.2	10,0	150	85	65
	P 2307.3	10,0	150	76	65
	P 2307.4	4,1	100	47	45
2308	P 2308.1	14,3	150	113	93
	P 2308.2	10,3	150	87	67
	P 2308.3	10,3	150	78	67
	P 2308.4	4,1	100	47	55
2309	P 2309.1	4,5	100	51	50
	P 2309.2	11,6	150	88	75
	P 2309.3	9,2	150	78	60
	P 2309.4	9,2	150	79	60
2310	P 2310.1	6,0	100	66	61
	P 2310.2	10,4	150	77	68
	P 2310.3	10,4	150	84	68
2311	P 2311.1	11,0	150	77	71
	P 2311.2	11,0	150	86	71
	P 2311.3	13,0	150	105	88
	P 2311.4	9,8	150	81	64
	P 2311.5	5,4	100	73	75
	P 2311.6	14,8	150	124	96
2312	P 2312.1	10,0	150	85	65
	P 2312.2	10,0	150	80	65
	P 2312.3	7,9	150	70	51
	P 2312.4	7,9	150	75	51
	P 2312.5	7,9	150	58	51
	P 2312.6	7,9	150	63	51
	P 2312.7	5,6	100	62	45
2313	P 2313.1	14,5	150	109	94
	P 2313.2	5,7	100	72	63
	P 2313.3	10,2	150	78	66
	P 2313.4	10,2	150	83	66

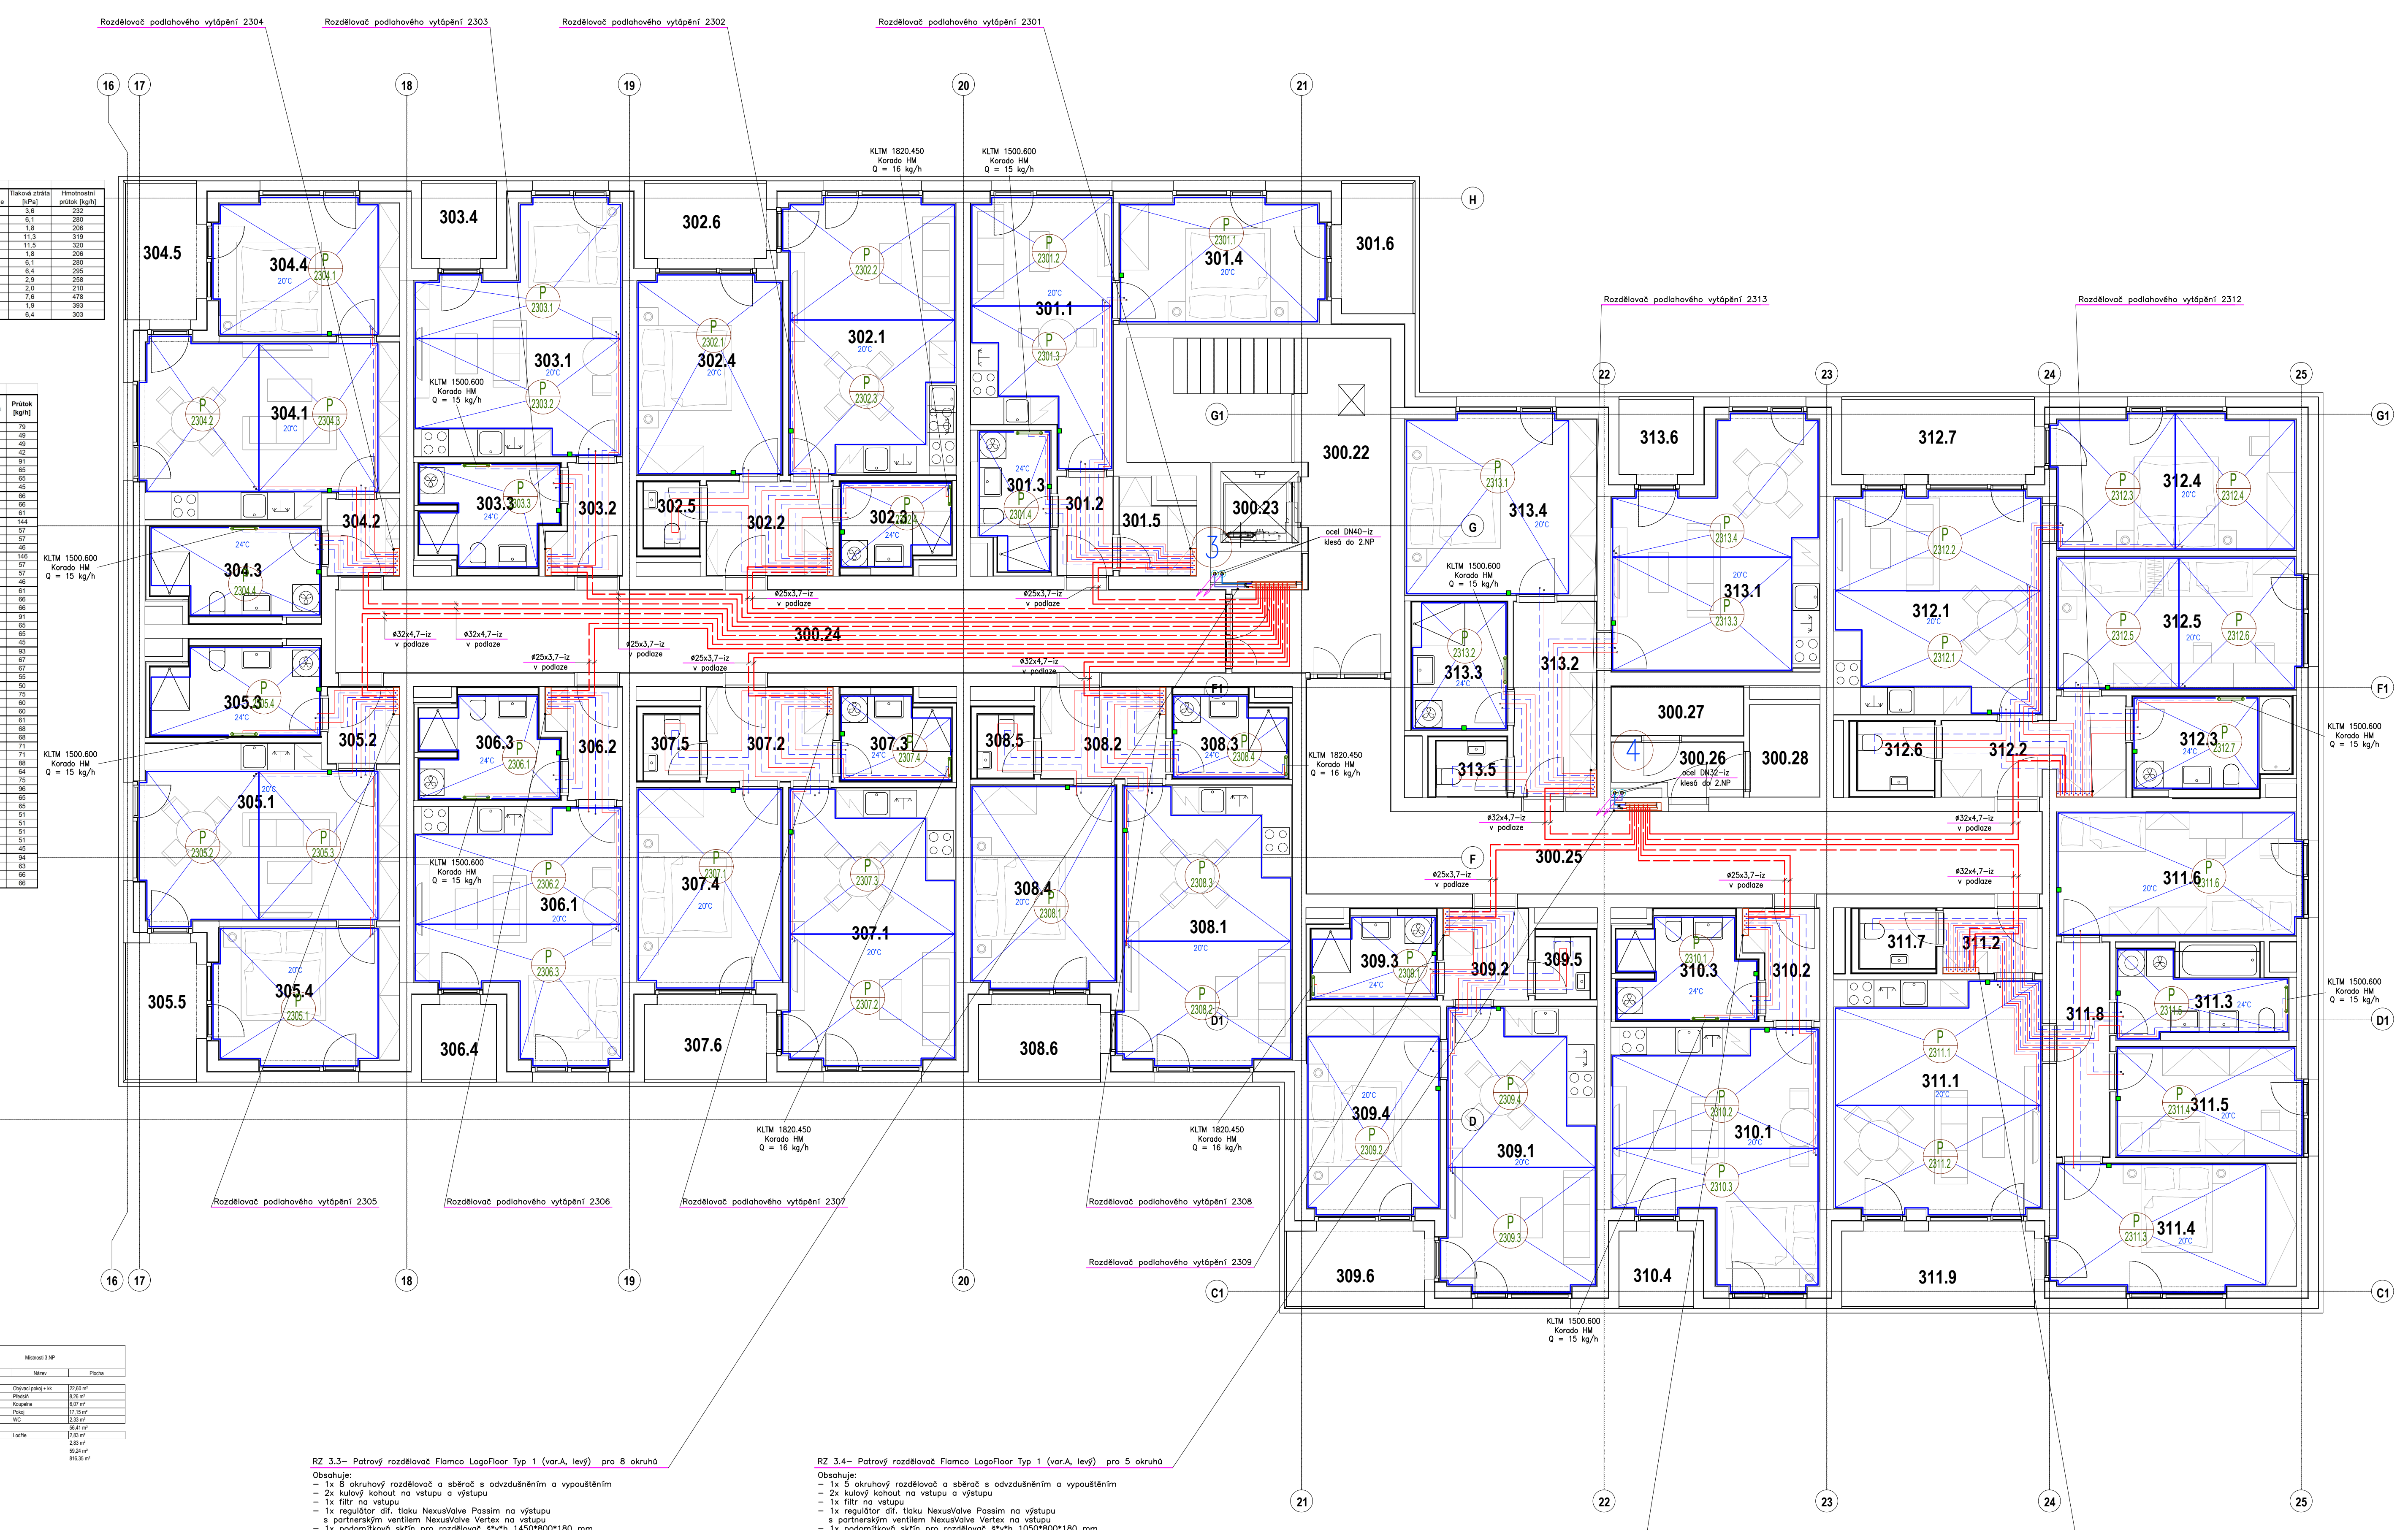
Rozdělovač podlahového vytápění 2304
Rozdělovač podlahového vytápění 2303
Rozdělovač podlahového vytápění 2302
Rozdělovač podlahového vytápění 2301
Rozdělovač podlahového vytápění 2313
Rozdělovač podlahového vytápění 2312
Rozdělovač podlahového vytápění 2305
Rozdělovač podlahového vytápění 2306
Rozdělovač podlahového vytápění 2307
Rozdělovač podlahového vytápění 2308
Rozdělovač podlahového vytápění 2309
Rozdělovač podlahového vytápění 2310
Rozdělovač podlahového vytápění 2311
KLTM 1500.600 Korado HM Q = 15 kg/h
KLTM 1820.450 Korado HM Q = 16 kg/h
ocel DN40–iz klesá do 2.NP
ocel DN32–iz klesá do 2.NP
ø32x4,7–iz v podlaze
ø25x3,7–iz v podlaze
14
15
16
17
18
19
20
21
22
23
24
25
H
G
G1
F
F1
D
D1
C1
300.22
300.23
300.24
300.25
300.26
300.27
300.28
20°C
24°C

Místnosti 3.NP		
Číslo	Název	Plocha
300.27	Sklep	3,35 m²
300.28	Sklep	3,28 m²
		6,63 m²
300.22	Schodiště	28,56 m²
300.23	Výtah	2,80 m²
300.24	Chodba	37,57 m²
300.25	Chodba	36,64 m²
300.26	Chodba	3,27 m²
		108,84 m²
B.C2.03.00 - Společné prostory		115,46 m²
301.1	Obývací pokoj + kk	17,27 m²
301.2	Předsíň	2,78 m²
301.3	Koupelna	5,15 m²
301.4	Pokoj	12,31 m²
301.5	Komora	3,21 m²
		40,73 m²
301.6	Lodžie	4,70 m²
		4,70 m²
B.C2.03.01		45,42 m²
302.1	Obývací pokoj + kk	23,06 m²
302.2	Předsíň	6,05 m²
302.3	Koupelna	4,74 m²
302.4	Pokoj	14,35 m²
302.5	WC	2,37 m²
		50,57 m²
302.6	Lodžie	4,62 m²
		4,62 m²
B.C2.03.02		55,19 m²
303.1	Obývací pokoj + kk	22,43 m²
303.2	Předsíň	3,59 m²
303.3	Koupelna	6,92 m²
		32,94 m²
303.4	Lodžie	2,83 m²
		2,83 m²
B.C2.03.03		35,77 m²
304.1	Obývací pokoj + kk	21,58 m²
304.2	Předsíň	2,77 m²
304.3	Koupelna	7,75 m²
304.4	Pokoj	12,03 m²
		44,14 m²
304.5	Lodžie	4,91 m²
		4,91 m²
B.C2.03.04		49,05 m²
305.1	Obývací pokoj + kk	21,61 m²
305.2	Předsíň	2,76 m²
305.3	Koupelna	7,73 m²
305.4	Pokoj	12,03 m²
		44,14 m²
305.5	Lodžie	4,92 m²
		4,92 m²
B.C2.03.05		49,06 m²
306.1	Obývací pokoj + kk	22,43 m²
306.2	Předsíň	3,59 m²
306.3	Koupelna	6,93 m²
		32,95 m²
306.4	Lodžie	2,83 m²
		2,83 m²
B.C2.03.06		35,78 m²

Místnosti 3.NP		
Číslo	Název	Plocha
307.1	Obývací pokoj + kk	23,07 m²
307.2	Předsíň	6,06 m²
307.3	Koupelna	4,75 m²
307.4	Pokoj	14,36 m²
307.5	WC	2,37 m²
		50,60 m²
307.6	Lodžie	4,62 m²
		4,62 m²
B.C2.03.07		55,23 m²
308.1	Obývací pokoj + kk	23,52 m²
308.2	Předsíň	5,81 m²
308.3	Koupelna	4,76 m²
308.4	Pokoj	14,57 m²
308.5	WC	2,28 m²
		50,93 m²
308.6	Lodžie	4,62 m²
		4,62 m²
B.C2.03.08		55,56 m²
309.1	Obývací pokoj + kk	21,28 m²
309.2	Předsíň	3,97 m²
309.3	Koupelna	5,21 m²
309.4	Pokoj	13,72 m²
309.5	WC	2,20 m²
		46,38 m²
309.6	Lodžie	5,32 m²
		5,32 m²
B.C2.03.09		51,69 m²
310.1	Obývací pokoj + kk	23,26 m²
310.2	Předsíň	3,65 m²
310.3	Koupelna	6,94 m²
		33,86 m²
310.4	Lodžie	2,81 m²
		2,81 m²
B.C2.03.10		36,66 m²
311.1	Obývací pokoj + kk	24,21 m²
311.2	Předsíň	3,30 m²
311.3	Koupelna	7,73 m²
311.4	Pokoj	14,96 m²
311.5	Pokoj	10,04 m²
311.6	Pokoj	15,12 m²
311.7	WC	2,74 m²
311.8	Chodba	5,78 m²
		83,88 m²
311.9	Lodžie	7,30 m²
		7,30 m²
B.C2.03.11		91,18 m²
312.1	Obývací pokoj + kk	23,03 m²
312.2	Předsíň	7,83 m²
312.3	Koupelna	7,57 m²
312.4	Pokoj	15,96 m²
312.5	Pokoj	16,12 m²
312.6	WC	3,25 m²
		73,75 m²
312.7	Lodžie	7,30 m²
		7,30 m²
B.C2.03.12		81,05 m²

Místnosti 3.NP		
Číslo	Název	Plocha
313.1	Obývací pokoj + kk	22,60 m²
313.2	Předsíň	8,26 m²
313.3	Koupelna	6,07 m²
313.4	Pokoj	17,15 m²
313.5	WC	2,33 m²
		56,41 m²
313.6	Lodžie	2,83 m²
		2,83 m²
B.C2.03.13		59,24 m²
C2		816,35 m²

RZ 3.3– Patrový rozdělovač Flamco LogoFloor Typ 1 (var.A, levý) pro 8 okruhů

Obsahuje:
- 1x 8 okruhový rozdělovač a sběrač s odvzdušněním a vypouštěním
- 2x kulový kohout na vstupu a výstupu
- 1x filtr na vstupu
- 1x regulátor dif. tlaku NexusValve Passim na výstupu s partnerským ventilem NexusValve Vertex na vstupu
- 1x podomítková skříň pro rozdělovač š*v*h 1450*800*180 mm

A dále pro každý okruh (byt) obsahuje:
- měřič tepla LogoPlus a regulační ventil NexusValve Brevis na zpátečce
- kulový kohout s jímkou pro čidlo měřiče tepla

RZ 3.3 - Patrový rozdělovač Flamco LOGOfloor Typ 1 (var.A, levý) pro 8 okruhů
Flamco NexusValve Passim DN40; 5-25 kPa; nastaven na 22,8 kPa
Flamco NexusValve Vertex DN40; kv = 15,19; nastavení 7,2; M = 2138 kg/h

Byt	NexusValve Brevis - L			Měřič tepla s drátovým M-Bus	průtok [kg/h]	připojovacího potrubí Rautitan Stabil
	DN	kv	nast.			
C2.03.01	15	0,63	5,6	Flamco LogoPlus Q= 0,6 m³/h	232	25 x 3,7 mm
C2.03.02	15	1,05	7,5	Flamco LogoPlus Q= 0,6 m³/h	280	25 x 3,7 mm
C2.03.03	15	0,53	5,1	Flamco LogoPlus Q= 0,6 m³/h	206	25 x 3,7 mm
C2.03.04	20	2,09	6,1	Flamco LogoPlus Q= 0,6 m³/h	319	32 x 4,7 mm
C2.03.05	20	2,27	6,5	Flamco LogoPlus Q= 0,6 m³/h	320	32 x 4,7 mm
C2.03.06	15	0,53	5,1	Flamco LogoPlus Q= 0,6 m³/h	206	25 x 3,7 mm
C2.03.07	15	1,06	7,6	Flamco LogoPlus Q= 0,6 m³/h	280	25 x 3,7 mm
C2.03.08	15	0,96	7,1	Flamco LogoPlus Q= 0,6 m³/h	295	32 x 4,7 mm

RZ 3.4– Patrový rozdělovač Flamco LogoFloor Typ 1 (var.A, levý) pro 5 okruhů

Obsahuje:
- 1x 5 okruhový rozdělovač a sběrač s odvzdušněním a vypouštěním
- 2x kulový kohout na vstupu a výstupu
- 1x filtr na vstupu
- 1x regulátor dif. tlaku NexusValve Passim na výstupu s partnerským ventilem NexusValve Vertex na vstupu
- 1x podomítková skříň pro rozdělovač š*v*h 1050*800*180 mm

A dále pro každý okruh (byt) obsahuje:
- měřič tepla LogoPlus a regulační ventil NexusValve Brevis na zpátečce
- kulový kohout s jímkou pro čidlo měřiče tepla

RZ 3.4 - Patrový rozdělovač Flamco LOGOfloor Typ 1 (var.A, levý) pro 5 okruhů
Flamco NexusValve Passim DN40; 5-25 kPa; nastaven na 16,7 kPa
Flamco NexusValve Vertex DN32; kv = 10,60; nastavení 8,1; M = 1642 kg/h

Byt	NexusValve Brevis - L			Měřič tepla s drátovým M-Bus	průtok [kg/h]	připojovacího potrubí Rautitan Stabil
	DN	kv	nast.			
C2.03.09	15	0,97	7,2	Flamco LogoPlus Q= 0,6 m³/h	258	25 x 3,7 mm
C2.03.10	15	0,66	5,7	Flamco LogoPlus Q= 0,6 m³/h	210	25 x 3,7 mm
C2.03.11	20	2,41	6,8	Flamco LogoPlus Q= 1,5 m³/h	478	32 x 4,7 mm
C2.03.12	20	2,79	7,5	Flamco LogoPlus Q= 0,6 m³/h	393	32 x 4,7 mm
C2.03.13	20	1,66	5,2	Flamco LogoPlus Q= 0,6 m³/h	303	32 x 4,7 mm

Legenda ÚT

— — —	Hlavní rozvod otopné vody okruhu vytápění objektu. Rozvod z ocelového potrubí spojovaného svařováním s tepelnou izolací veden v šachtě není-li na výkrese vyznačeno jinak. Dimenze dopojení jednotlivých patrových rozdělovačů viz Schéma hlavních rozvodů.
— — —	Rozvod otopné vody pro napojení jednotlivých bytů. Rozvod z plastového potrubí s kyslíkovou bariérou Rehau Rautitan stabil s tepelnou izolací veden v podlaze není-li na výkrese vyznačeno jinak. Nekótované úseky jsou ø32x4,7 mm.
▬	Koupelnové otopné těleso Korado Koralux Linear Comfort-M. Na rozvod otopné vody napojeno ze zdi pomocí rohové připojovací sady Korado HM s termostatickou hlavicí. S PŘÍPRAVOU pro napojení el. topné patrony s regulátorem teploty Korado Z-KT7R-400. Značeno: typ výška.šířka
- - -	Rozvod jednotlivých okruhů podlahového vytápění. Rozvod z plastového potrubí Rehau Rautherm S 17x2 veden v podlaze.
P X.Y	Okruh podlahového vytápění číslo Y napojen na rozdělovač číslo X.
—	Hranice prostoru vytápěného podlahovým vytápěním, hranice jednotlivých okruhů podlahového vytápění.
▭	Rozdělovač podlahového vytápění Rehau HKV-D. Umístěn ve skříni rozdělovače Rehau.
■	Prostorový termostat podlahového vytápění s externím čidlem teploty podlahy – dodávka EL.

Poznámky:

- REALIZACE SYSTÉMU VYTÁPĚNÍ MUSÍ PROBÍHAT KOORDINOVANĚ S OSTATNÍMI PROFESEMI A POŽADAVKY STAVEBNĚ – ARCHITEKTONICKÉHO ŘEŠENÍ, A TO ZEJMÉNA S NOMINOVANÝMI PŘÍPRAVAMI PRO INTERIÉR A JEHO KONCOVÝMI PRVKY.
- PATROVÉ ROZVODY PRO VYTÁPĚNÍ BYTŮ A NEBYTOVÝCH PROSTOR BUDOU PROVEDENY Z PLASTOVÉHO POTRUBÍ S KYSLÍKOVOU BARIÉROU REHAU RAUTITAN STABIL. POTRUBÍ BUDE SPOJOVÁNO NEROZEBÍRATELNÝMI SPOJI PRO ULOŽENÍ V PODLAZE.
- HLAVNÍ ROZVODY VEDENÉ POD STROPEM V 1.PP, STOUPAČKY A DOPOJENÍ PATROVÝCH ROZDĚLOVAČŮ BUDOU VYTVOŘENY Z OCELOVÉHO POTRUBÍ (DO DN50 TRUBKY ZÁVITOVÉ BĚŽNÉ PODLE ČSN 42 5710, OD DN60 TRUBKY HLADKÉ PODLE ČSN 42 5715). POTRUBÍ DN65 JE 76x3,2 MM.
- PATROVÉ ROZDĚLOVAČE BUDOU DOPOJENY PANCÉŘOVANÝMI HADICEMI NEBO JINÝM PRVKEM, KTERÝ UMOŽNÍ KOMPENZACI DÉLKOVÉ ROZTAŽNOSTI STOUPAČKY.
- POTRUBÍ ÚT BUDE OPATŘENO PŘÍSLUŠNOU TLOUŠŤKOU TEPELNÉ IZOLACE. NA ROZVODY V PODLAZE BUDE POUŽITA POLYETYLENOVÁ IZOLACE. PRO VOLNÉ ROZVODY PAK MINERÁLNÍ IZOLACE S HLINÍKOVÝM POVRCHEM.
- ODVZDUŠNĚNÍ BUDE MOŽNÉ NA OTOPNÝCH TĚLESECH A NA NEJVYŠŠÍCH MÍSTECH SOUSTAVY (KDE MUSÍ BÝT OSAZENY ODVZDUŠŇOVACÍ VENTILY).
- VYPOUŠTĚNÍ BUDE MOŽNÉ NA VYPOUŠTĚCÍCH KOHOUTECH NA NEJNIŽŠÍCH MÍSTECH SOUSTAVY.
- KOTVENÍ POTRUBÍ BUDE ŘEŠENO DODAVATELSKOU DOKUMENTACÍ (STANDARD HILTI, SIKLA).
- V MÍSTNOSTECH VYBAVENÝCH PODLAHOVÝM VYTÁPĚNÍM BUDOU INSTALOVÁNY PROSTOROVÉ TERMOSTATY S ČIDLEM TEPLOTY PODLAHY V DODÁVCE EL. BUDE OVLÁDAT TERMOPOHONY VENTILŮ NA ROZDĚLOVAČI PODLAHOVÉHO VYTÁPĚNÍ. TERMOPOHONY S PŘIPOJOVACÍM ZÁVITEM M30X1,5, PROSTOROVÉ TERMOSTATY S ČIDLEM TEPLOTY PODLAHY A KABELOVÉ PROPOJENÍ – DODÁVKA EL. EL. ZAJISTÍ ŘÍZENÍ TEPLOTY V JEDNOTLIVÝCH MÍSTNOSTECH.
- PŘI NÁVRHU PODLAHOVÉHO VYTÁPĚNÍ BYLO UVAŽOVÁNO S TĚMITO NÁŠLAPNÝMI VRSTVAMI:
  - KERAMICKÁ DLAŽBA $R_{max} = 0,015$ m²K/W
  - VINYLOVÁ PODLAHA $R_{max} = 0,05$ m²K/W
- VŠECHNY NÁŠLAPNÉ VRSTVY MUSÍ BÝT URČENY PRO PODLAHOVÉ VYTÁPĚNÍ !!!

Teplotní spád otopné vody okruhu přípravy TV 70/30 °C
Teplotní spád otopné vody okruhu vytápění objektu 43/33 °C

MINIMÁLNÍ TLOUŠŤKY TEPELNÉ IZOLACE

(λ = 0,038 W/m2K)

VOLNĚ VEDENÉ POTRUBÍ

DIMENZE	TLOUŠŤKA
DN12	20 mm
DN15, ø16,2x2,6	30 mm
DN20, ø20x2,9	30 mm
DN25, ø25x3,7	40 mm
DN32, ø32x4,7	40 mm
DN40, ø40x6	40 mm
DN50	50 mm
DN65	60 mm

V MÍSTECH KŘÍŽENÍ A PROSTUPŮ JE MOŽNÉ TEPELNOU IZOLACI OSLABIT

POTRUBÍ VEDENÉ VE ZDI A V PODLAZE

DIMENZE	TLOUŠŤKA
DN12	13 mm
DN15, ø16,2x2,6	13 mm
DN20, ø20x2,9	13 mm
DN25, ø25x3,7	13 mm
DN32, ø32x4,7	9 mm
DN40, ø40x6	20 mm
DN50	20 mm
DN65	20 mm

V MÍSTECH KŘÍŽENÍ A PROSTUPŮ JE MOŽNÉ TEPELNOU IZOLACI OSLABIT

Revize	Popis revize	Datum

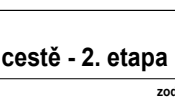
severka

± 0,000 = 224,62 m.n.m (BPV)

stavba **BD Na Mariánské cestě - 2. etapa**		stupeň Dokumentace pro provádění stavby
zpracovatel TZB DESIGN TZB design s.r.o. projekční kancelář TZB Malý Okrouhlík 7/1039, 182 00 Praha 8 e-mail: mysicka@tzb-design.cz mobil: +420 732 933 758 www.tzb-design.cz	zodpovědný projektant Ing. Jan Myšička vypracoval Jan Svatoň	stavební objekt SO03 - Bytový dům D2 a C2 část D.1.2.4 - Vytápění, chlazení a vzduchotechnika profesní díl / členění části 01 - Vytápění
investor DOMOPLAN a.s. Trnitá 543/16, Brno, 602 00	generální projektant BK engineering project s.r.o. Hanusova 347/16 140 00 Praha 4 info@bkproject.cz hlavní inženýr projektu Ing. Libor Doležal	datum 09/2025 x A4 45 měřítko 1:50 číslo paré

	zakázka	stupeň	s.objekt	část	členění	č. výkresu	revize
PŮDORYS 3NP	365	50	SO03	D.1.2.4	2.1	004	