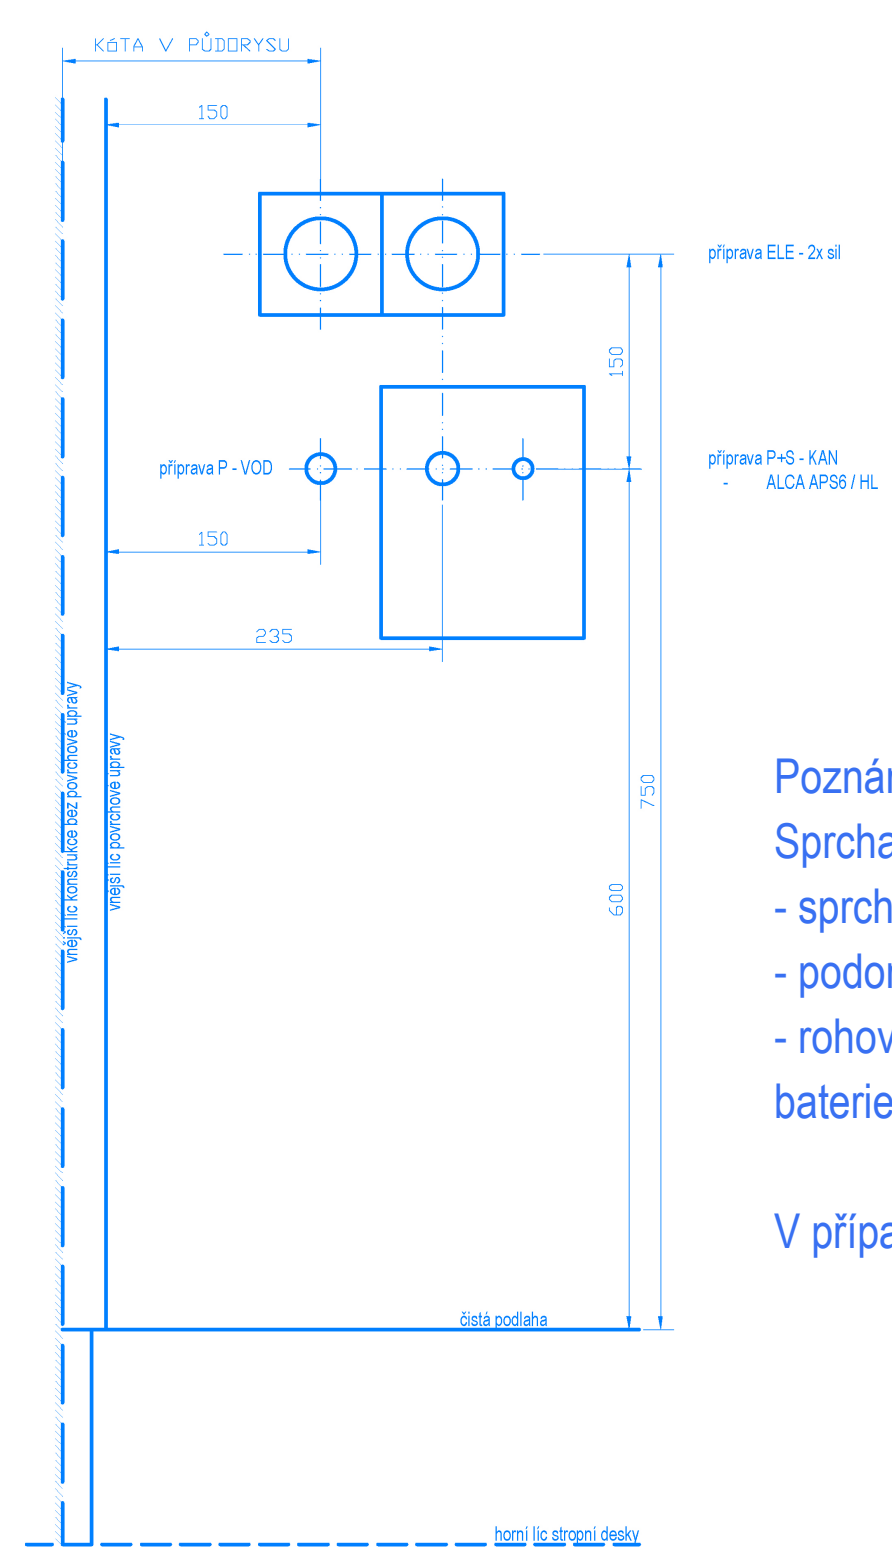
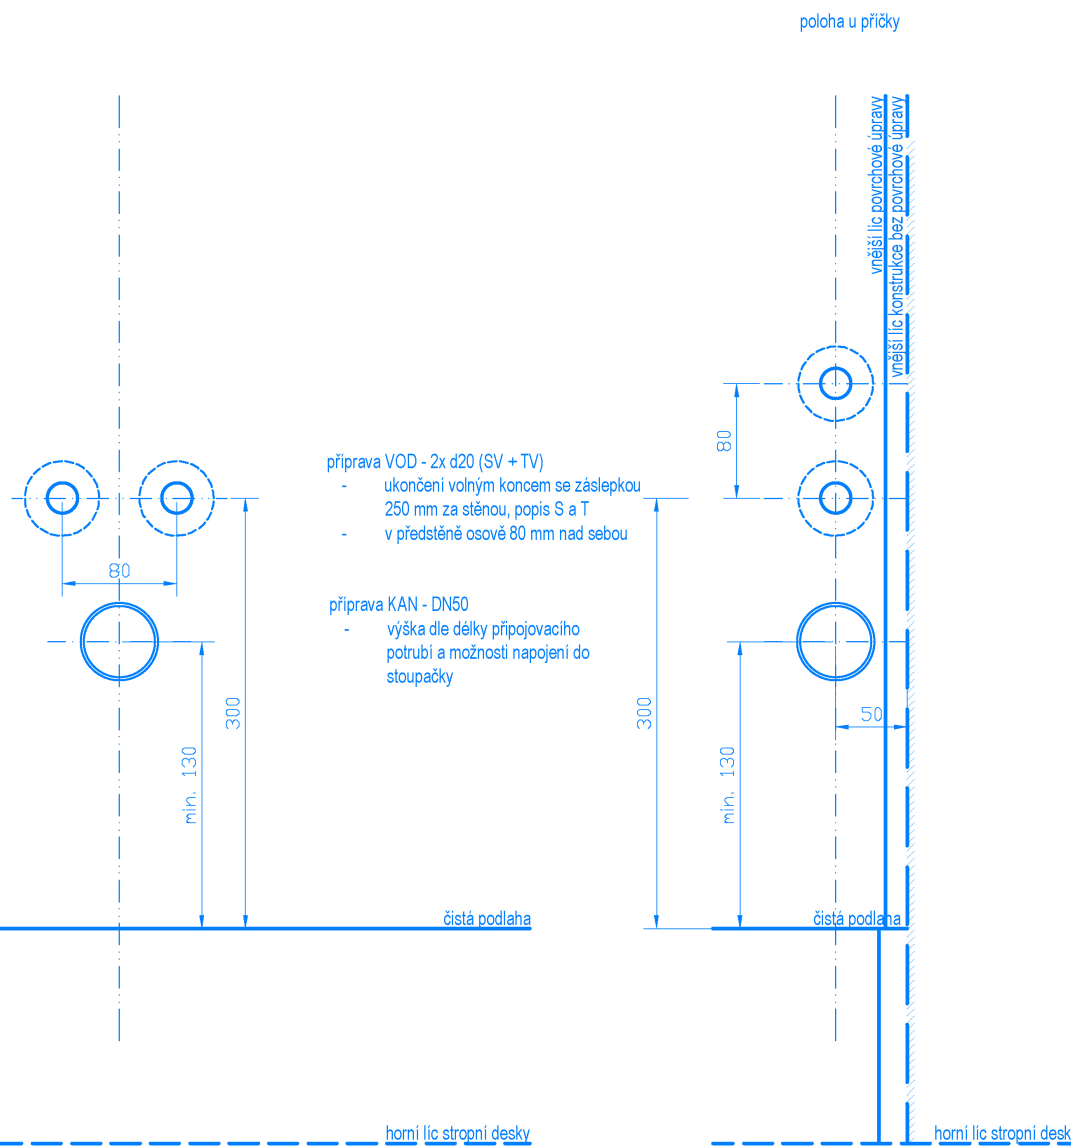


-  KK - KULOVÝ KOHOÚT
- W - VÝMĚŇOVACÍ VENTIL - TAŠAD
-  KKV - KULOVÝ KOHOÚT S VÝPOUŠTĚM
- RV - ROHOVÝ VENTIL
-  + PRACOVNÍ VENTIL/ZAHRADNÍ VENTIL S NÁPOJENÍM NA HADICI

 VK - VÝPOUSTĚČÍ KONEKT
 PV - POUŠTĚNÝ VENTIL
 ČERPAČKA
 ZK - ZPĚTNÁ KLAPEK
 VODOMĚR
 EMV - ELEKTROMAGNETICKÝ VENTIL
 PEVNÝ BOD

[illegible]

- sprcha ve výšce 2100 mm zarovnaná na výšku svítidla u umyvadla,
- podomítková baterie ve výšce 1000 mm
- rohový ventil pro napojení sprchy 170 mm od směšovací podomítkové baterie směrem ke stěně

V případě rozporu v půdoryse platí schéma

[illegible]