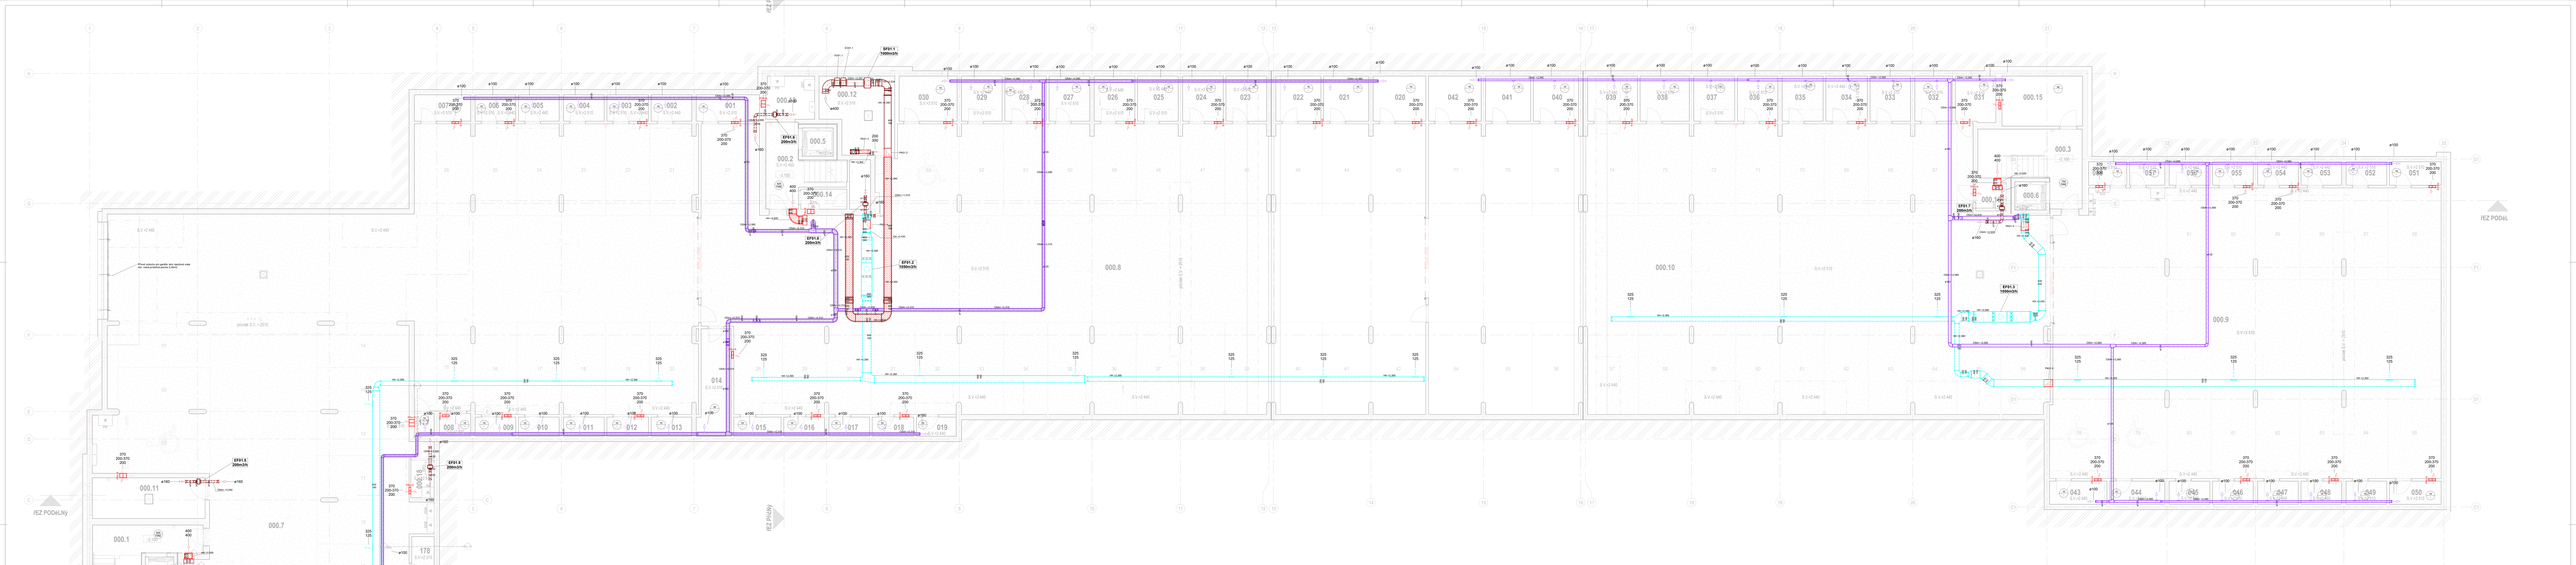

ŘEZ PODéLNÝ
ŘEZ PODéL
ŘEZ PŘÍČNÝ
SF01.1
1000m3/h
EF01.1
1050m3/h
EF01.2
1050m3/h
EF01.3
1050m3/h
EF01.4
200m3/h
EF01.5
200m3/h
EF01.6
200m3/h
EF01.7
200m3/h
EF01.8
200m3/h
EF01.9
200m3/h
EO01.1
VO01.1
PK01.1
PK01.2
PK01.3
PK01.4
PK01.5
PK01.6
000.1
000.2
000.3
000.4
000.5
000.6
000.7
000.8
000.9
000.10
000.11
000.12
000.13
000.14
000.15
000.18
001
002
003
004
005
006
007
008
009
010
011
012
013
014
015
016
017
018
019
020
021
022
023
024
025
026
027
028
029
030
031
032
033
034
035
036
037
038
039
040
041
042
043
044
045
046
047
048
049
050
051
052
053
054
055
056
057
058
178
179
180
181
S.V.=2 510
S.V.=2 440
S.V.=2 450
průvlak S.V. = 2510
Přívod vzduchu pro garáže skrz vjezdová vrata
min. volná průtočná plocha 0,45m2
370
200-370
200
325
125
400
400
200
300
ø100
ø125
ø160
ø200
ø400
PSU-S
OSA= +2,585
OSA= +2,310
OSA= +2,500
OSA= +2,357
OSA= +2,580
OSA= +1,010
HH +2,390
HH +2,580
HH +2,430
HH +2,600
HH +2,362
HH +2,534
HH +2,355
HH +3,550
-3,100
625
FIRE
750
FIRE
EPS
DAT
PR
ELE
AEM
H
G
G1
F
F1
E
D
D1
C
C1
B
A
1
2
3
4
5
6
7
8
9
10
11
12
13
14
15
16
17
18
19
20
21
22
23
24
25

LEGENDA

- PŘÍVODNÍ POTRUBÍ
- ODVODNÍ POTRUBÍ
- PROTIDEŠŤOVÁ ŽALUZIE - SÁNÍ
- PROTIDEŠŤOVÁ ŽALUZIE - VÝFUK
- VÝUSTKA - ODVODNÍ
- VÝUSTKA - PŘÍVODNÍ
- TALÍŘOVÝ VENTIL - ODVODNÍ
- TALÍŘOVÝ VENTIL - PŘÍVODNÍ
- ŠIKMÝ NÁSTAVEC - VÝFUK
- ŠIKMÝ NÁSTAVEC - SÁNÍ
- VENTILÁTOR
- FILTR
- KLAPKA
- PRUŽNÁ VLOŽKA
- REGULAČNÍ KLAPKA
- REGULÁTOR PRŮTOKU
- TLUMIČ HLUKU
- ZPĚTNÁ KLAPKA
- POŽÁRNÍ KLAPKA
- POŽÁRNÍ STĚNOVÝ UZÁVĚR

LEGENDA IZOLACÍ

- TEPELNÁ IZOLACE
- TEPELNÁ IZOLACE S OPLECHOVÁNÍM
- POŽÁRNÍ IZOLACE 30 min
- POŽÁRNÍ IZOLACE 45 min
- POŽÁRNÍ IZOLACE 45 min S OPLECHOVÁNÍM

- OZNAČENÍ PRO PŘIVÁDĚNÝ VZDUCH
- OZNAČENÍ PRO ODVÁDĚNÝ VZDUCH
- OZNAČENÍ PRO PŘEPOUŠTĚNÍ VZDUCHU
- OZNAČENÍ PRO SÁNÍ VZDUCHU
- OZNAČENÍ PRO VÝFUK VZDUCHU

POZNÁMKY

PŘESNÁ POLOHA KONCOVÝCH PRVKŮ DLE KOO VÝKRESU

BARVA KONCOVÝCH A VIDITELNÝCH PRVK Ů DLE POŽADAVKU ARCH.

Revize	Popis revize	Datum
1	Doplnění větrání sklípků + zrušení některých PSU	6.2.2026

severka

± 0,000 = 224,62 m.n.m (BPV)

stavba
BD Na Mariánské cestě - 2. etapa

stupeň
Dokumentace pro provádění stavby

zpracovatel
TZB DESIGN
TZB design s.r.o.
Nad Šutkou 1811/12
182 00 Praha 8
+420 732 584 618
mysicka@tzb-design.cz
www.tzb-design.cz

zodpovědný projektant
Ing. Jiří Kejmar

vypracoval
Ing. Martin Kejmar

stavební objekt
SO03 - Bytový dům D2 a C2

část
D.1.2 - Technika prostředí staveb

profesní díl / členění části
03 - Vzduchotechnika

investor
DOMOPLAN a.s.
Trnitá 543/16, Brno, 602 00

generální projektant
BK engineering project s.r.o.
Hanusova 347/16
140 00 Praha 4
info@bkproject.cz

hlavní inženýr projektu
Ing. Libor Doležal

datum 10/2025
x A4 42
měřítko 1:50
číslo paré

Půdorys 1PP	zakázka	stupeň	s.objekt	část	členění	č. výkresu	revize
	365	**50**	**SO03**	**D.1.2**	**03**	**001**	**1**