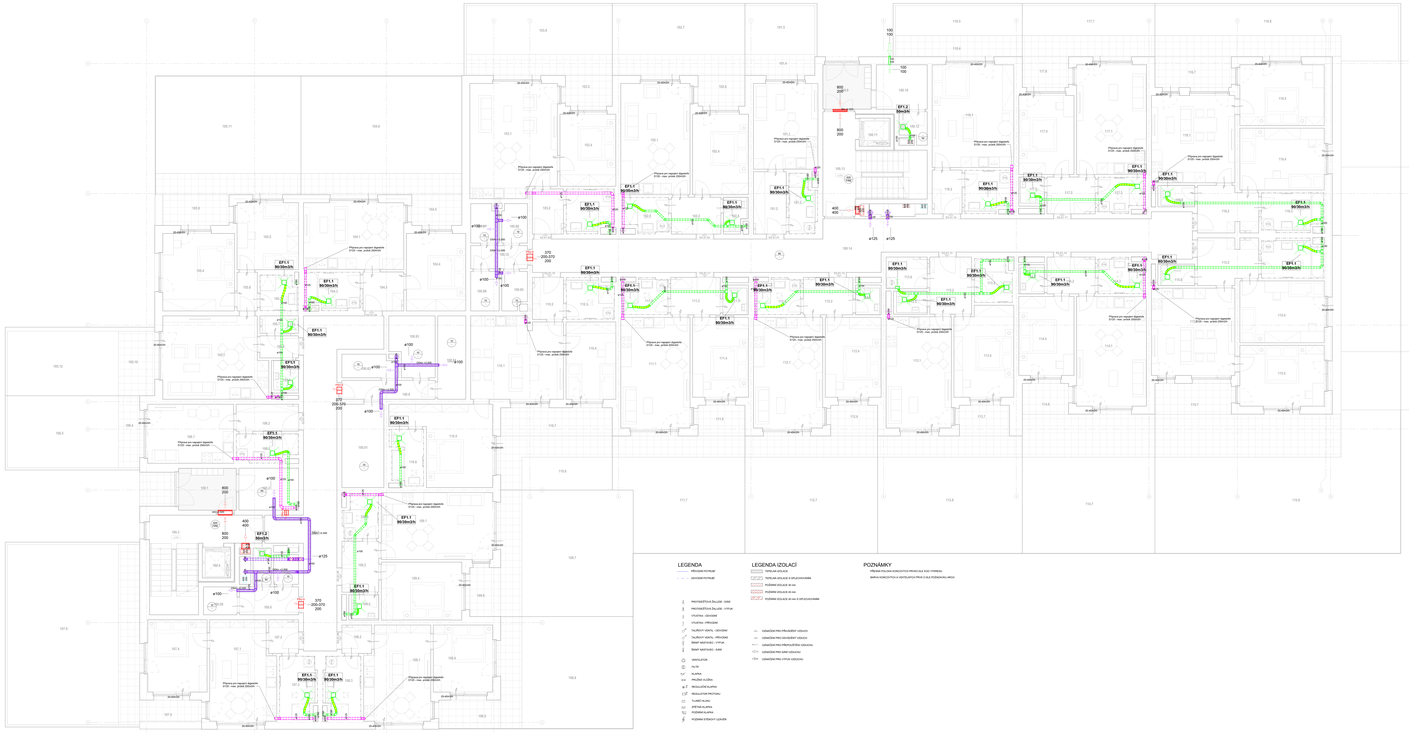

EF1.1
90/30m3/h
EF1.2
50m3/h
Příprava pro napojení digestoře
D125 - max. průtok 250m3/h
20-40m3/h
PSU-S
370
200-370
200
800
200
400
400
100
100
ø100
ø125
ø160
ø200
OSA= +2,500
OSA= +2,550
OSA= +2,505
OSA= +2,449
HH= +2,520
625
FIRE
750
FIRE
PK1.1
PK1.2
100.1
100.2
100.3
100.4
100.5
100.6
100.8
100.9
100.10
100.11
100.12
100.13
100.14
100.15
100.16
100.17
100.19
100.20
100.21
100.22
100.23
100.59
100.61
100.62
100.63
100.64
100.65
100.66
100.67
100.68
100.69
100.70
101.1
101.2
101.3
101.4
101.5
102.1
102.2
102.3
102.4
102.5
102.6
102.7
103.1
103.2
103.3
103.4
103.5
103.6
104.1
104.2
104.3
104.4
104.5
104.6
105.1
105.2
105.3
105.4
105.5
105.6
105.7
105.8
105.9
105.10
105.11
105.12
106.1
106.2
106.3
106.4
106.5
107.1
107.2
107.3
107.4
107.5
107.6
107.7
108.1
108.2
108.3
108.4
108.5
108.6
108.7
109.1
109.2
109.3
109.4
109.5
109.6
109.7
110.1
110.2
110.3
110.4
110.5
110.6
110.7
110.8
111.1
111.2
111.3
111.4
111.5
111.6
111.7
111.8
111.9
111.10
112.1
112.2
112.3
112.4
112.5
112.6
112.7
112.8
113.1
113.2
113.3
113.4
113.5
113.6
113.7
113.8
114.1
114.2
114.3
114.4
114.6
114.7
115.1
115.2
115.4
115.5
115.6
115.7
115.8
116.1
116.2
116.3
116.4
116.5
116.6
116.7
116.8
117.1
117.2
117.3
117.4
117.5
117.6
117.7
118.1
118.2
118.4
118.5
D2.01.01
D2.01.02
D2.01.03
D2.01.04
D2.01.10
D2.01.11
D2.01.12
D2.01.13
D2.01.14
D2.01.15
D2.01.16
D2.01.17
D2.01.18
C2.01.01
C2.01.02
C2.01.03
C2.01.04
C2.01.05
C2.01.06
C2.01.08
C2.01.10
C2.01.11
C2.01.12
C2.01.13
severka

LEGENDA

- PŘÍVODNÍ POTRUBÍ
- ODVODNÍ POTRUBÍ
- PROTIDEŠŤOVÁ ŽALUZIE - SÁNÍ
- PROTIDEŠŤOVÁ ŽALUZIE - VÝFUK
- VÝUSTKA - ODVODNÍ
- VÝUSTKA - PŘÍVODNÍ
- TALÍŘOVÝ VENTIL - ODVODNÍ
- TALÍŘOVÝ VENTIL - PŘÍVODNÍ
- ŠIKMÝ NÁSTAVEC - VÝFUK
- ŠIKMÝ NÁSTAVEC - SÁNÍ
- VENTILÁTOR
- FILTR
- KLAPKA
- PRUŽNÁ VLOŽKA
- REGULAČNÍ KLAPKA
- REGULÁTOR PRŮTOKU
- TLUMIČ HLUKU
- ZPĚTNÁ KLAPKA
- POŽÁRNÍ KLAPKA
- POŽÁRNÍ STĚNOVÝ UZÁVĚR

LEGENDA IZOLACÍ

- TEPELNÁ IZOLACE
- TEPELNÁ IZOLACE S OPLECHOVÁNÍM
- POŽÁRNÍ IZOLACE 30 min
- POŽÁRNÍ IZOLACE 45 min
- POŽÁRNÍ IZOLACE 45 min S OPLECHOVÁNÍM
- OZNAČENÍ PRO PŘIVÁDĚNÝ VZDUCH
- OZNAČENÍ PRO ODVÁDĚNÝ VZDUCH
- OZNAČENÍ PRO PŘEPOUŠTĚNÍ VZDUCHU
- OZNAČENÍ PRO SÁNÍ VZDUCHU
- OZNAČENÍ PRO VÝFUK VZDUCHU

POZNÁMKY

PŘESNÁ POLOHA KONCOVÝCH PRVKŮ DLE KOO VÝKRESU

BARVA KONCOVÝCH A VIDITELNÝCH PRVKŮ DLE POŽADAVKU ARCH.

Revize	Popis revize	Datum

± 0,000 = 224,62 m.n.m (BPV)

stavba
BD Na Mariánské cestě - 2. etapa

stupeň
Dokumentace pro provádění stavby

zpracovatel
TZB DESIGN
TZB design s.r.o.
Nad Šutkou 1811/12
182 00 Praha 8
+420 732 584 618
mysicka@tzb-design.cz
www.tzb-design.cz

zodpovědný projektant
Ing. Jiří Kejmar

vypracoval
Ing. Martin Kejmar

stavební objekt
SO03 - Bytový dům D2 a C2

část
D.1.2 - Technika prostředí staveb

profesní díl / členění části
03 - Vzduchotechnika

investor
DOMOPLAN a.s.
Trnitá 543/16, Brno, 602 00

generální projektant
BK engineering project s.r.o.
Hanusova 347/16
140 00 Praha 4
info@bkproject.cz

hlavní inženýr projektu
Ing. Libor Doležal

datum 10/2025
x A4 42
měřítko 1:50
číslo paré

	zakázka	stupeň	s.objekt	část	členění	č. výkresu	revize
Půdorys 1NP	365	50	SO03	D.1.2	03	002	