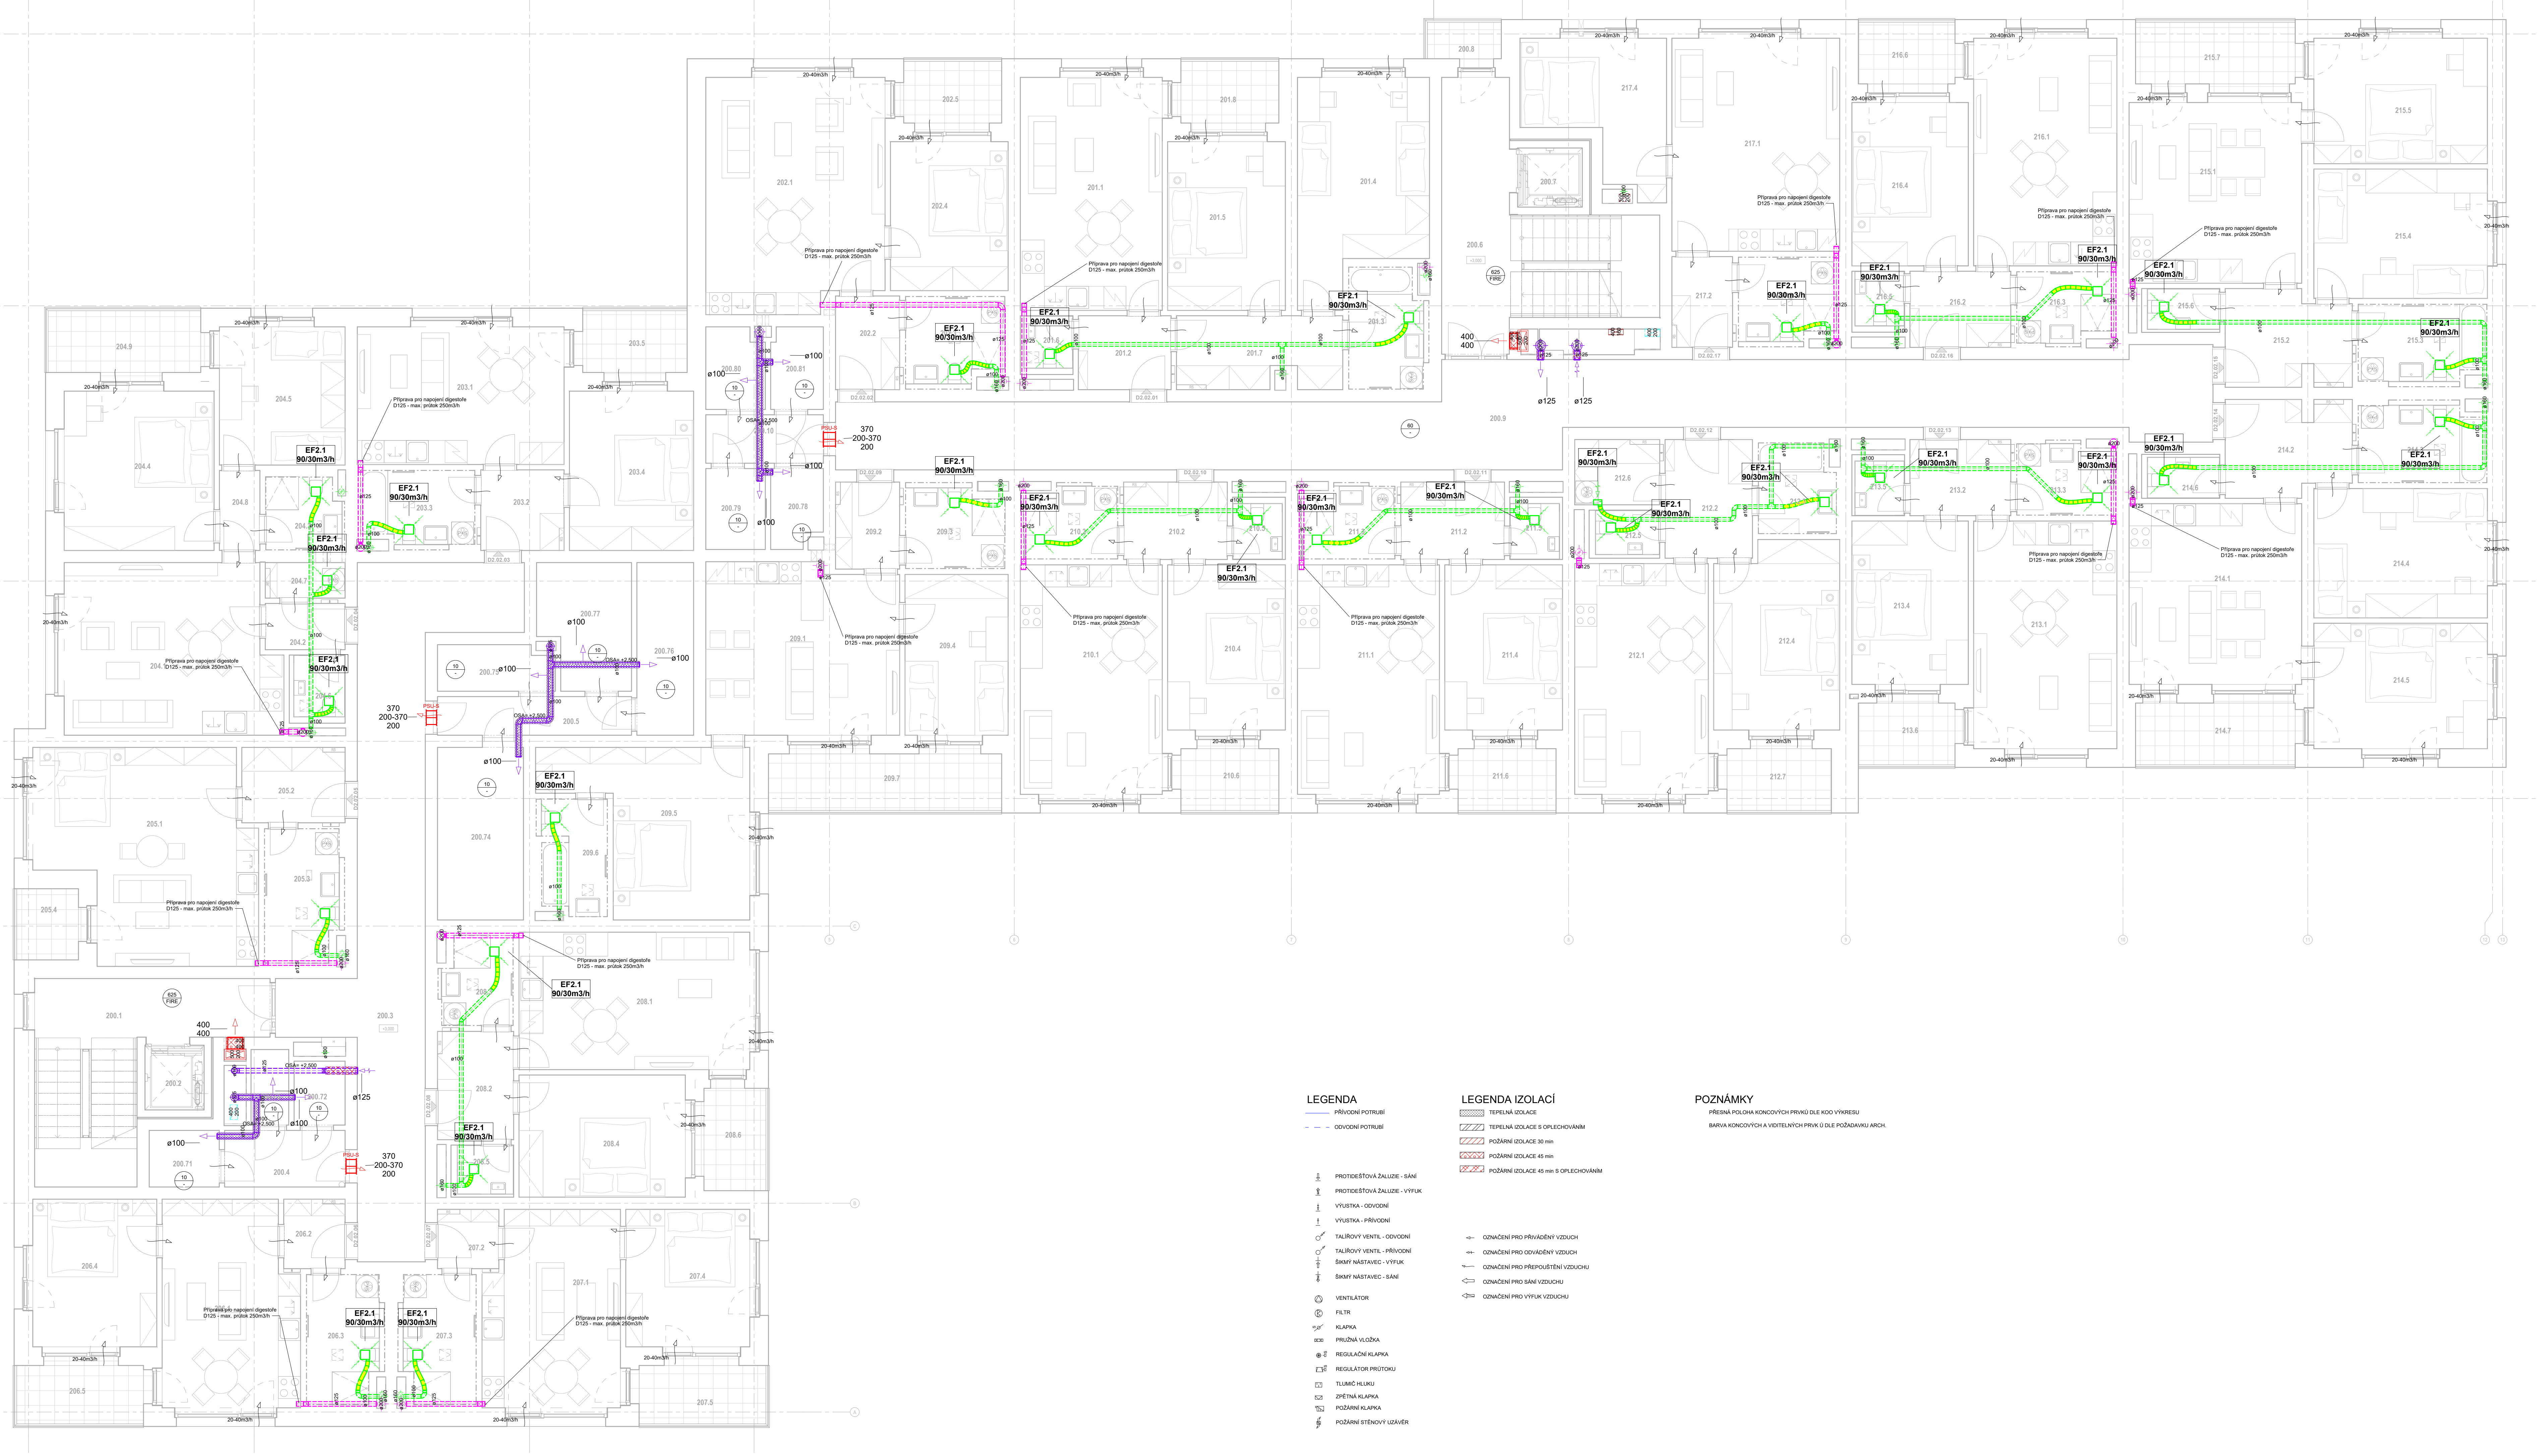
EF2.1
90/30m3/h
Příprava pro napojení digestoře
D125 - max. průtok 250m3/h
20-40m3/h
PSU-S
370
200-370
200
400
400
ø100
ø125
ø160
ø200
OSA= +2,500
OSA= +2,550
OSA= +2,505
625
FIRE
60
10
PK2.1
PK2.2
D2.02.01
D2.02.02
D2.02.03
D2.02.09
D2.02.10
D2.02.11
D2.02.12
D2.02.13
D2.02.16
D2.02.17
200.1
200.2
200.3
200.4
200.5
200.6
200.7
200.8
200.9
200.71
200.72
200.73
200.74
200.75
200.76
200.77
200.78
200.79
200.80
200.81
201.1
201.2
201.3
201.4
201.5
201.6
201.7
201.8
202.1
202.2
202.4
202.5
203.1
203.2
203.3
203.4
203.5
204.1
204.2
204.4
204.5
204.7
204.8
204.9
205.1
205.2
205.3
205.4
206.1
206.2
206.3
206.4
206.5
207.1
207.2
207.3
207.4
207.5
208.1
208.2
208.3
208.4
208.5
208.6
209.1
209.2
209.3
209.4
209.5
209.6
209.7
210.1
210.2
210.3
210.4
210.5
210.6
211.1
211.2
211.3
211.4
211.5
211.6
212.1
212.2
212.4
212.5
212.6
212.7
213.1
213.2
213.3
213.4
213.5
213.6
214.1
214.2
214.4
214.5
214.6
214.7
215.1
215.2
215.3
215.4
215.5
215.6
215.7
216.1
216.2
216.3
216.4
216.5
216.6
217.1
217.2
217.4

LEGENDA

- PŘÍVODNÍ POTRUBÍ
- ODVODNÍ POTRUBÍ
- PROTIDEŠŤOVÁ ŽALUZIE - SÁNÍ
- PROTIDEŠŤOVÁ ŽALUZIE - VÝFUK
- VÝUSTKA - ODVODNÍ
- VÝUSTKA - PŘÍVODNÍ
- TALÍŘOVÝ VENTIL - ODVODNÍ
- TALÍŘOVÝ VENTIL - PŘÍVODNÍ
- ŠIKMÝ NÁSTAVEC - VÝFUK
- ŠIKMÝ NÁSTAVEC - SÁNÍ
- VENTILÁTOR
- FILTR
- KLAPKA
- PRUŽNÁ VLOŽKA
- REGULAČNÍ KLAPKA
- REGULÁTOR PRŮTOKU
- TLUMIČ HLUKU
- ZPĚTNÁ KLAPKA
- POŽÁRNÍ KLAPKA
- POŽÁRNÍ STĚNOVÝ UZÁVĚR

LEGENDA IZOLACÍ

- TEPELNÁ IZOLACE
- TEPELNÁ IZOLACE S OPLECHOVÁNÍM
- POŽÁRNÍ IZOLACE 30 min
- POŽÁRNÍ IZOLACE 45 min
- POŽÁRNÍ IZOLACE 45 min S OPLECHOVÁNÍM
- OZNAČENÍ PRO PŘIVÁDĚNÝ VZDUCH
- OZNAČENÍ PRO ODVÁDĚNÝ VZDUCH
- OZNAČENÍ PRO PŘEPOUŠTĚNÍ VZDUCHU
- OZNAČENÍ PRO SÁNÍ VZDUCHU
- OZNAČENÍ PRO VÝFUK VZDUCHU

POZNÁMKY

PŘESNÁ POLOHA KONCOVÝCH PRVKŮ DLE KOO VÝKRESU

BARVA KONCOVÝCH A VIDITELNÝCH PRVKŮ DLE POŽADAVKU ARCH.


EF2.1
90/30m3/h
Příprava pro napojení digestoře
D125 - max. průtok 250m3/h
20-40m3/h
PSU-S
370
200-370
200
400
400
ø100
ø125
ø160
ø200
OSA= +2,500
OSA= +2,550
OSA= +2,505
750
FIRE
50
30
10
PK2.1
PK2.2
C2.02.01
C2.02.02
C2.02.03
C2.02.04
C2.02.06
C2.02.08
C2.02.10
C2.02.11
C2.02.12
C2.02.13
200.12
200.13
200.14
200.15
200.82
200.83
201.1
201.2
201.3
201.4
201.5
201.6
202.1
202.2
202.3
202.4
202.5
202.6
203.1
203.2
203.3
203.4
204.1
204.2
204.3
204.4
204.5
205.1
205.2
205.3
205.4
205.5
206.1
206.2
206.3
206.4
207.1
207.2
207.3
207.4
207.5
207.6
208.1
208.2
208.4
208.5
208.6
209.1
209.2
209.3
209.4
209.5
209.6
210.1
210.2
210.3
210.4
211.1
211.2
211.3
211.4
211.5
211.6
211.7
211.8
211.9
212.1
212.2
212.4
212.5
212.6
212.7
213.1
213.2
213.3
213.4
213.5
213.6

Revize	Popis revize	Datum

severka

± 0,000 = 224,62 m.n.m (BPV)

stavba **BD Na Mariánské cestě - 2. etapa**		**stupeň** Dokumentace pro provádění stavby
zpracovatel TZB DESIGN TZB design s.r.o. Nad Šutkou 1811/12 182 00 Praha 8 +420 732 584 618 mysicka@tzb-design.cz www.tzb-design.cz	**zodpovědný projektant** Ing. Jiří Kejmar **vypracoval** Ing. Martin Kejmar	**stavební objekt** SO03 - Bytový dům D2 a C2 **část** D.1.2 - Technika prostředí staveb **profesní díl / členění části** 03 - Vzduchotechnika
investor DOMOPLAN a.s. Trnitá 543/16, Brno, 602 00	**generální projektant** BK engineering project s.r.o. Hanusova 347/16 140 00 Praha 4 info@bkproject.cz **hlavní inženýr projektu** Ing. Libor Doležal	**datum** 10/2025 **x A4** 42 **měřítko** 1:50 **číslo paré**

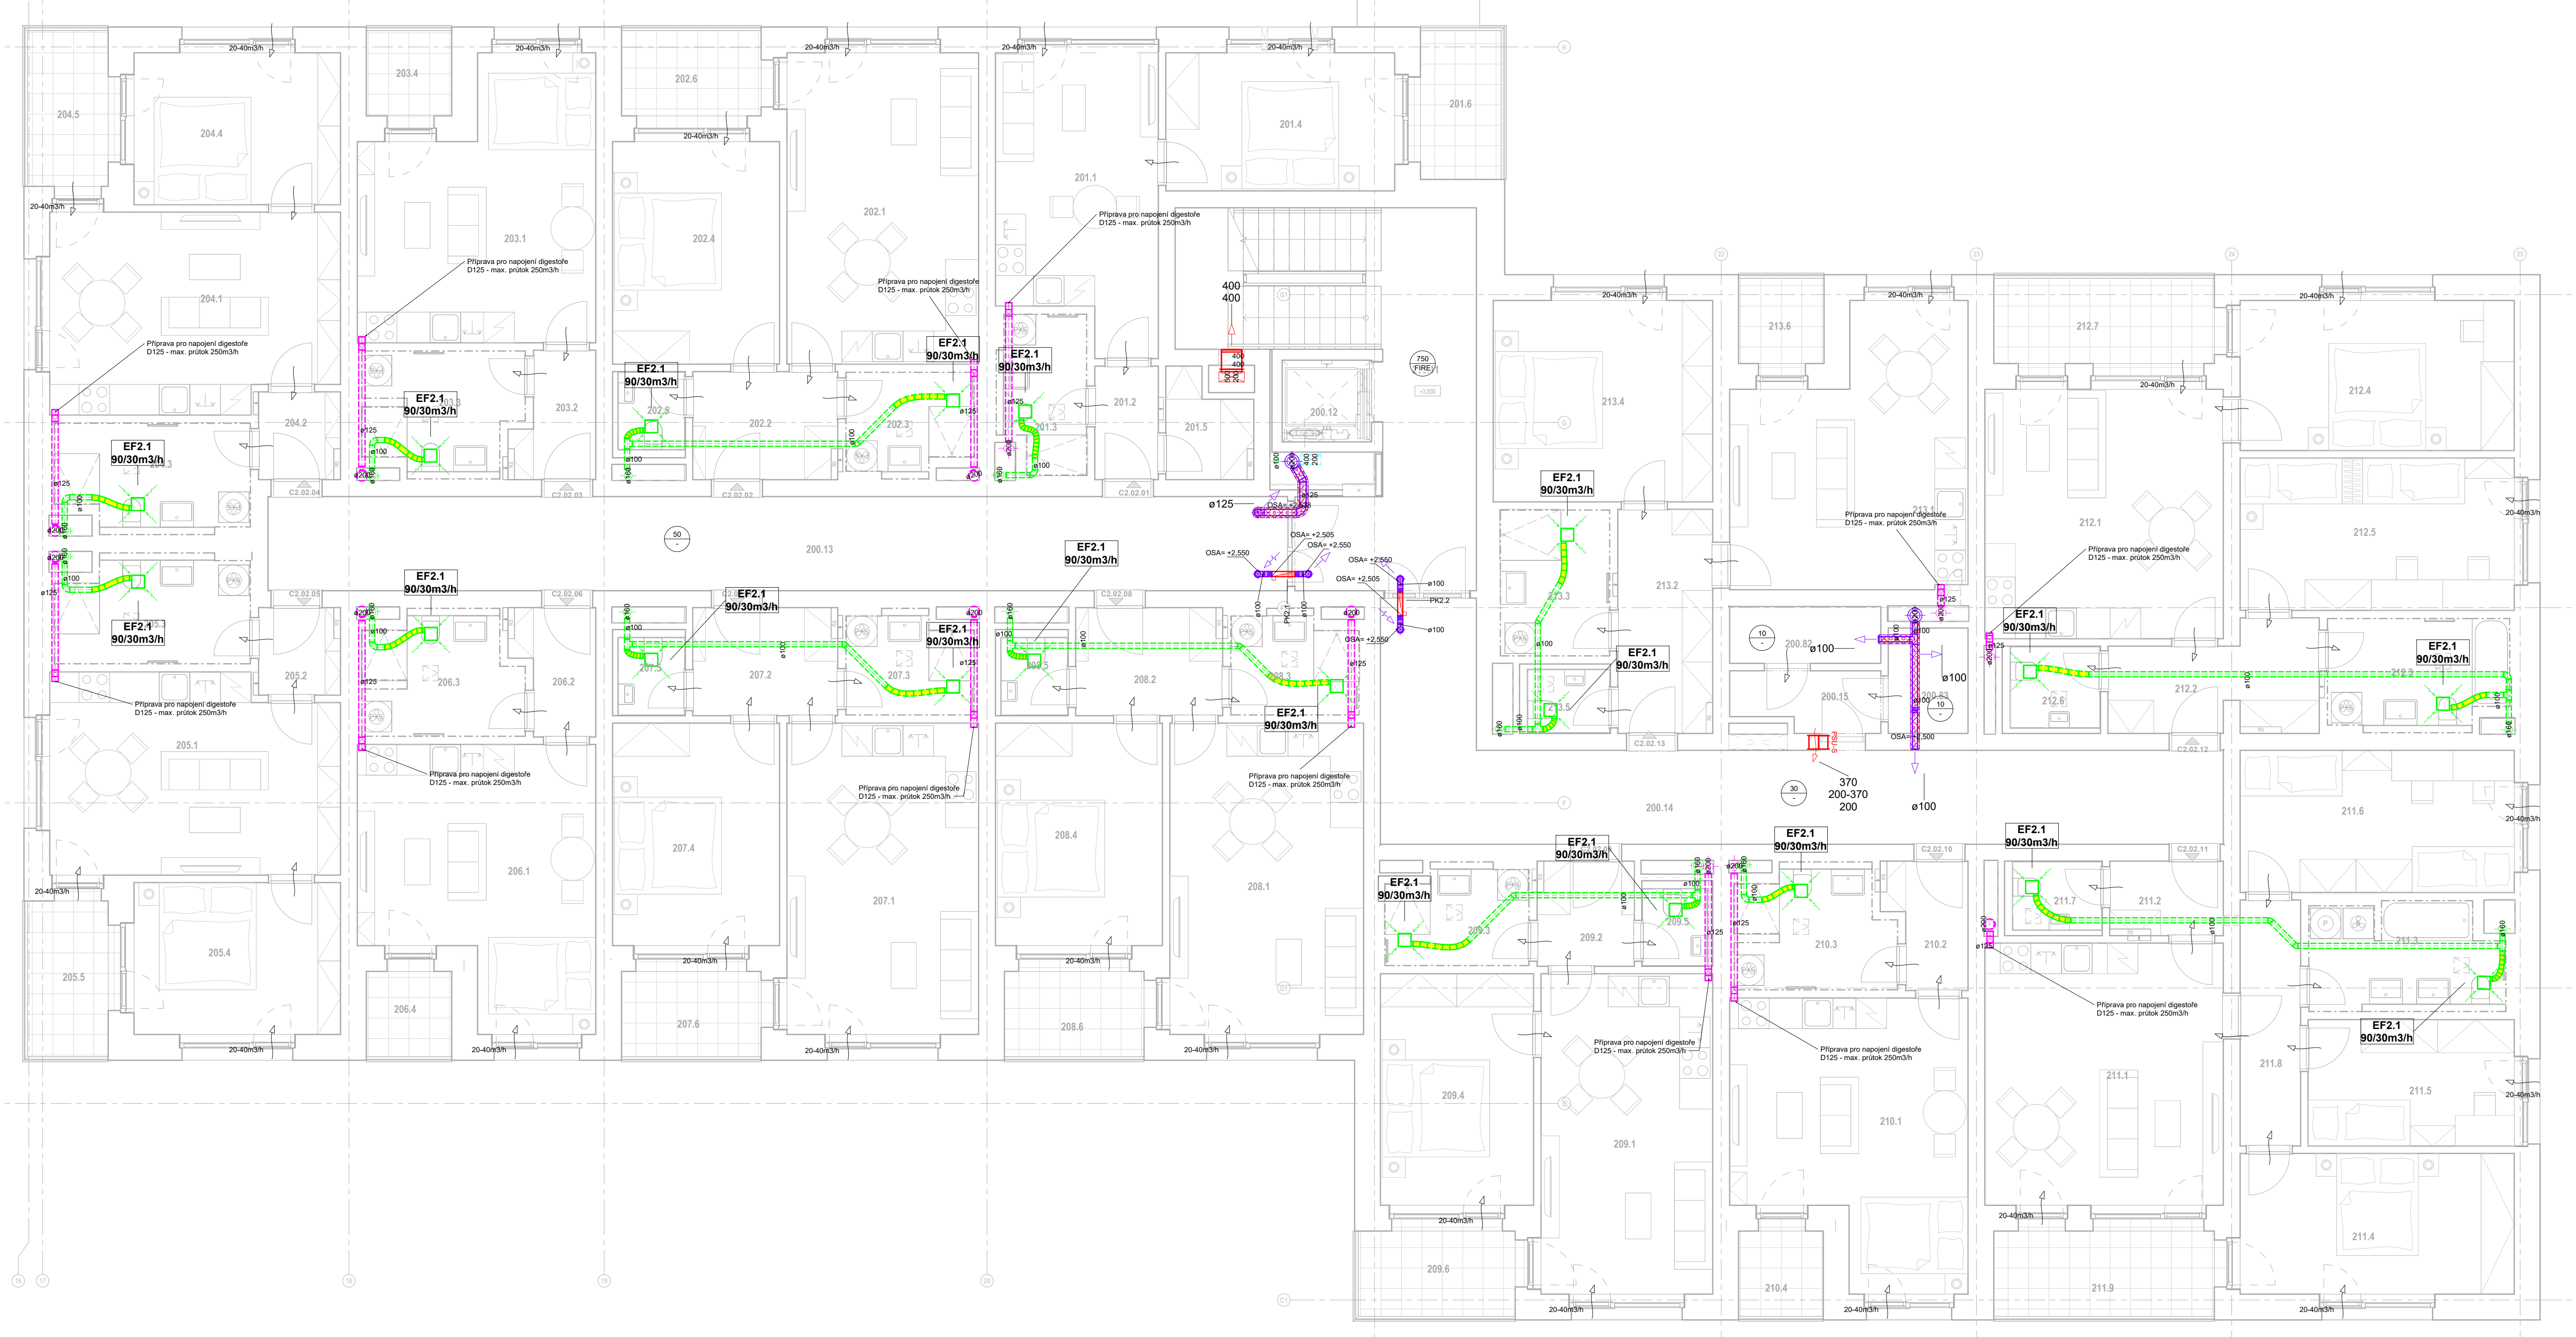Půdorys 2NP	zakázka	stupeň	s.objekt	část	členění	č. výkresu	revize
	365	**50**	**SO03**	**D.1.2**	**03**	**003**	