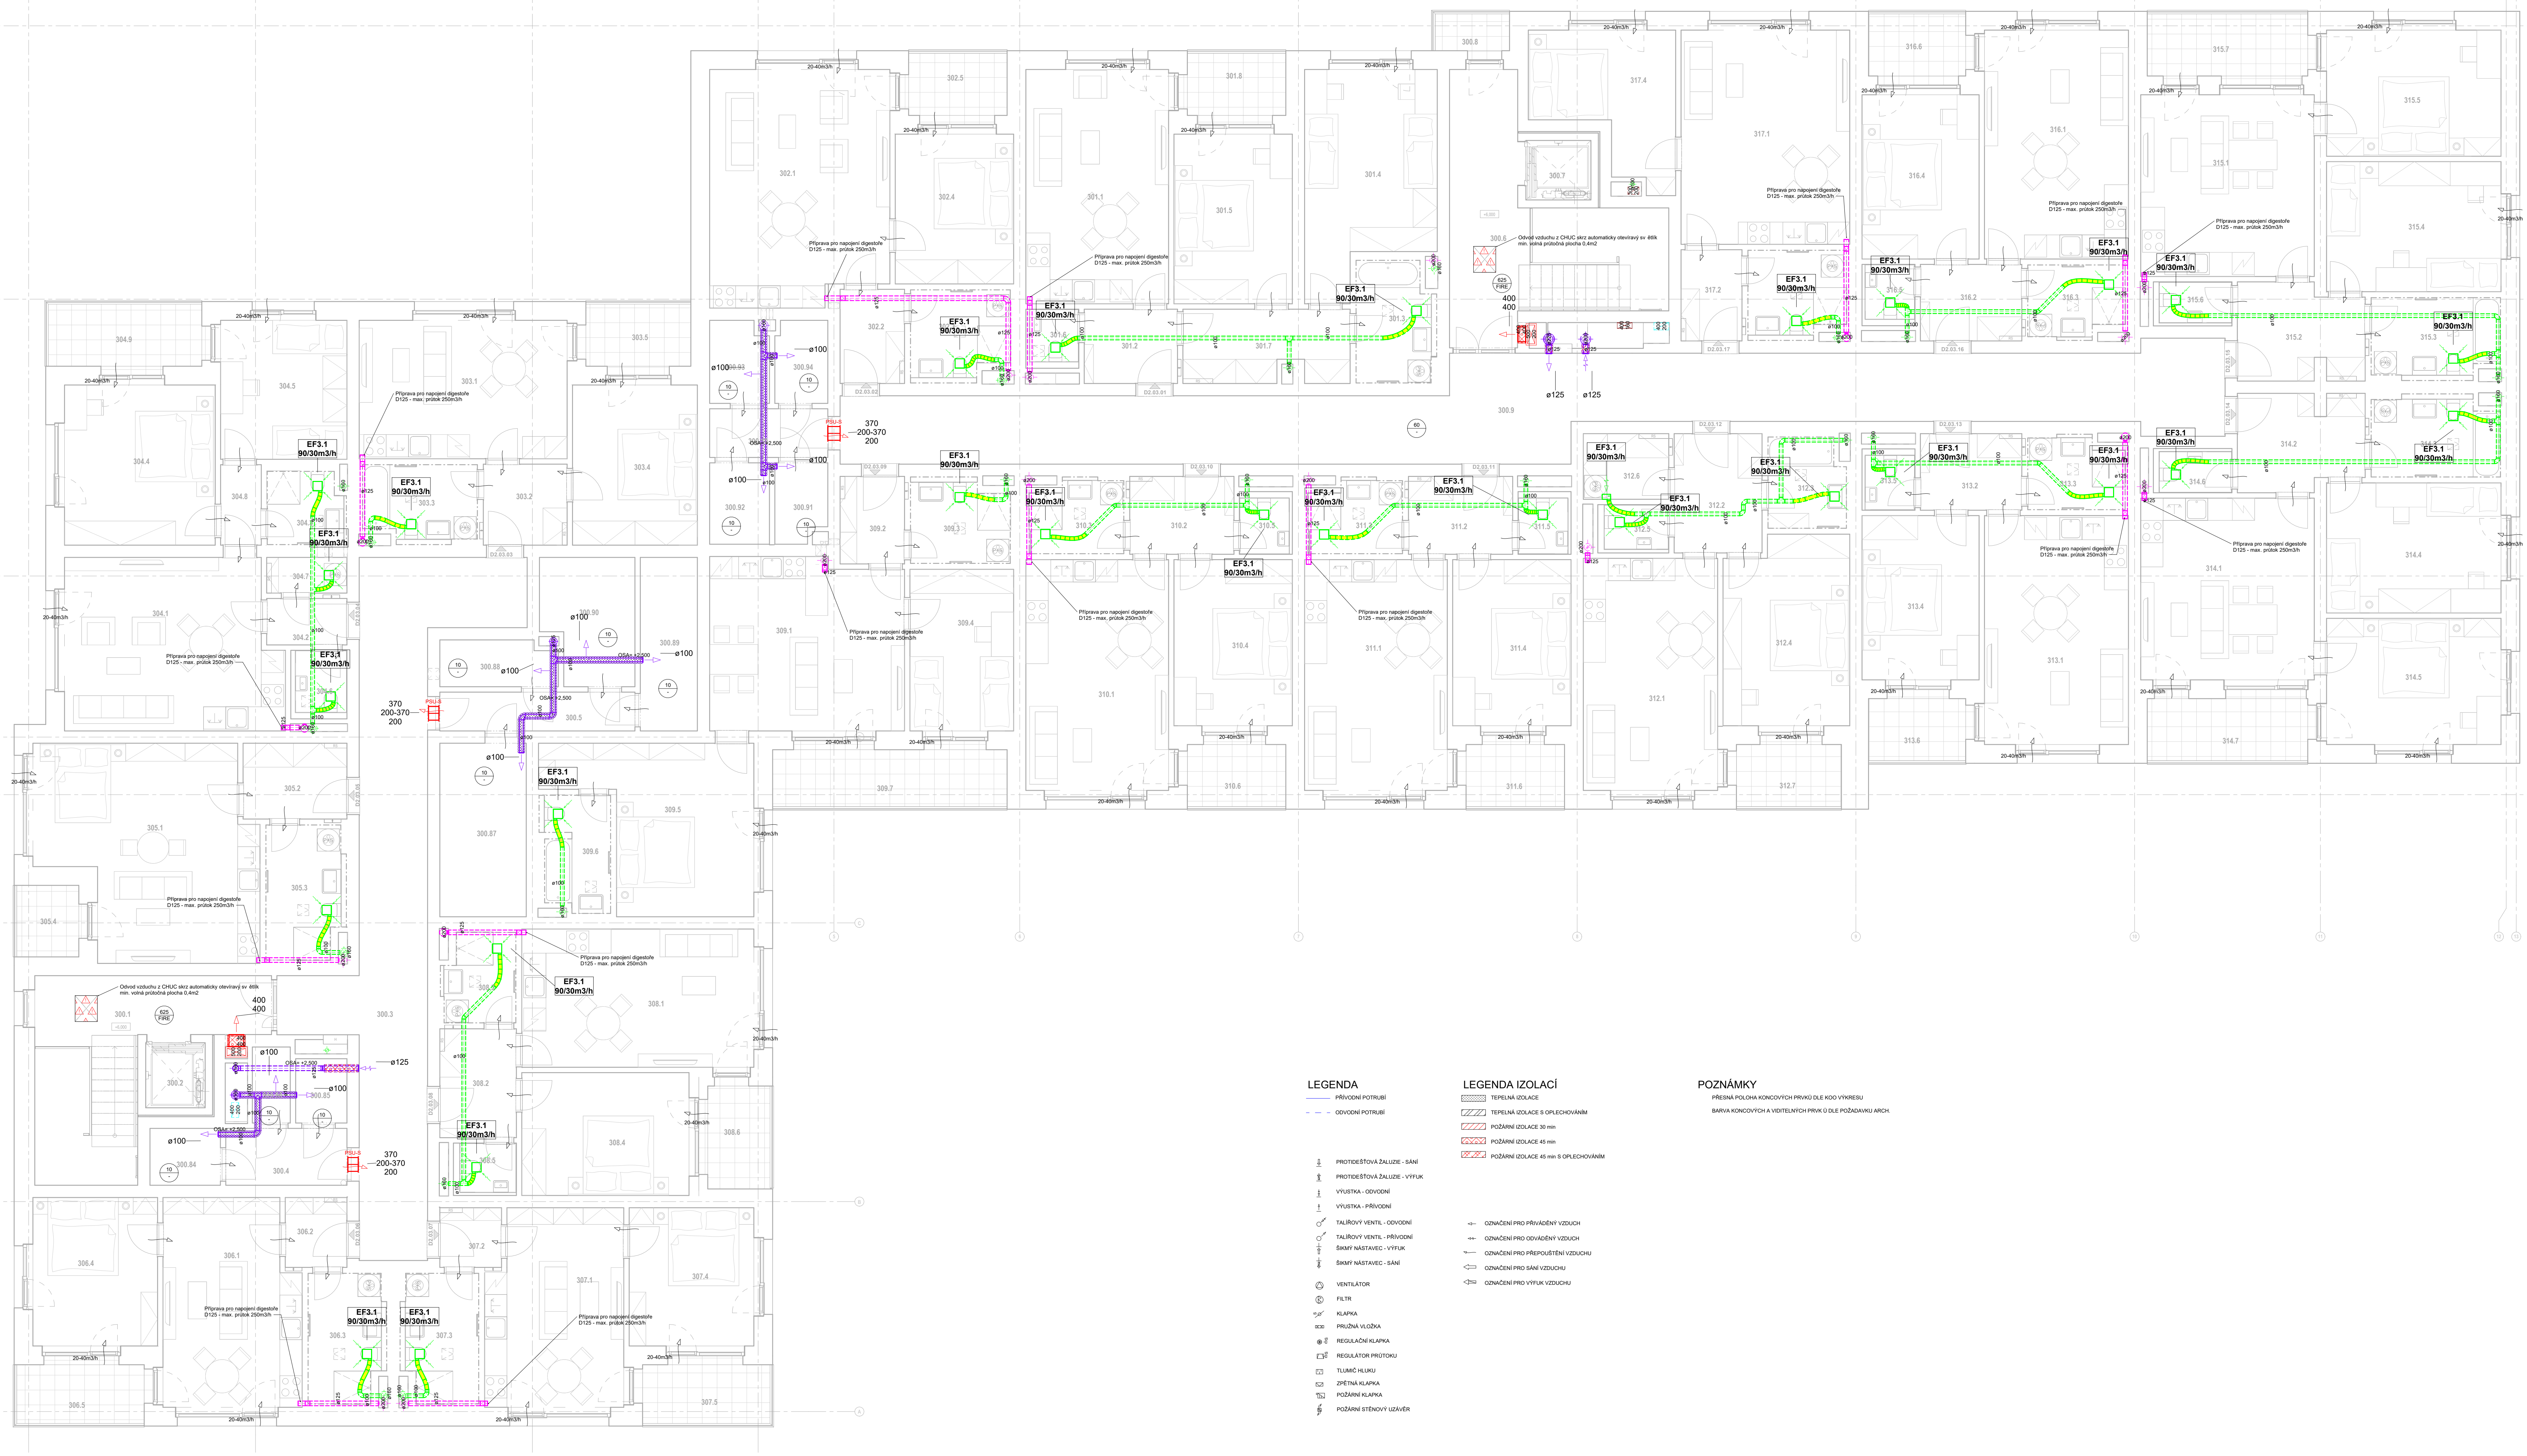
EF3.1
90/30m3/h
Příprava pro napojení digestoře
D125 - max. průtok 250m3/h
Odvod vzduchu z CHUC skrz automaticky otevíravý sv ětlík
min. volná průtočná plocha 0,4m2
20-40m3/h
PSU-S
370
200-370
200
400
400
625
FIRE
ø100
ø125
ø160
ø200
OSA= +2,500
300.1
300.2
300.3
300.4
300.5
300.6
300.7
300.8
300.9
300.84
300.85
300.87
300.88
300.89
300.90
300.91
300.92
300.93
300.94
301.1
301.2
301.3
301.4
301.5
301.6
301.7
301.8
302.1
302.2
302.3
302.4
302.5
303.1
303.2
303.3
303.4
303.5
304.1
304.2
304.4
304.5
304.6
304.7
304.8
304.9
305.1
305.2
305.3
305.4
306.1
306.2
306.3
306.4
306.5
307.1
307.2
307.3
307.4
307.5
308.1
308.2
308.4
308.5
308.6
309.1
309.2
309.3
309.4
309.5
309.6
309.7
310.1
310.2
310.3
310.4
310.5
310.6
311.1
311.2
311.3
311.4
311.5
311.6
312.1
312.2
312.3
312.4
312.5
312.6
312.7
313.1
313.2
313.3
313.4
313.5
313.6
314.1
314.2
314.4
314.5
314.6
314.7
315.1
315.2
315.3
315.4
315.5
315.6
315.7
316.1
316.2
316.3
316.4
316.5
316.6
317.1
317.2
317.4
D2.03.01
D2.03.02
D2.03.03
D2.03.09
D2.03.10
D2.03.11
D2.03.12
D2.03.13
D2.03.14
D2.03.15
D2.03.16
D2.03.17


EF3.1
90/30m3/h
Příprava pro napojení digestoře
D125 - max. průtok 250m3/h
Odvod vzduchu z CHUC skrz automaticky otevíravý sv ětlík
min. volná průtočná plocha 0,4 2m2
20-40m3/h
PSU-S
370
200-370
200
400
400
750
FIRE
PK3.1
PK3.2
OSA= +2,505
OSA= +2,550
OSA= +2,500
ø100
ø125
ø160
ø200
300.11
300.12
300.13
300.14
300.15
300.95
301.1
301.2
301.3
301.4
301.5
301.6
302.1
302.2
302.3
302.4
302.5
302.6
303.1
303.2
303.4
304.1
304.2
304.3
304.4
304.5
305.1
305.2
305.3
305.4
305.5
306.1
306.2
306.3
306.4
307.1
307.2
307.3
307.4
307.5
307.6
308.1
308.2
308.4
308.5
308.6
309.1
309.2
309.3
309.4
309.5
309.6
310.1
310.2
310.3
310.4
311.1
311.2
311.3
311.4
311.5
311.6
311.7
311.8
311.9
312.1
312.2
312.4
312.5
312.6
312.7
313.2
313.3
313.4
313.5
313.6
C2.03.01
C2.03.02
C2.03.03
C2.03.04
C2.03.05
C2.03.06
C2.03.08
C2.03.10
C2.03.11
C2.03.12
C2.03.13

LEGENDA

- PŘÍVODNÍ POTRUBÍ
- ODVODNÍ POTRUBÍ
- PROTIDEŠŤOVÁ ŽALUZIE - SÁNÍ
- PROTIDEŠŤOVÁ ŽALUZIE - VÝFUK
- VÝUSTKA - ODVODNÍ
- VÝUSTKA - PŘÍVODNÍ
- TALÍŘOVÝ VENTIL - ODVODNÍ
- TALÍŘOVÝ VENTIL - PŘÍVODNÍ
- ŠIKMÝ NÁSTAVEC - VÝFUK
- ŠIKMÝ NÁSTAVEC - SÁNÍ
- VENTILÁTOR
- FILTR
- KLAPKA
- PRUŽNÁ VLOŽKA
- REGULAČNÍ KLAPKA
- REGULÁTOR PRŮTOKU
- TLUMIČ HLUKU
- ZPĚTNÁ KLAPKA
- POŽÁRNÍ KLAPKA
- POŽÁRNÍ STĚNOVÝ UZÁVĚR

LEGENDA IZOLACÍ

- TEPELNÁ IZOLACE
- TEPELNÁ IZOLACE S OPLECHOVÁNÍM
- POŽÁRNÍ IZOLACE 30 min
- POŽÁRNÍ IZOLACE 45 min
- POŽÁRNÍ IZOLACE 45 min S OPLECHOVÁNÍM

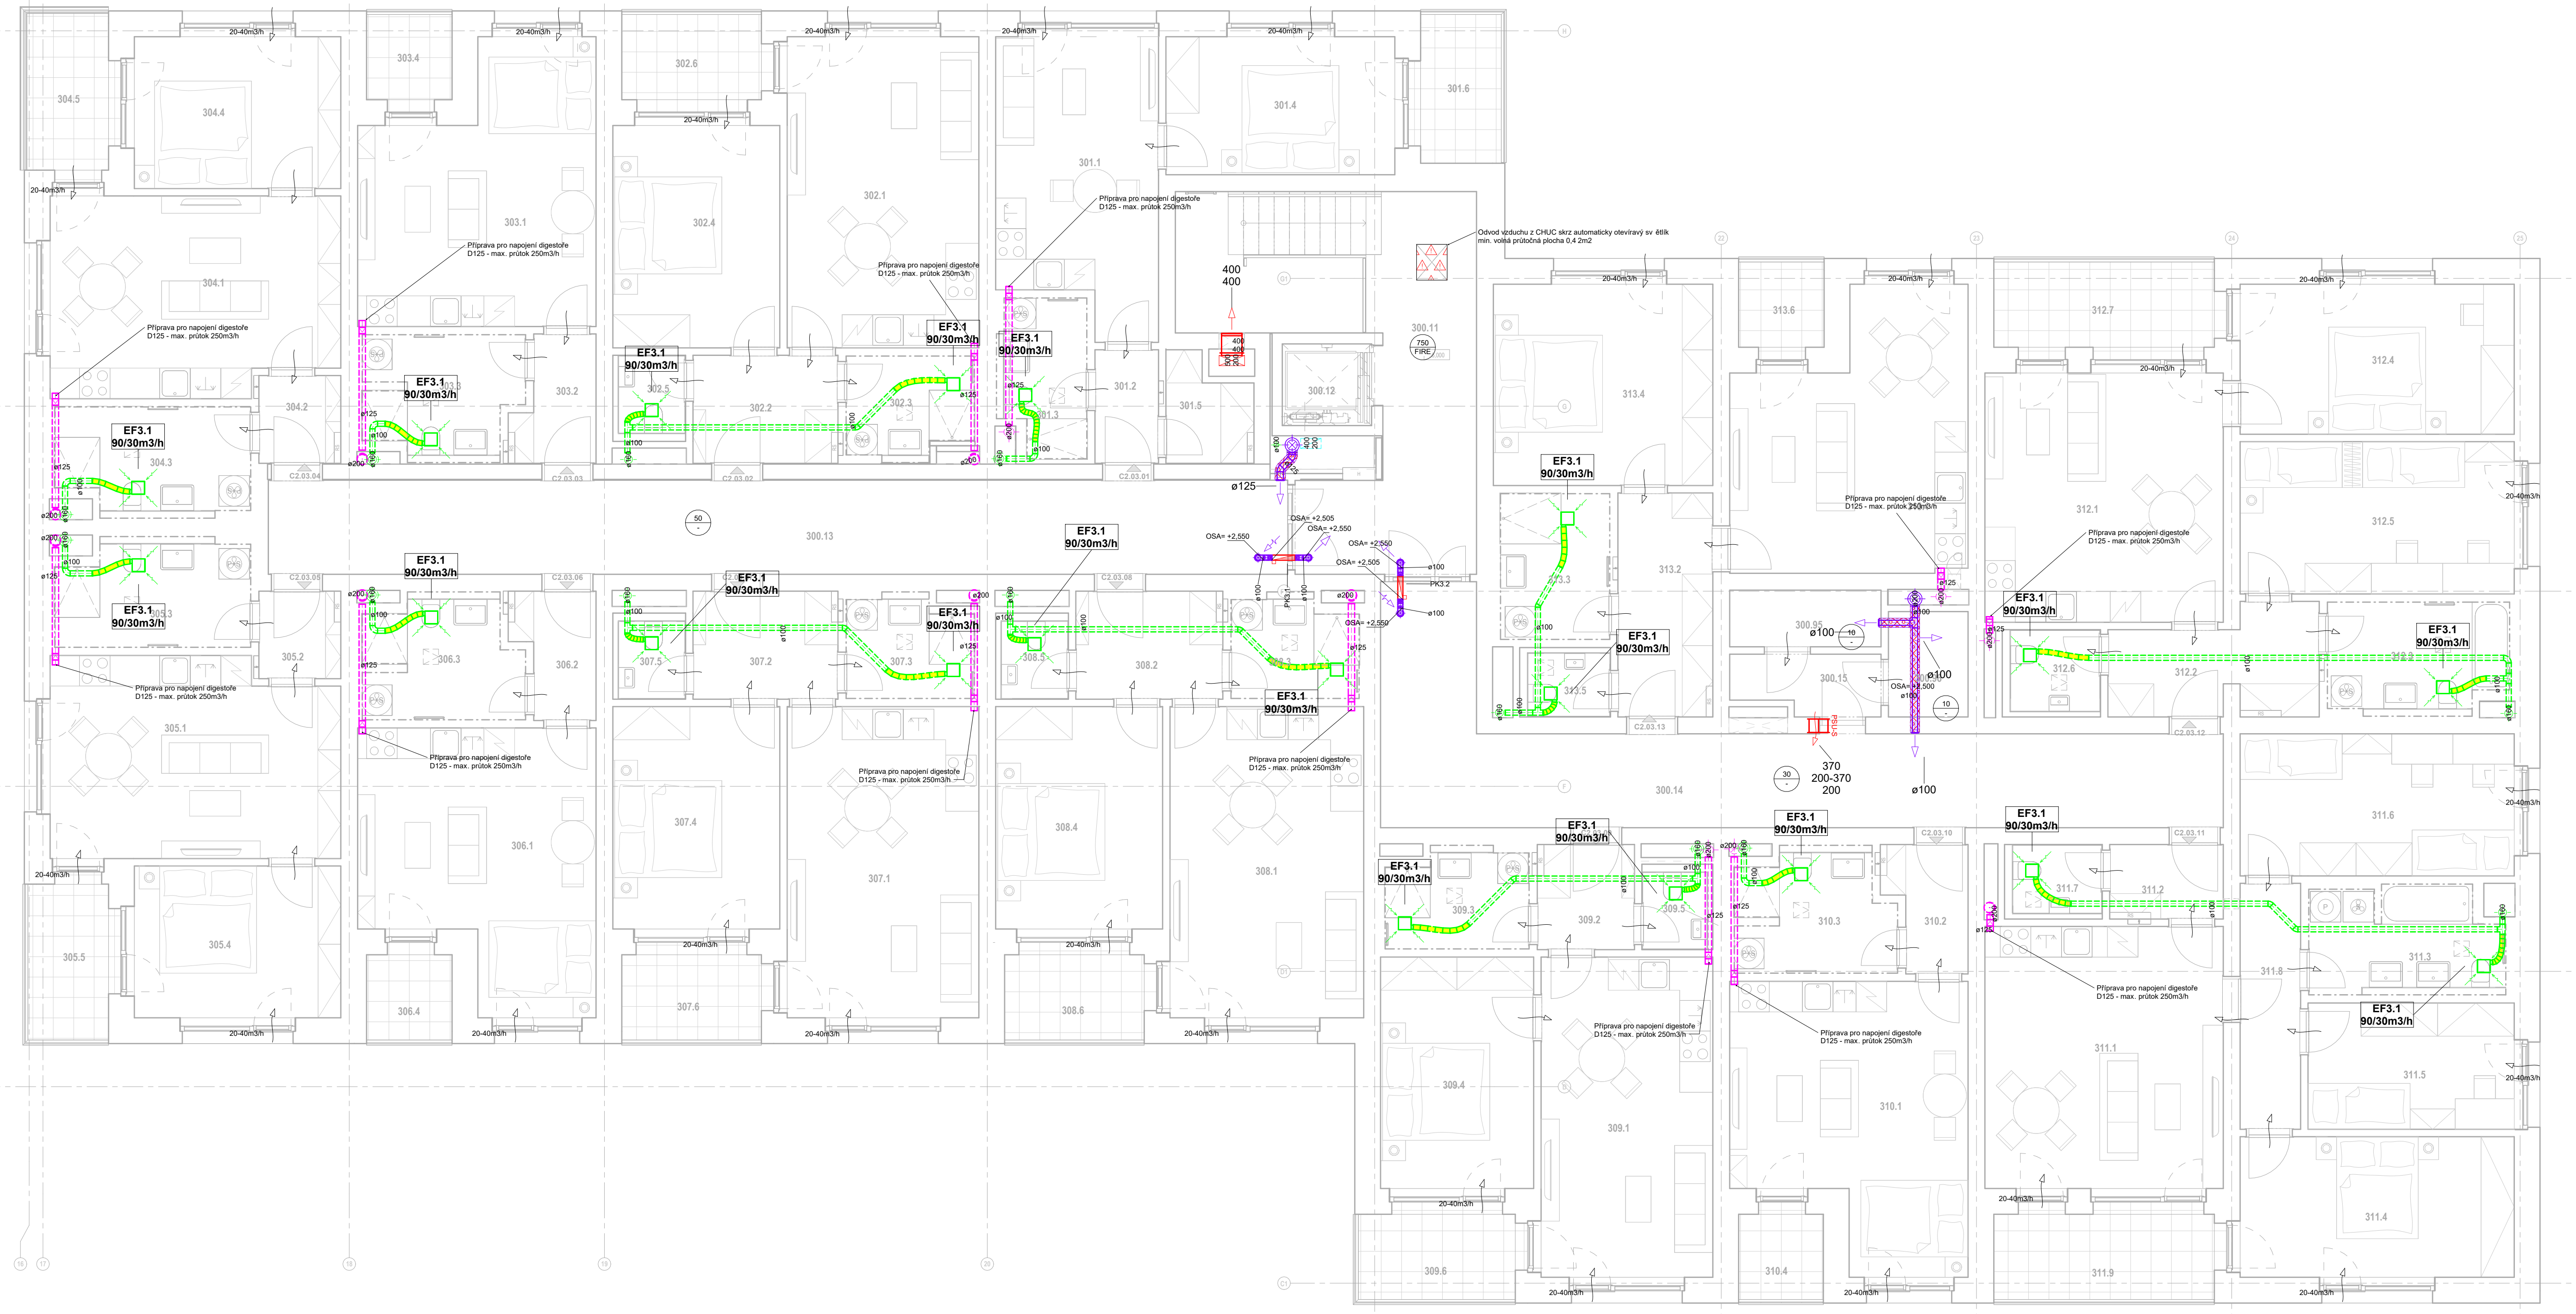- OZNAČENÍ PRO PŘIVÁDĚNÝ VZDUCH
- OZNAČENÍ PRO ODVÁDĚNÝ VZDUCH
- OZNAČENÍ PRO PŘEPOUŠTĚNÍ VZDUCHU
- OZNAČENÍ PRO SÁNÍ VZDUCHU
- OZNAČENÍ PRO VÝFUK VZDUCHU

POZNÁMKY

PŘESNÁ POLOHA KONCOVÝCH PRVKŮ DLE KOO VÝKRESU

BARVA KONCOVÝCH A VIDITELNÝCH PRVK Ů DLE POŽADAVKU ARCH.

Revize	Popis revize	Datum

severka

± 0,000 = 224,62 m.n.m (BPV)

stavba **BD Na Mariánské cestě - 2. etapa**		stupeň Dokumentace pro provádění stavby
zpracovatel TZBDESIGN TZB design s.r.o. Nad Šutkou 1811/12 182 00 Praha 8 +420 732 584 618 mysicka@tzb-design.cz www.tzb-design.cz	zodpovědný projektant Ing. Jiří Kejmar vypracoval Ing. Martin Kejmar	stavební objekt SO03 - Bytový dům D2 a C2 část D.1.2 - Technika prostředí staveb profesní díl / členění části 03 - Vzduchotechnika
investor DOMOPLAN a.s. Trnitá 543/16, Brno, 602 00	generální projektant BK engineering project s.r.o. Hanusova 347/16 140 00 Praha 4 info@bkproject.cz hlavní inženýr projektu Ing. Libor Doležal	datum 10/2025 x A4 42 měřítko 1:50 číslo paré

Půdorys 3NP	zakázka	stupeň	s.objekt	část	členění	č. výkresu	revize
	365	50	SO03	D.1.2	03	004	