


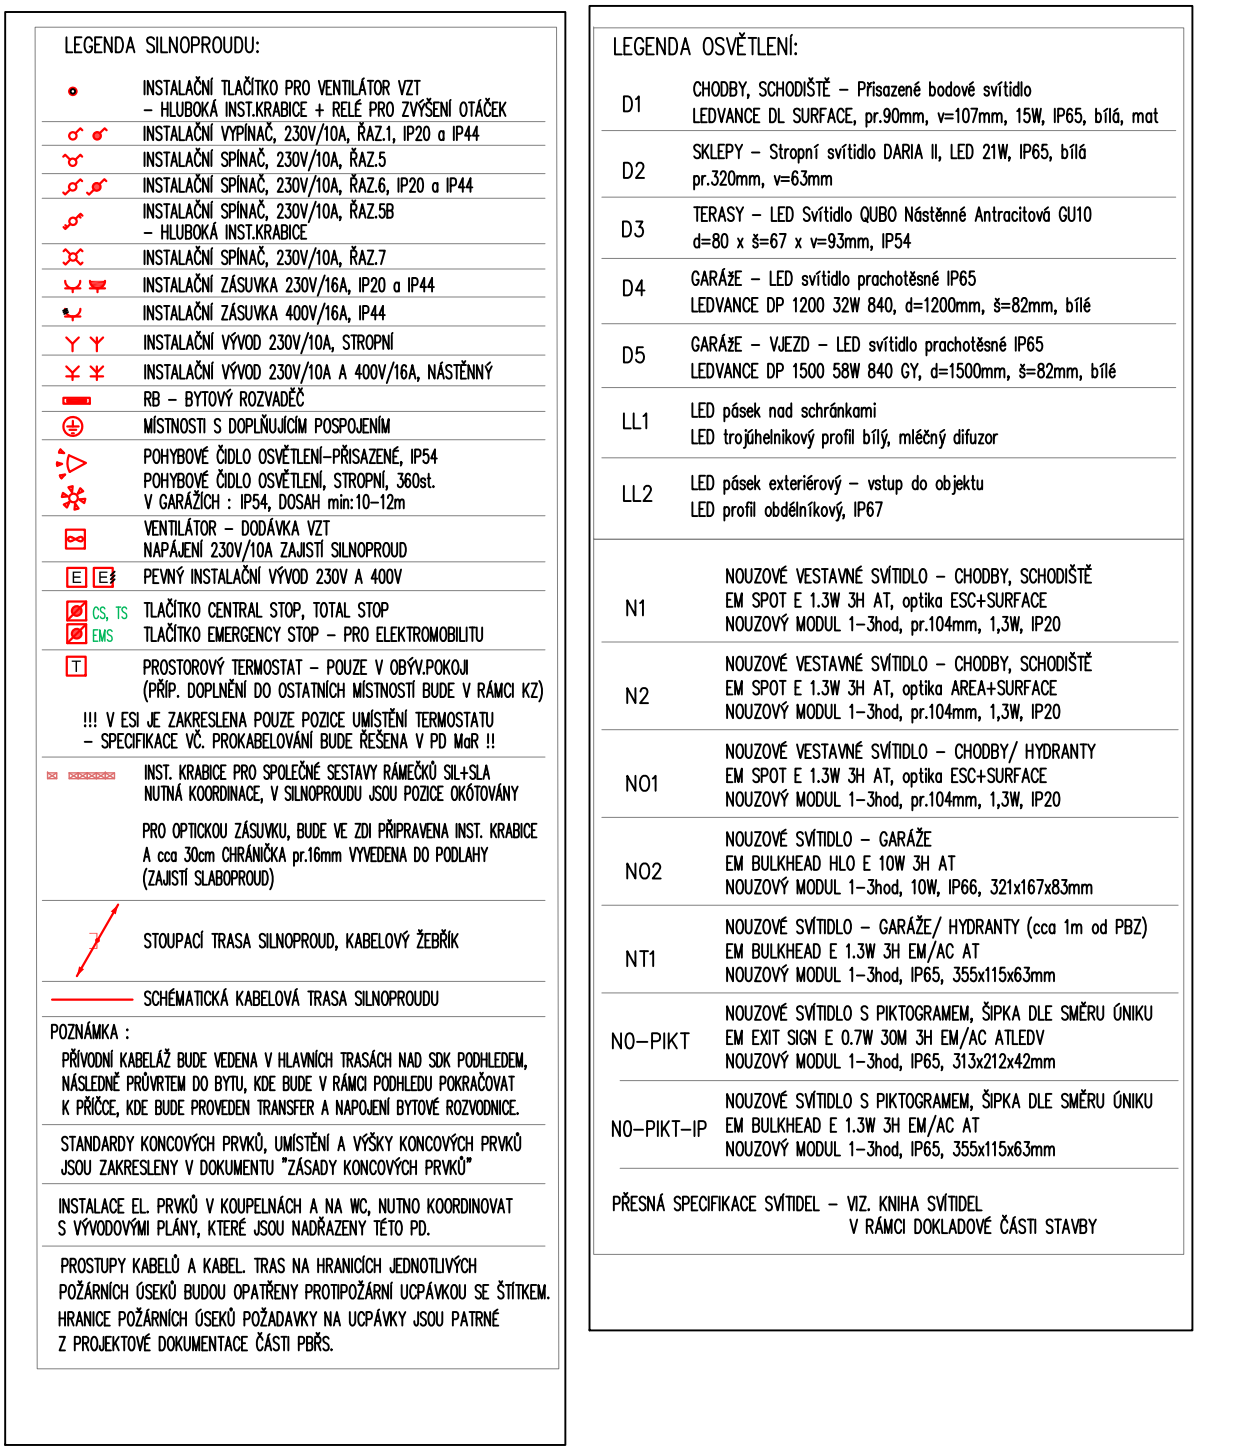

Investor DOMOPLAN a.s. Tmáň 543/16, Brno, 602 00		generální projektant BK engineering project s.r.o. Hornova 347/16 740 00 Pohoř info@bkproject.cz Hlavní inženýr projektu Ing. A. Kříž	datum 02/2026 x AA 21 m/řko	Číslo paré
--	--	---	---	------------

		Ing. Libor Doležal			1:50		
PŮDORYS 1.PP - část 2		základka	stupeň	s. objektiv	část	číslo	č. výkresu
		365	50	SO03	D.1.2	05	100B 01