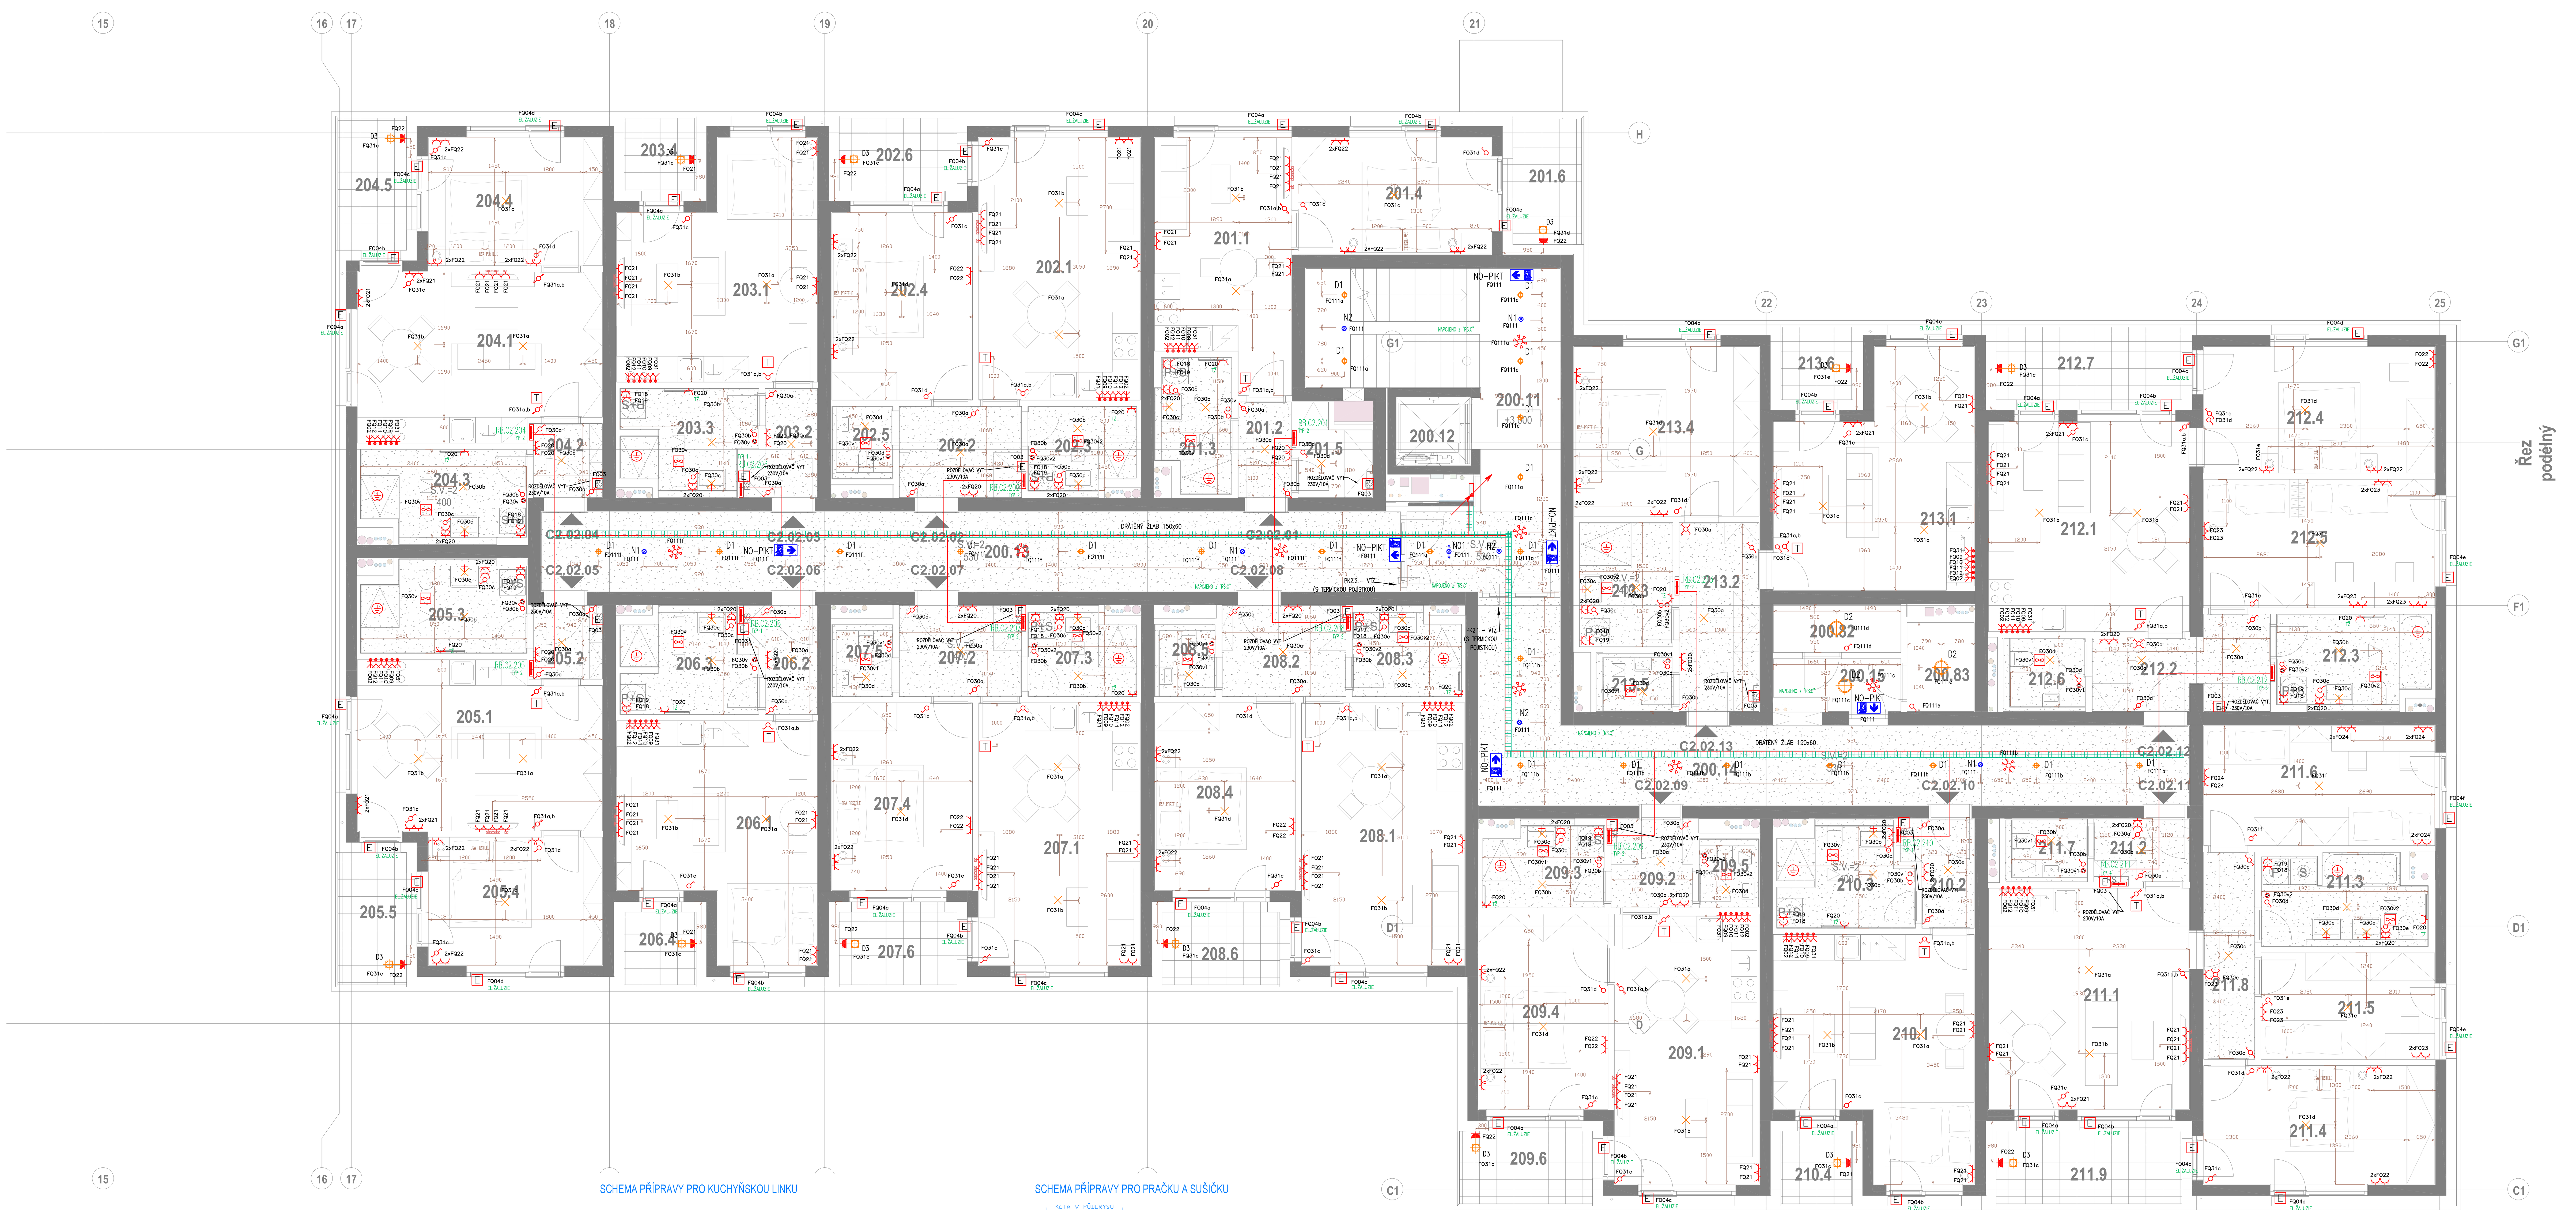

LEGENDA SILNOPROUDU:

	INSTALAČNÍ TLAČÍTKO PRO VENTILÁTOR VZT – HLUBOKÁ INST.KRABICE + RELÉ PRO ZVÝŠENÍ OTÁČEK
	INSTALAČNÍ VYPÍNAČ, 230V/10A, ŘAZ.1, IP20 a IP44
	INSTALAČNÍ SPÍNAČ, 230V/10A, ŘAZ.5
	INSTALAČNÍ SPÍNAČ, 230V/10A, ŘAZ.6, IP20 a IP44
	INSTALAČNÍ SPÍNAČ, 230V/10A, ŘAZ.5B – HLUBOKÁ INST.KRABICE
	INSTALAČNÍ SPÍNAČ, 230V/10A, ŘAZ.7
	INSTALAČNÍ ZÁSUVKA 230V/16A, IP20 a IP44
	INSTALAČNÍ ZÁSUVKA 400V/16A, IP44
	INSTALAČNÍ VÝVOD 230V/10A, STROPNÍ
	INSTALAČNÍ VÝVOD 230V/10A A 400V/16A, NÁSTĚNNÝ
	RB – BYTOVÝ ROZVADĚČ
	MÍSTNOSTI S DOPLŇUJÍCÍM POSPOJENÍM
	POHYBOVÉ ČIDLO OSVĚTLENÍ–PŘISAZENÉ, IP54 POHYBOVÉ ČIDLO OSVĚTLENÍ, STROPNÍ, 360st. V GARÁŽÍCH : IP54, DOSAH min:10–12m
	VENTILÁTOR – DODÁVKA VZT NAPÁJENÍ 230V/10A ZAJISTÍ SILNOPROUD
E	PEVNÝ INSTALAČNÍ VÝVOD 230V A 400V
CS, TS EMS	TLAČÍTKO CENTRAL STOP, TOTAL STOP TLAČÍTKO EMERGENCY STOP – PRO ELEKTROMOBILITU
T	PROSTOROVÝ TERMOSTAT – POUZE V OBÝV.POKOJI (PŘÍP. DOPLNĚNÍ DO OSTATNÍCH MÍSTNOSTÍ BUDE V RÁMCI KZ) !!! V ESI JE ZAKRESLENA POUZE POZICE UMÍSTĚNÍ TERMOSTATU – SPECIFIKACE VČ. PROKABELOVÁNÍ BUDE ŘEŠENA V PD MaR !!
	INST. KRABICE PRO SPOLEČNÉ SESTAVY RÁMEČKŮ SIL+SLA NUTNÁ KOORDINACE, V SILNOPROUDU JSOU POZICE OKÓTOVÁNY PRO OPTICKOU ZÁSUVKU, BUDE VE ZDI PŘIPRAVENA INST. KRABICE A cca 30cm CHRÁNIČKA pr.16mm VYVEDENA DO PODLAHY (ZAJISTÍ SLABOPROUD)
	STOUPACÍ TRASA SILNOPROUD, KABELOVÝ ŽEBŘÍK
	SCHÉMATICKÁ KABELOVÁ TRASA SILNOPROUDU

POZNÁMKA :

PŘÍVODNÍ KABELÁŽ BUDE VEDENA V HLAVNÍCH TRASÁCH NAD SDK PODHLEDEM, NÁSLEDNĚ PRŮVRTEM DO BYTU, KDE BUDE V RÁMCI PODHLEDU POKRAČOVAT K PŘÍČCE, KDE BUDE PROVEDEN TRANSFER A NAPOJENÍ BYTOVÉ ROZVODNICE.

STANDARDY KONCOVÝCH PRVKŮ, UMÍSTĚNÍ A VÝŠKY KONCOVÝCH PRVKŮ JSOU ZAKRESLENY V DOKUMENTU "ZÁSADY KONCOVÝCH PRVKŮ"

INSTALACE EL. PRVKŮ V KOUPELNÁCH A NA WC, NUTNO KOORDINOVAT S VÝVODOVÝMI PLÁNY, KTERÉ JSOU NADŘAZENY TÉTO PD.

PROSTUPY KABELŮ A KABEL. TRAS NA HRANICÍCH JEDNOTLIVÝCH POŽÁRNÍCH ÚSEKŮ BUDOU OPATŘENY PROTIPOŽÁRNÍ UCPÁVKOU SE ŠTÍTKEM. HRANICE POŽÁRNÍCH ÚSEKŮ POŽADAVKY NA UCPÁVKY JSOU PATRNÉ Z PROJEKTOVÉ DOKUMENTACE ČÁSTI PBŘS.

LEGENDA OSVĚTLENÍ:

D1	CHODBY, SCHODIŠTĚ – Přisazené bodové svítidlo LEDVANCE DL SURFACE, pr.90mm, v=107mm, 15W, IP65, bílá, mat
D2	SKLEPY – Stropní svítidlo DARIA II, LED 21W, IP65, bílá pr.320mm, v=63mm
D3	TERASY – LED Svítidlo QUBO Nástěnné Antracitová GU10 d=80 x š=67 x v=93mm, IP54
D4	GARÁŽE – LED svítidlo prachotěsné IP65 LEDVANCE DP 1200 32W 840, d=1200mm, š=82mm, bílé
D5	GARÁŽE – VJEZD – LED svítidlo prachotěsné IP65 LEDVANCE DP 1500 58W 840 GY, d=1500mm, š=82mm, bílé
LL1	LED pásek nad schránkami LED trojúhelnikový profil bílý, mléčný difuzor
LL2	LED pásek exteriérový – vstup do objektu LED profil obdélníkový, IP67
N1	NOUZOVÉ VESTAVNÉ SVÍTIDLO – CHODBY, SCHODIŠTĚ EM SPOT E 1.3W 3H AT, optika ESC+SURFACE NOUZOVÝ MODUL 1–3hod, pr.104mm, 1,3W, IP20
N2	NOUZOVÉ VESTAVNÉ SVÍTIDLO – CHODBY, SCHODIŠTĚ EM SPOT E 1.3W 3H AT, optika AREA+SURFACE NOUZOVÝ MODUL 1–3hod, pr.104mm, 1,3W, IP20
NO1	NOUZOVÉ VESTAVNÉ SVÍTIDLO – CHODBY/ HYDRANTY EM SPOT E 1.3W 3H AT, optika ESC+SURFACE NOUZOVÝ MODUL 1–3hod, pr.104mm, 1,3W, IP20
NO2	NOUZOVÉ SVÍTIDLO – GARÁŽE EM BULKHEAD HLO E 10W 3H AT NOUZOVÝ MODUL 1–3hod, 10W, IP66, 321x167x83mm
NT1	NOUZOVÉ SVÍTIDLO – GARÁŽE/ HYDRANTY (cca 1m od PBZ) EM BULKHEAD E 1.3W 3H EM/AC AT NOUZOVÝ MODUL 1–3hod, IP65, 355x115x63mm
NO–PIKT	NOUZOVÉ SVÍTIDLO S PIKTOGRAMEM, ŠIPKA DLE SMĚRU ÚNIKU EM EXIT SIGN E 0.7W 30M 3H EM/AC ATLEDV NOUZOVÝ MODUL 1–3hod, IP65, 313x212x42mm
NO–PIKT–IP	NOUZOVÉ SVÍTIDLO S PIKTOGRAMEM, ŠIPKA DLE SMĚRU ÚNIKU EM BULKHEAD E 1.3W 3H EM/AC AT NOUZOVÝ MODUL 1–3hod, IP65, 355x115x63mm

PŘESNÁ SPECIFIKACE SVÍTIDEL – VIZ. KNIHA SVÍTIDEL V RÁMCI DOKLADOVÉ ČÁSTI STAVBY

SCHEMA PŘÍPRAVY PRO KUCHYŇSKOU LINKU

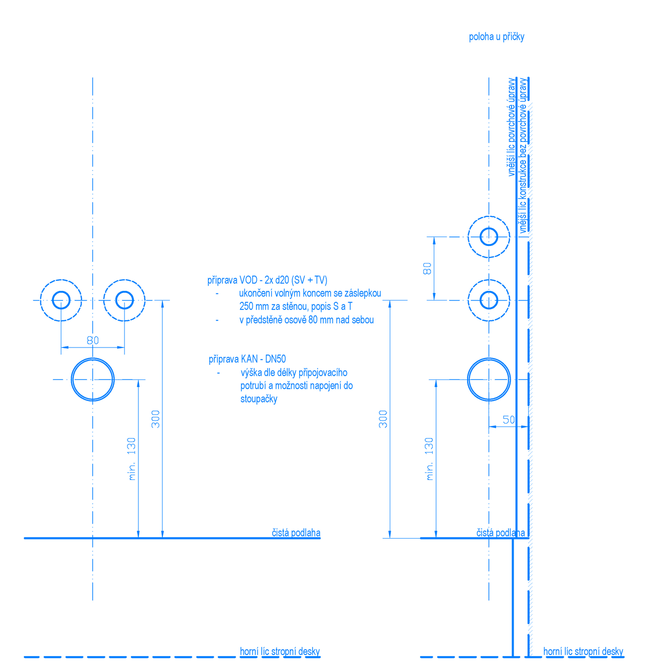

SCHEMA PŘÍPRAVY PRO PRAČKU A SUŠIČKU

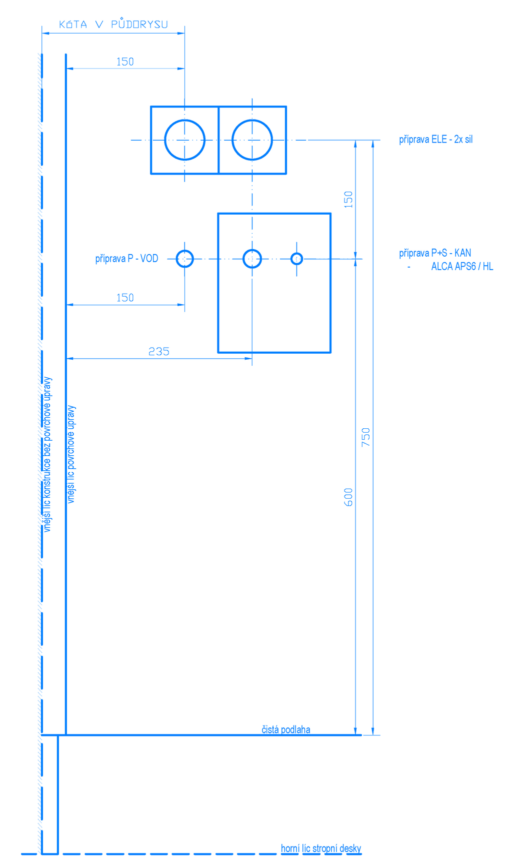

Poznámky:

Sprcha:
- sprcha ve výšce 2100 mm zarovnaná na výšku svítidla u umyvadla,
- podomítková baterie ve výšce 1000 mm
- rohový ventil pro napojení sprchy 170 mm od směšovací podomítkové baterie směrem ke stěně

V případě rozporu v půdoryse platí schéma

Revize	Popis revize	Datum

severka

± 0,000 = 224,62 m.n.m (BPV)

stavba	BD Na Mariánské cestě - 2. etapa
stupeň	Dokumentace pro provádění stavby
zpracovatel	MINET ELEKTRO, spol. s r.o. Pražská 810/16, 102 21 Praha 10 Czech Republic T: +420 281 017 259 www.minetelektro.cz
zodpovědný projektant	Ing. Jiří Pavlovský
vypracoval	Iva Židková
stavební objekt	SO03 - Bytový dům D2 a C2
část	D.1.2 Technika prostředí staveb
profesní díl / členění části	D.1.2.5 Silnoproud
investor	DOMOPLAN a.s. Trnitá 543/16, Brno, 602 00
generální projektant	BK engineering project s.r.o. Hanusova 347/16 140 00 Praha 4 info@bkproject.cz
hlavní inženýr projektu	Ing. Libor Doležal
datum	10/2025
x A4	21
měřítko	1:50
číslo paré	

PŮDORYS 2.NP - objekt C2	zakázka	stupeň	s.objekt	část	členění	č. výkresu	revize
	365	50	SO03	D.1.2	05	102B	