
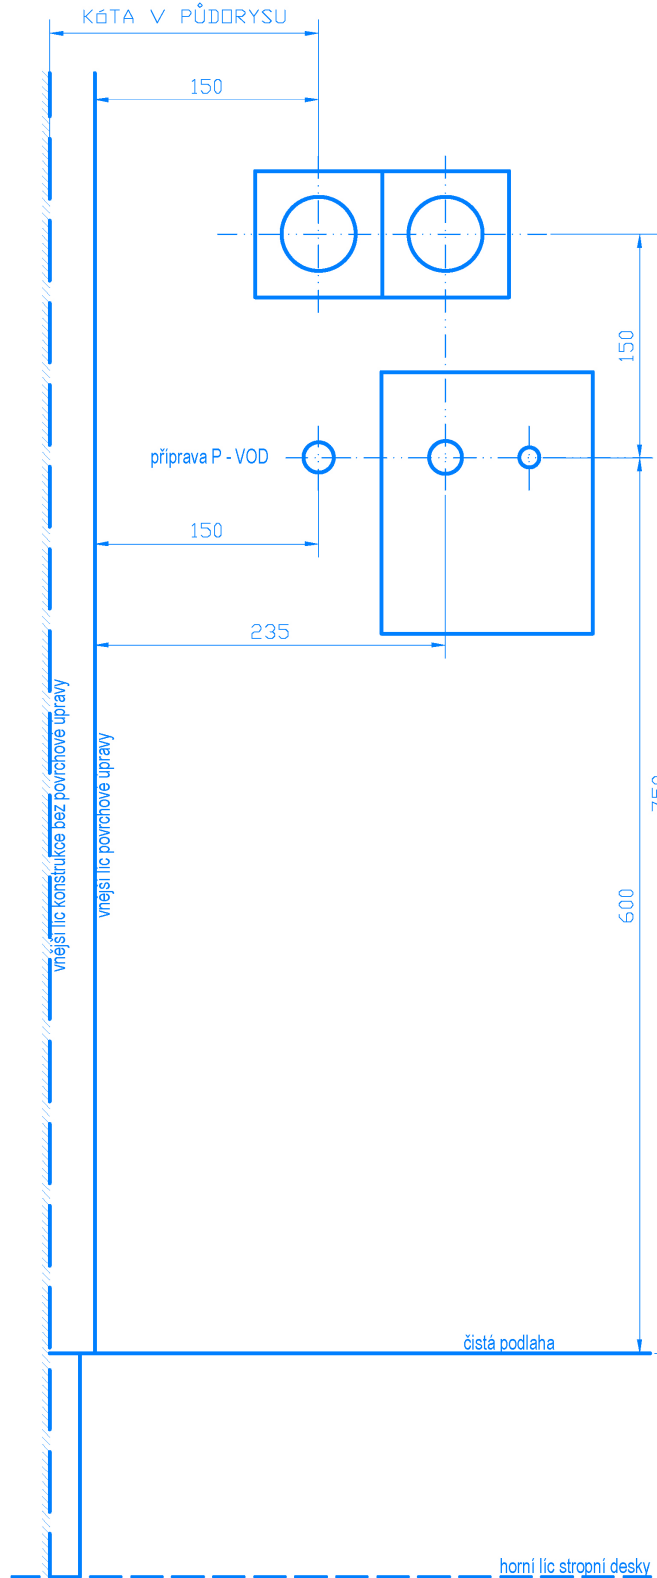


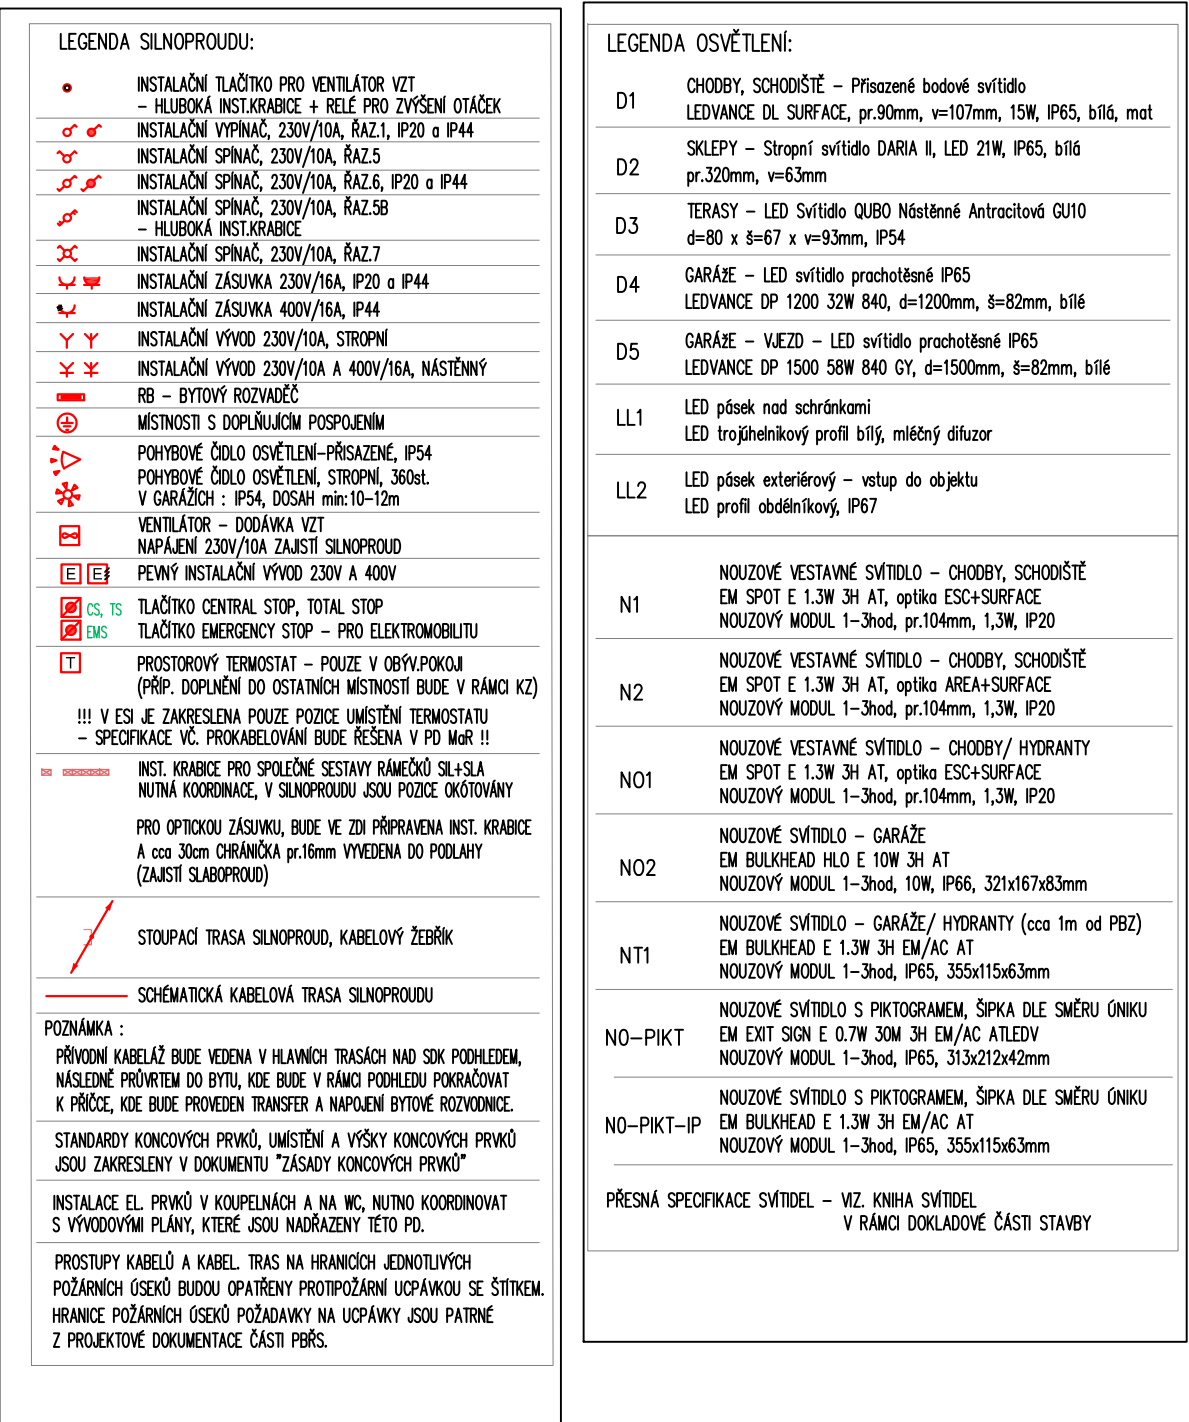

- sprcha ve výšce 2100 mm zarovnaná na výšku svítidla u umyvadla,
- podomítková baterie ve výšce 1000 mm
- rohový ventil pro napojení sprchy 170 mm od směšovací podomítkové baterie směrem ke stěně

V případě rozporu v půdoryse platí schéma

[illegible]