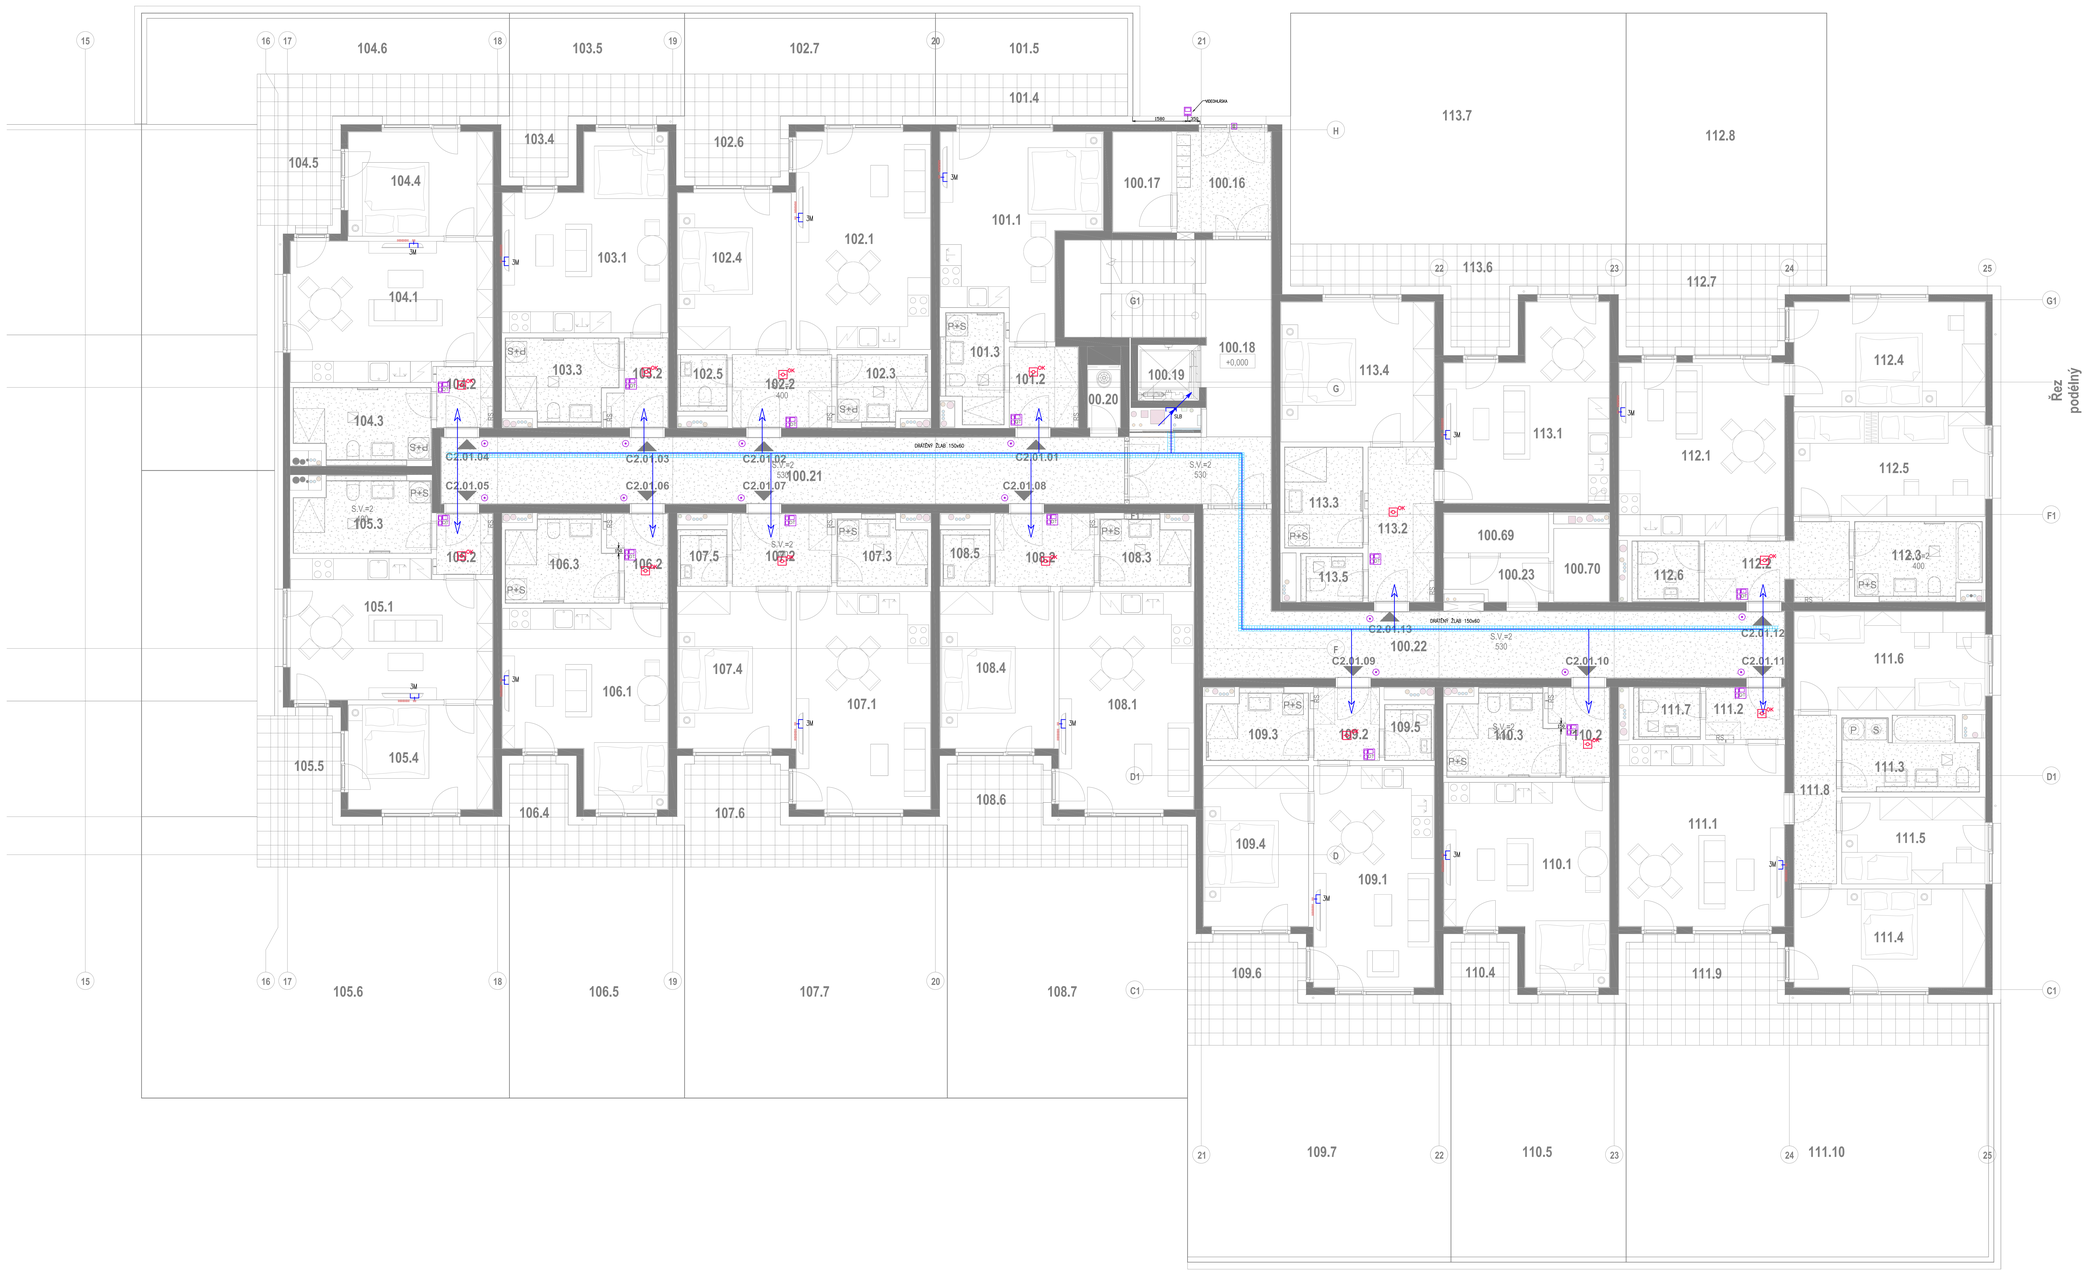

LEGENDA SLABOPROUDU:

- 3M — OPTICKÁ ZÁSUVKA V BYTĚ (UKONČENÍ OPT. KABELU)
- INST. KRABICE PRO SPOLEČNÉ SESTAVY RÁMEČKŮ SILA+SLA NUTNÁ KOORDINACE S ČÁSTÍ SILNOPROUD, KDE JSOU POZICE ZAKÓTOVANY PRO OPTICKOU ZÁSUVKU, BUDE VE ZDI PŘIPRAVENA MCI. KRABICE A cca 30cm OHÁNĚDÍ pr.16mm VYVEDENA DO PODLAHY (vyjdi SILABOPROUD)
- VNITŘNÍ JEDNOTKA INTERCOMU
- ZVONKOVÉ TLAČÍTKO
- EL.ZÁMEK DVEŘÍ (DODÁVKA STAVBY/DVEŘÍ)
- AUTONOMNÝ OPTICKO-KOUŘOVÝ HLÁSIČ - POZICI NUTNO ZKOORDINOVAT SE ŠATĚLY
- STOUPACÍ KABELOVÁ TRASA KABELOVÝ ŽEBŘÍK
- SCHÉMATICKÉ KABELOVÉ TRASY SLABOPROUDU (VEDENY NAD SDK) ZAKÓNČENÍ KABELOVÝCH TRAS V BYTĚ: - OPTICKÝ KABELÁŽ – OPTIKO PIGTAIL ZA TV (OPTICKÁ ZÁSUVKA) - KABEL CAT.6, PRO IP INTERKOM-CHODBA (PŘÍSTROJ DT)

OPTICKÁ KABELÁŽ BUDE VEDENA V HLAVNÍCH TRASÁCH NAD SDK PODHLEDEM, NÁSLEDNÉ PROVRTEM DO BYTU, KDE BUDE V RÁMCI PODHLEDU POKRAČOVAT K PŘÍSTROJI, KDE BUDE PROVEDEN TRANSFER DO PODLAHY, NÁSLEDNĚ VEDENÍ PODLAHOU DO MÍSTA OPTICKÉ ZÁSUVKY ZA TV.

POZNÁMKY:

- VEŠKERÉ INSTALACE PROCHÁZEJÍCÍ CHRÁNĚNÝMI ÚNIKOVÝMI CESTAMI BUDOU ÚNIKOVÝCH PROSTŘEDNÍM VZDUCHEM
- HRANICE POŽÁRNÍCH ÚSEKŮ A POŽADAVKY NA UCPÁVKY JSOU PATRNÉ Z PROJEKTOVÉ DOKUMENTACE ČÁSTI PBŘS
- EL.ZÁMKY HLAVNÍCH VSTUPNÍCH DVEŘÍ BUDOU DODÁVKOU STAVBY (DVEŘÍ)
- TATO DOKUMENTACE NENAHRAZUJE DODAVATELSKOU A DÍLENSKOU DOKUMENTACI

KOORDINACE:

- VEDENÍ KABELOVÝCH TRAS (VÝŠKY KABELOVÝCH TRAS ŽLABŮ/ROŠTŮ), KOLIZNÍ MÍSTA KŘÍŽENÍ A SOUSEDŮ VČE ŽLABŮ/ROŠTŮ A TAKÉ KŘÍŽENÍ A SOUSEDNÍ S TECHNOLOGICKÝMI ČÁSTMI PROFESÍ BUDE PROVEDENO DLE KOORDINAČNÍ PD, KTERÁ JE NADŘAZENA TÉTO VÝKRESOVÉ VÝŠKA A PŘESNÉ UMÍSTĚNÍ KONCOVÝCH PRVKŮ BUDE PROVEDENO DLE KOORDINAČNÍCH VÝKRESŮ A VÝKRESŮ INTERIÉRŮ.
- STANDARDY KONCOVÝCH PRVKŮ, UMÍSTĚNÍ A VÝŠKY KONCOVÝCH PRVKŮ JSOU ZAHRNUTY V DOKUMENTU "STANDARDY KONCOVÝCH PRVKŮ"

Revize	Popis revize	Datum

stavba	BD Na Mariánské cestě - 2. etapa
stupeň	Dokumentace pro provádění stavby
zpracovatel	MINET ELEKTRO, spol. s r.o., Pražská 514/16, 102 21 Praha 10 - Hostivař, Česká republika, T: +420 251 071 004, www.minetelektro.cz
zodpovědný projektant	Ing. Jiří Pavlovský
vypracoval	Iva Žižková
stavební objekt	SO03 - Bytový dům D2 a C2
část	D.1.2 Technika prostředí staveb
profesní díl / členění části	D.1.2.6 Elektronické komunikace
investor	DOMOPLAN a.s., Trnitá 543/16, Brno, 602 00
generální projektant	BK engineering project a.s., Jankovcova 1569/2c, 140 00 Praha 4, info@bkproject.cz, Hlavní inženýr projektu: Ing. Libor Dokčal
datum	10/2025
číslo paré	
v. A4	21
měřítko	1:50
PŮDORYS 1.NP - objekt C2	základka: 365 / stupeň: 50 / s.objekt: SO03 / část: D.1.2 / členění: 06 / č. výkresu: 101B / revize:

nivelace: ± 0,000 = 224,62 m.n.m (BPV)