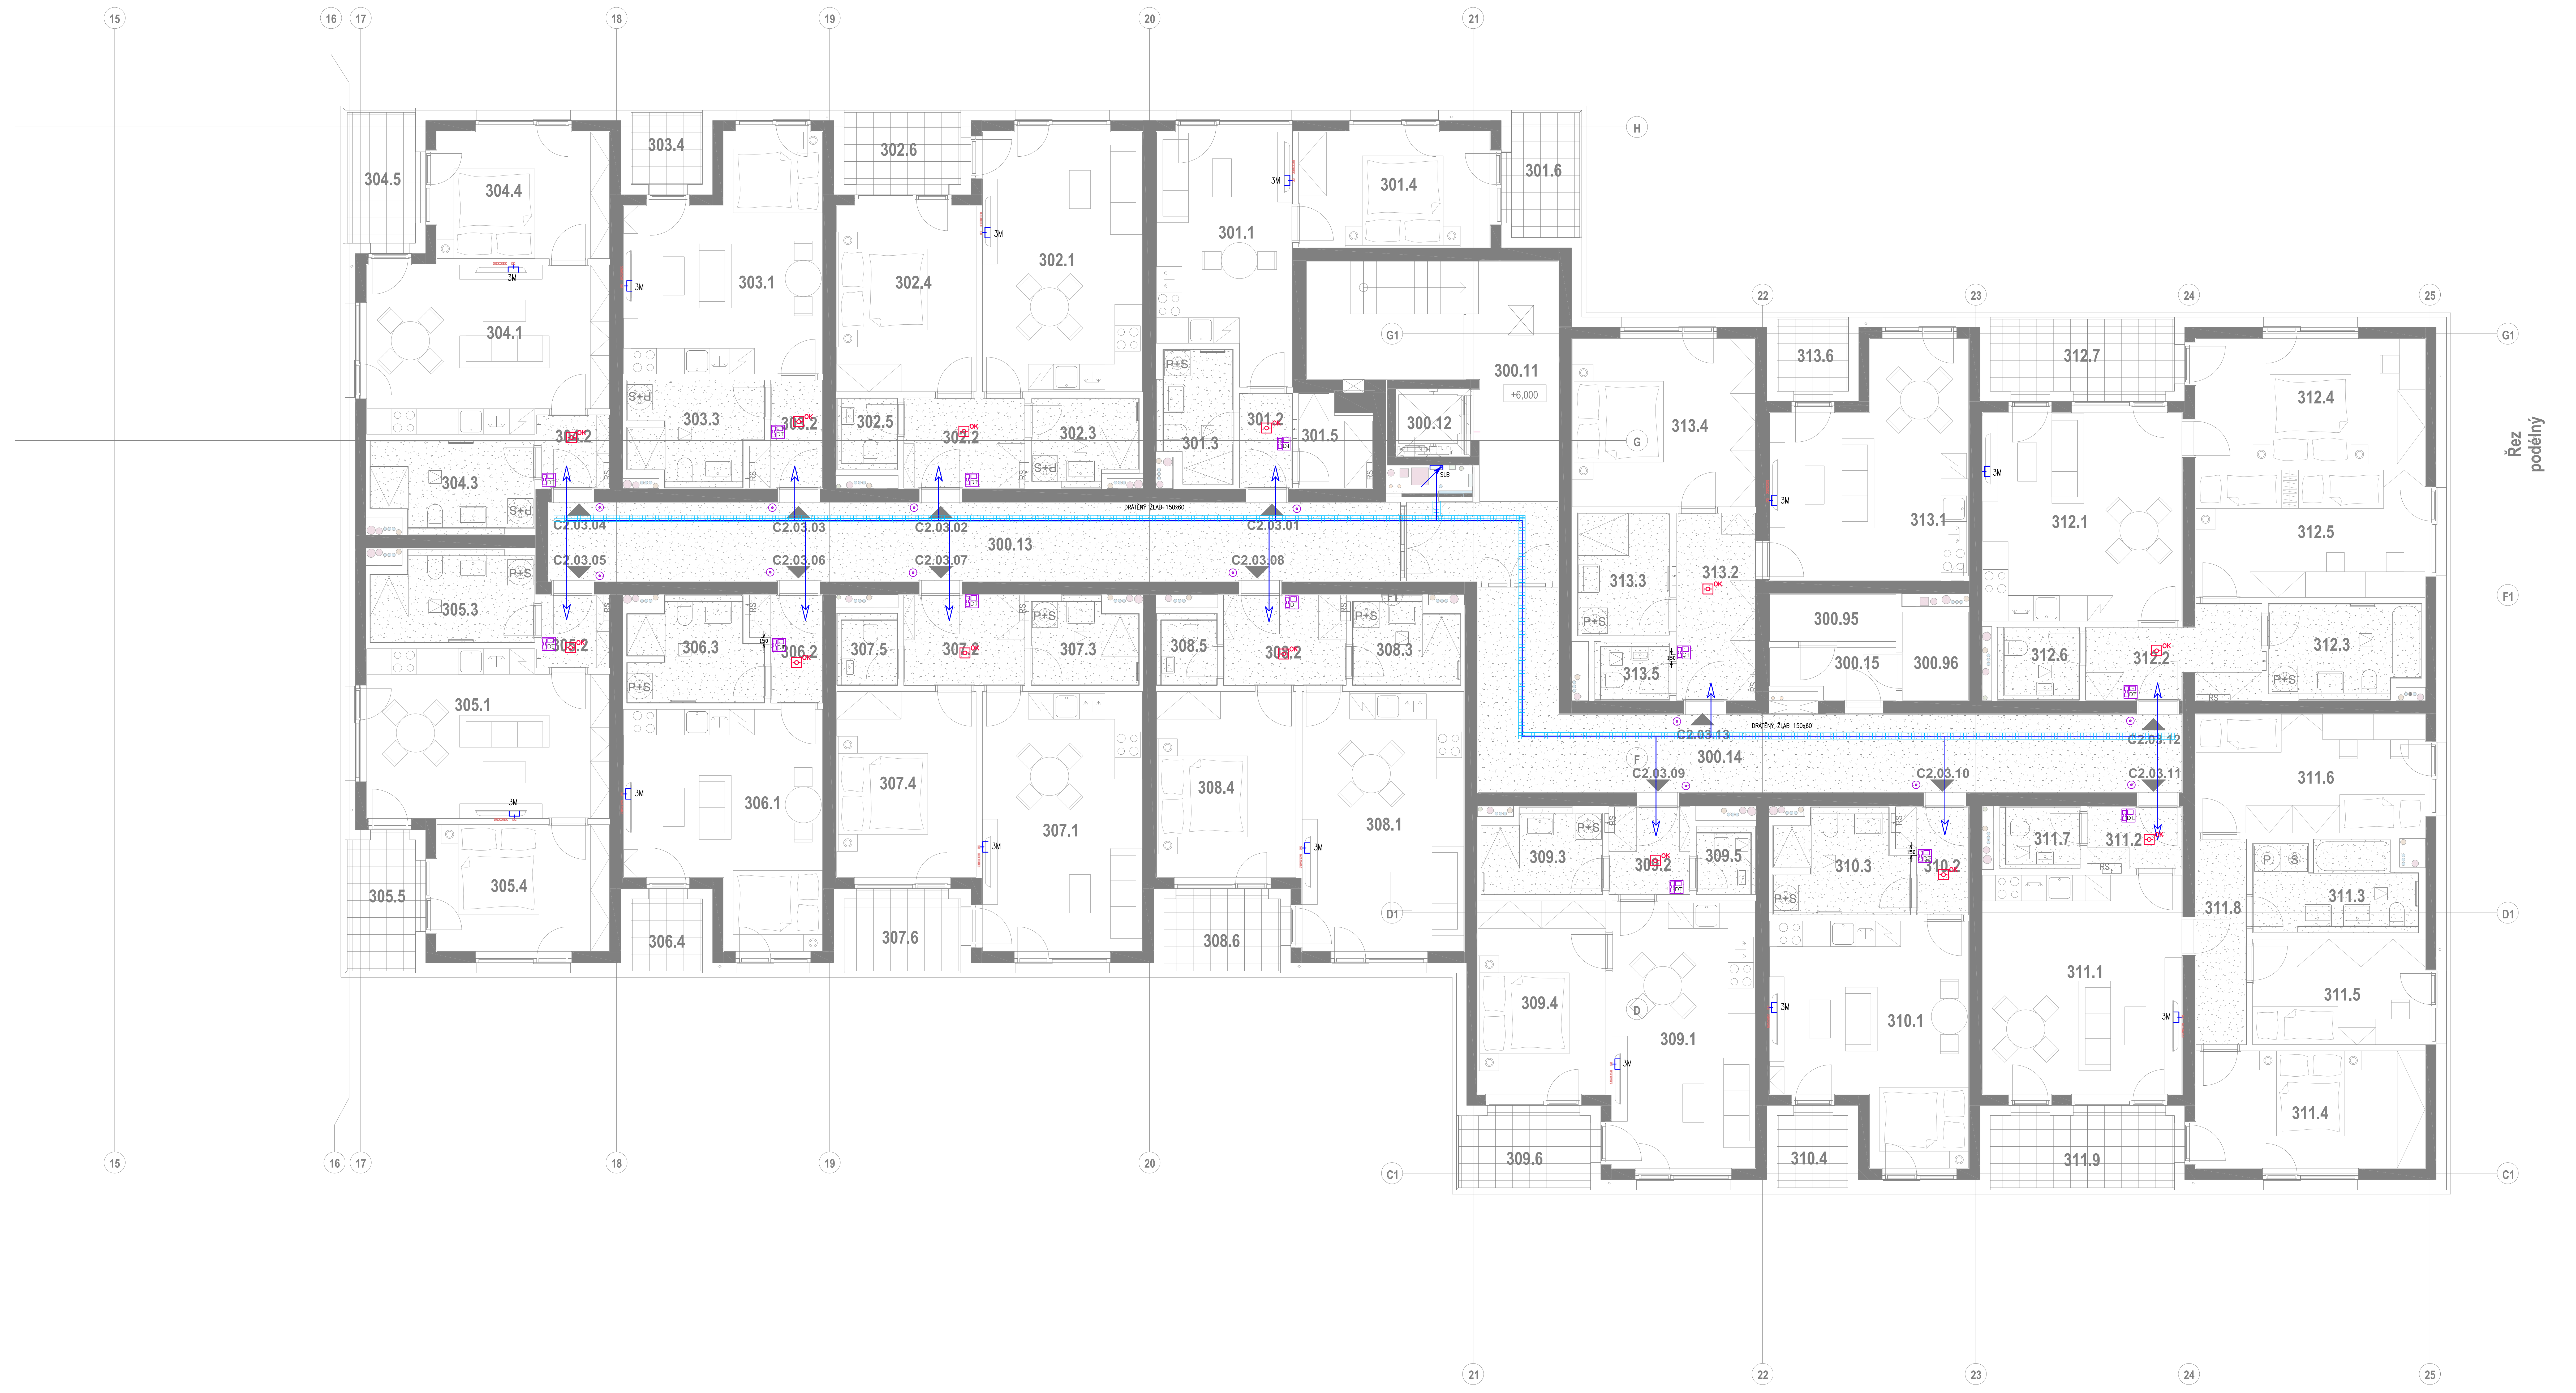

LEGENDA SLABOPROUDU:

⊏ 3M	OPTICKÁ ZÁSUVKA V BYTĚ (UKONČENÍ OPT. KABELU)
▨▨▨ ▨	INST. KRABICE PRO SPOLEČNÉ SESTAVY RÁMEČKŮ SIL+SLA NUTNÁ KOORDINACE S ČÁSTI SILNOPROUD, KDE JSOU POZICE OKÓTOVÁNY PRO OPTICKOU ZÁSUVKU, BUDE VE ZDI PŘIPRAVENA INST. KRABICE A cca 30cm CHRÁNIČKA pr.16mm VYVEDENA DO PODLAHY (zajistí SLABOPROUD)
DT	VNITŘNÍ JEDNOTKA INTERCOMU
⊙	ZVONKOVÉ TLAČÍTKO
▯	EL.ZÁMEK DVEŘÍ (DODÁVKA STAVBY/DVEŘÍ)
OK	AUTONOMNÍ OPTICKO-KOUŘOVÝ HLÁSIČ -POZICI NUTNO ZKOORDINOVAT SE SVÍTIDLY
↗	STOUPACÍ KABELOVÁ TRASA KABELOVÝ ŽEBŘÍK
→	SCHÉMATICKÉ KABELOVÉ TRASY SLABOPROUDU (VEDENY NAD SDK) ZAKONČENÍ KABELOVÝCH TRAS V BYTĚ: -OPTICKÁ KABELÁŽ – OBÝVACÍ POKOJ, ZA TV (OPTICKÁ ZÁSUVKA) -KABEL CAT.6, PRO IP INTERKOM-CHODBA (PŘÍSTROJ DT)

OPTICKÁ KABELÁŽ BUDE VEDENA V HLAVNÍCH TRASÁCH NAD SDK PODHLEDEM, NÁSLEDNĚ PRŮVRTEM DO BYTU, KDE BUDE V RÁMCI PODHLEDU POKRAČOVAT K PŘÍČCE, KDE BUDE PROVEDEN TRANSFER DO PODLAHY, NÁSLEDNÉ VEDENÍ PODLAHOU DO MÍSTA OPTICKÉ ZÁSUVKY ZA TV.

POZNÁMKY:

- VEŠKERÉ INSTALACE PROCHÁZEJÍCÍ CHRÁNĚNÝMI ÚNIKOVÝMI CESTAMI BUDOU OPATŘENY PROTIPOŽÁRNÍ IZOLACÍ
- HRANICE POŽÁRNÍCH ÚSEKŮ A POŽADAVKY NA UCPÁVKY JSOU PATRNÉ Z PROJEKTOVÉ DOKUMENTACE ČÁSTI PBŘS
- EL.ZÁMKY HLAVNÍCH VSTUPNÍCH DVEŘÍ BUDOU DODÁVKOU STAVBY (DVEŘÍ)
- TATO DOKUMENTACE NENAHRAZUJE DODAVATELSKOU A DÍLENSKOU DOKUMENTACI

KOORDINACE:

- VEDENÍ KABELOVÝCH TRAS (VÝŠKY KABELOVÝCH TRAS ŽLABŮ/ROŠTŮ, KOLIZNÍ MÍSTA KŘÍŽENÍ A SOUBĚHŮ VÍCE ŽLABŮ/ROŠTŮ A TAKÉ KŘÍŽENÍ A SOUBĚHY S TECHNOLOGIEMI OSTATNÍCH PROFESÍ BUDE PROVEDENO DLE KOORDINAČNÍ PD, KTERÁ JE NADŘAZENA TĚMTO VÝKRESŮM VÝŠKA A PŘESNÉ UMÍSTĚNÍ KONCOVÝCH PRVKŮ BUDE PROVEDENO DLE KOORDINAČNÍCH VÝKRESŮ A VÝKRESŮ INTERIÉRŮ.
- STANDARDY KONCOVÝCH PRVKŮ, UMÍSTĚNÍ A VÝŠKY KONCOVÝCH PRVKŮ JSOU ZAKRESLENY V DOKUMENTU "ZÁSADY KONCOVÝCH PRVKŮ"

Revize	Popis revize	Datum

severka

± 0,000 = 224,62 m.n.m (BPV)

stavba
BD Na Mariánské cestě - 2. etapa

stupeň
Dokumentace pro provádění stavby

zpracovatel
MINET ELEKTRO, spol. s r.o.
Pražská 810/16, 102 21 Praha 10
Czech Republic
T: +420 281 017 259
www.minetelektro.cz

zodpovědný projektant
Ing. Jiří Pavlovský

vypracoval
Iva Židková

stavební objekt
SO03 - Bytový dům D2 a C2

část
D.1.2 Technika prostředí staveb

profesní díl / členění části
D.1.2.6 Elektronické komunikace

investor
DOMOPLAN a.s.
Trnitá 543/16, Brno, 602 00

generální projektant
BK engineering project s.r.o.
Hanusova 347/16
140 00 Praha 4
info@bkproject.cz

hlavní inženýr projektu
Ing. Libor Doležal

datum 10/2025

x A4 21

měřítko 1:50

číslo paré

	zakázka	stupeň	s.objekt	část	členění	č. výkresu	revize
PŮDORYS 3.NP - objekt C2	365	50	SO03	D.1.2	06	103B	