ŘEZ PŘÍČNÝ
ŘEZ PODÉLNÝ
MR-V03.1
ROZVÁDĚČ MĚŘENÍ A REGULACE
PŘÍKON ROZVÁDĚČE: Pi = 9kW
PŘÍVOD A VÝVODY: HOREM
ROZMĚRY SKŘÍNĚ: 800 x 1200 x 210 mm
KRYTÍ SKŘÍNĚ: IP65 / IP20
MR-K03
ROZVÁDĚČ MĚŘENÍ A REGULACE
PŘÍKON ROZVÁDĚČE: Pi = 15kW
PŘÍVOD A VÝVODY: HOREM
ROZMĚRY SKŘÍNĚ: 800 x 1200 x 210 mm
KRYTÍ SKŘÍNĚ: IP65 / IP20
MR-V03.2
ROZVÁDĚČ MĚŘENÍ A REGULACE
PŘÍKON ROZVÁDĚČE: Pi = 7kW
PŘÍVOD A VÝVODY: HOREM
ROZMĚRY SKŘÍNĚ: 800 x 1200 x 210 mm
KRYTÍ SKŘÍNĚ: IP65 / IP20
EOH01.1
E1.3
Logamatic 5313
SF01.1
ČIDLO VENKOVNÍ TEPLOTY
Instalace v úrovní 1.NP ve výšce 3m nad terénem
K2
K1
BDS
E1.2
E1.1
E2
MT1
MT2, T3
TV1
SB1, SY1
PK01.2
PK01.3
E1.3
HUP
EF01.6
EF01.8
PK01.4
KO-01.2
EF01.2
CO-1.1
CO-1.2
CO-1.3
CO-1.4
CO-2.1
CO-2.2
CO-2.3
CO-3.1
CO-3.2
CO-3.3
CO-3.4
ČIDLO CO
Instalace ve výšce 1,6m nad čistou podlahou
JYTY-O 4x1
EF01.7
PK01.5
EF01.3
KO-01.3
PK01.6
EF01.5
EF01.9
EF01.1
KO-01.1
PK01.1
EF01.4
POZOR-CO
TAB-9.1
TAB-9.2
TAB-9.3
H1
000.1
000.2
000.3
000.4
000.5
000.6
000.7
000.8
000.9
000.10
000.11
000.13
000.14
000.15
S.V.=2 440
S.V.=2 510
Požární roleta

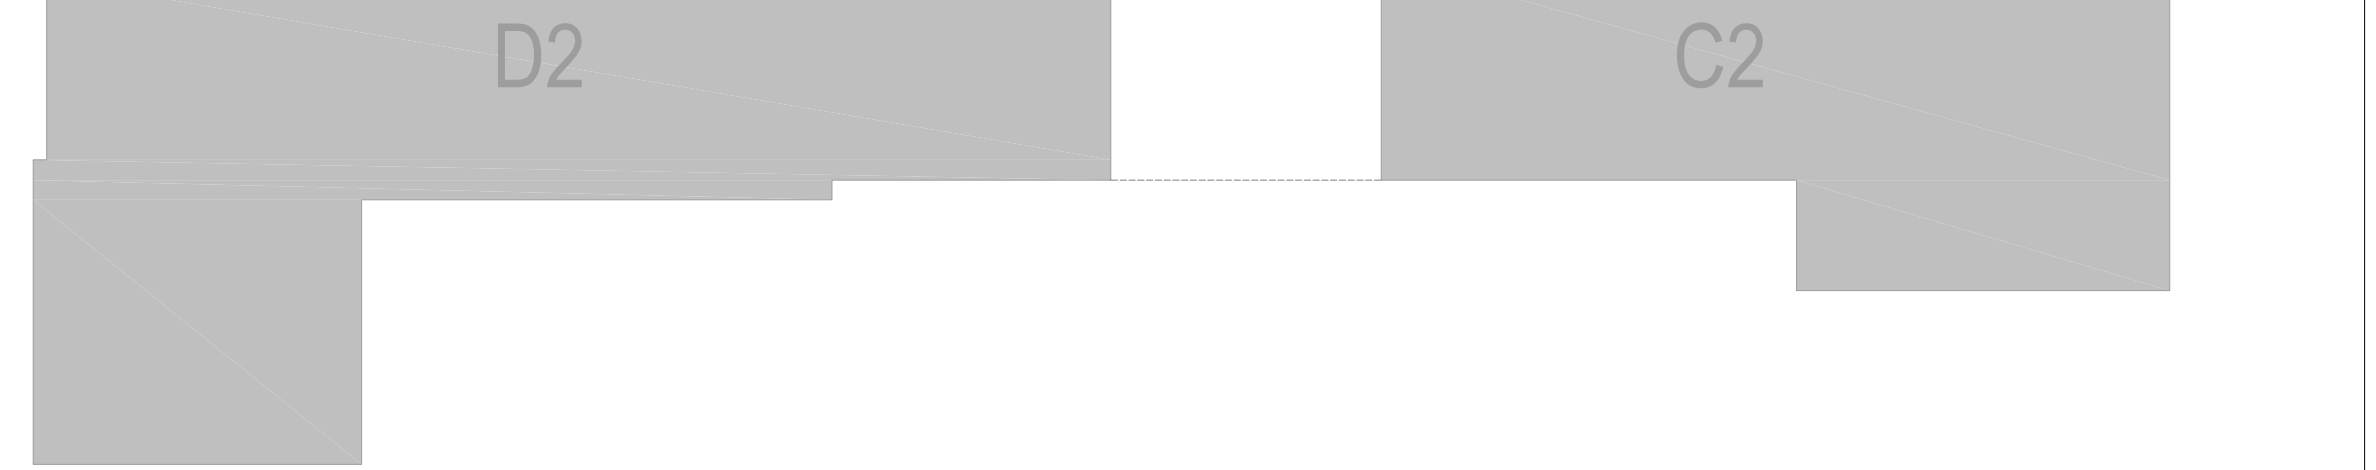

Místnosti 1.PP		
Číslo	Název	Plocha
001	Sklep	5,35 m²
002	Sklep	3,44 m²
003	Sklep	3,51 m²
004	Sklep	3,44 m²
005	Sklep	3,44 m²
006	Sklep	3,44 m²
007	Sklep	4,76 m²
008	Sklep	1,92 m²
009	Sklep	2,50 m²
010	Sklep	2,50 m²
011	Sklep	2,50 m²
012	Sklep	2,55 m²
013	Sklep	2,50 m²
014	Sklep	10,64 m²
015	Sklep	2,90 m²
016	Sklep	2,50 m²
017	Sklep	2,50 m²
018	Sklep	2,55 m²
019	Sklep	2,44 m²
020	Sklep	7,61 m²
021	Sklep	6,51 m²
022	Sklep	6,51 m²
023	Sklep	5,88 m²
024	Sklep	5,88 m²
025	Sklep	5,88 m²
026	Sklep	5,88 m²
027	Sklep	5,88 m²
028	Sklep	6,00 m²
029	Sklep	5,88 m²
030	Sklep	8,38 m²
		135,64 m²
000.1	Schodiště	21,16 m²
000.2	Schodiště	13,26 m²
000.4	Výtah	2,80 m²
000.5	Výtah	2,80 m²
000.7	Hromadné garáže	739,60 m²
000.8	Hromadné garáže	622,98 m²
		1 402,59 m²
000.8	Elektro	3,87 m²
000.11	Technická místnost	15,34 m²
000.12	Kotelna	16,56 m²
000.13	Elektro	6,68 m²
000.14	Elektro	3,14 m²
000.18	Elektro	2,93 m²
		48,53 m²
D2.00.00 - Společné prostory		1 586,77 m²

Místnosti 1.PP		
Číslo	Název	Plocha
031	Sklep	5,97 m²
032	Sklep	5,45 m²
033	Sklep	5,84 m²
034	Sklep	6,00 m²
035	Sklep	5,91 m²
036	Sklep	5,84 m²
037	Sklep	5,91 m²
038	Sklep	7,12 m²
039	Sklep	7,19 m²
040	Sklep	6,51 m²
041	Sklep	6,51 m²
042	Sklep	7,61 m²
043	Sklep	4,25 m²
044	Sklep	4,09 m²
045	Sklep	3,01 m²
046	Sklep	3,01 m²
047	Sklep	3,01 m²
048	Sklep	3,01 m²
049	Sklep	3,01 m²
050	Sklep	3,83 m²
051	Sklep	3,89 m²
052	Sklep	3,06 m²
053	Sklep	3,06 m²
054	Sklep	3,06 m²
055	Sklep	3,06 m²
056	Sklep	3,06 m²
057	Sklep	2,66 m²
058	Sklep	2,87 m²
		127,83 m²
000.3	Schodiště	19,56 m²
000.6	Výtah	2,80 m²
000.9	Hromadné garáže	357,33 m²
000.10	Hromadné garáže	549,32 m²
000.15	Kočárkárna	12,90 m²
		941,91 m²
000.16	Elektro	2,75 m²
		2,75 m²
C2.00.00 - Společné prostory		1 072,50 m²
C2		1 072,50 m²

LEGENDA

MR-.. ... ROZVÁDĚČ MĚŘENÍ A REGULACE
M ... VÝVOD PRO ELEKTRICKÝ MOTOR (VENTILÁTOR)
S ... VÝVOD PRO EL.POHON VZD. KLAPKY
CO ... ČIDLO DEKCE CO V GARÁŽÍCH
(montáž v nádechové výšce 1,5m nad čistou podlahou)
T ... ČIDLO TEPLOTY V PROSTORU
Montáž do výšky 1500mm nad čistou podlahou
◣ ... POŽÁRNÍ KLAPKA
MaR POŽÁRNÍ KLAPKY MONITORUJE (OTV/ZAV)
– OVLÁDÁ EPS (NAPÁJÍ ESI)

POZOR-CO ... VÝSTRAŽNÁ SVĚTELNÁ TABULE – GARÁŽE
TAB-9.1 ... ZÁKAZ VJEZDU – NEBEZPEČÍ OTRAVY
TAB-9.2 ... ZÁKAZ VSTUPU – NEBEZPEČÍ OTRAVY
TAB-9.3 ... VYPNĚTE MOTOR, OPUSŤTE GARÁŽ
H1 ... SIRÉNA 230V AC – GARÁŽE

QT.... CALORIMETR TEPLO - M-BUS
SV.... VODOMĚR STUDENÁ VODA - M-BUS
TV.... VODOMĚR TEPLÁ VODA - M-BUS
EM.... ELEKTROMĚR - M-BUS

POZNÁMKY OBECNÉ

1. Tato dokumentace je vypracována v rozsahu pro provedení stavby a nenahrazuje dokumentaci dílenskou – dodavatelskou, kterou si vypracuje budoucí dodavatel.
2. Veškeré návaznosti na jiné profese musí být ověřeny před zpracováním dílenské dokumentace stavby.
3. Je-li v dokumentaci definován konkrétní výrobek (výrobky) nebo technologie, má se za to, že je tím definován minimální požadovaný standard a v nabídce/dodávce může být nahrazen i výrobkem nebo technologií srovnatelnou. Nedodržení této podmínky vylučuje tvůrce této pd z následných řešení technických nesrovnalostí či problémů. Nahraditel si musí být plně vědom, že náhrada/-y je/jsou prováděny jen a pouze na jeho odpovědnost.
4. Nutno dodržet bezpečnostní odstup signálních a datových vodičů od rozvodů silových a to ve vzdálenosti alespoň 15-20cm nebo použít plechové kabelové kanály se stíněnými dělícími přepážkami.
5. Dle ČSN je nutné veškerá instalovaná zařízení vodivě pospojit zelenožlutým vodičem o minimálním průřezu 6mm2 (doporučuji realizaci koordinovat s dodavateli VZT a ELE pro určení hranic dodávek, neboť i tyto profese mají některá zařízení vodivě pospojovat).
6. Před uvedením do provozu je nutné provést výchozí revizi elektroinstalace, bez které není možné zařízení provozovat.
7. Prostupy kabelů požárně dělícími konstrukcemi požárně utěsnit – požární odolnost příslušné stavební konstrukce viz. technická zpráva PBŘS.

ZÁKLADNÍ ELEKTROTECHNICKÉ POŽADAVKY NA ROZVÁDĚČE ...
NAP. SOUSTAVA: (dle konkrétního rozváděče)
OVL. SOUSTAVA: 1+N+PE / AC 230V, 50Hz / TN-S
AC/DC 24V SELV

OCHRANA PŘED ÚRAZEM EL. PROUDEM DLE ČSN 33 2000-4-41 ed. 2 Z1 :
OCHRANA ŽIVÝCH ČÁSTÍ : – KRYTÍM
– IZOLACÍ

OCHRANA NEŽIVÝCH ČÁSTÍ : – SAMOČINNÝM ODPOJENÍM OD ZDROJE
– DVOJITOU IZOLACÍ
– MALÝM BEZPEČNÝM NAPĚTÍM SELV

Revize	Popis revize	Datum
01	Aktualizace půdorysu 1PP, koordinace	02/2026

severka
± 0,000 = 224,62 m.n.m (BPV)

stavba
BD Na Mariánské cestě - 2. etapa
stupeň
Dokumentace pro provádění stavby

zpracovatel
MINET ELEKTRO, spol. s r.o.
Pražská 810/16, 102 21 Praha 10
Czech Republic
T: +420 281 017 259
www.minetelektro.cz

zodpovědný projektant
Ing. Jiří Pavlovský
vypracoval
Radek Hak

stavební objekt
SO03 - Bytový dům D2 a C2
část
D.1.2 Technika prostředí staveb
profesní díl / členění části
D.1.2.8 Měření a regulace

investor
DOMOPLAN a.s.
Trnitá 543/16, Brno, 602 00

generální projektant
BK engineering project s.r.o.
Hanusova 347/16
140 00 Praha 4
info@bkproject.cz
hlavní inženýr projektu
Ing. Libor Doležal

datum 02/2026
x A4 45
měřítko 1:50
číslo paré

PŮDORYS 1.PP

zakázka	stupeň	s.objekt	část	členění	č. výkresu	revize
365	50	SO03	D.1.2	08	100	01