


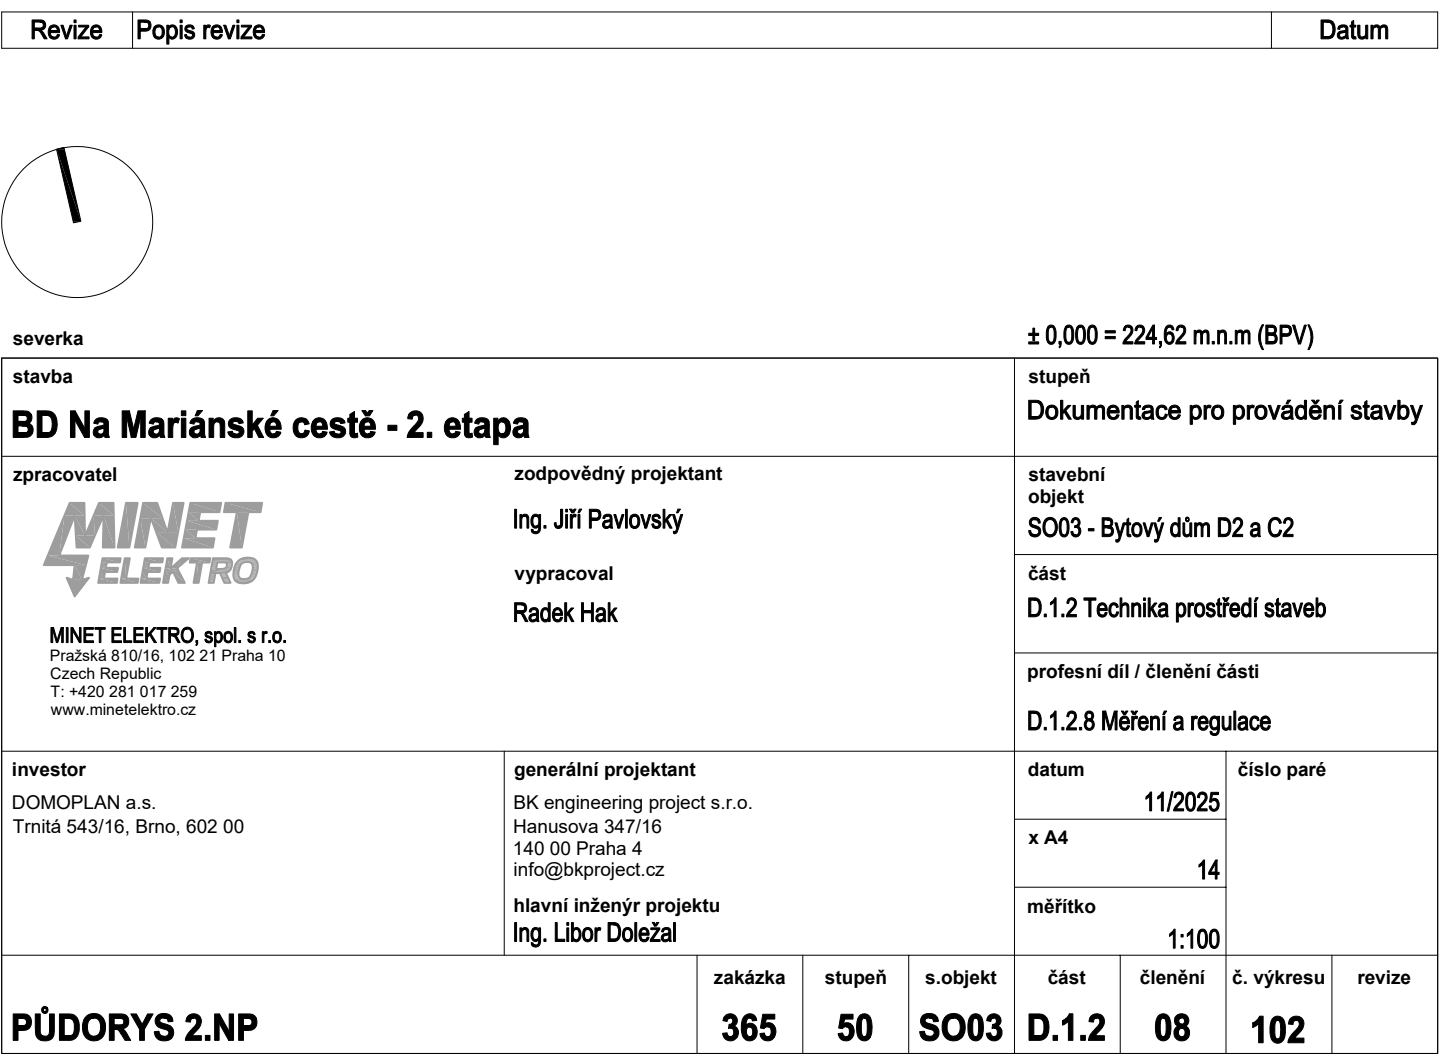

1. Tato dokumentace je vypracována v rozsahu pro provedení stavby a nenahrazuje dokumentaci výkresovou - dodavatelskou, kterou si vypracuje zadavatel dle požadavků.	NAP. SOUSTAVA: (dle konkrétního rozvaděče) OVL. SOUSTAVA: TN-SPE / AC 230V, 50Hz / TN-S AC/DC 24V SELV
2. Veškeré návaznosti na jiné profese musí být ověřeny před zaprosáním dílenské dokumentace stavby.	OHRAŇNÁ PŘED ÚRAZEM EL. PROUDEM DLE ČSN 33 2000-4.41 ed. 2 Z1 OHRAŇNÁ ŽIVÝCH ČÁSTÍ: - KRYTÍM - IZOLACÍ
3. Je-li v dokumentaci definován konkrétní výrobek (výrobky) nebo technologie, na to je, že to je, že to je, že to je definován minimální požadovaný standard a v nádobě/dodávce může být nahrazen i výrobek nebo technologie srovnatelnou. Nedožržel to podmínky výroby tvůrce této před z následných řešení technických nesvatostí i při řešení. Nahradit si musí být plně vědom, že nahradí-/y je/ jsou prováděny jen a pouze na jeho odpovědnost.	OHRAŇNÁ NEŽIVÝCH ČÁSTÍ: - SAMOČINNÝM ODPOJENÍM OD ZDRAVOTNÍHO - DVOJITOU IZOLACÍ - MALÝM BEZPEČNÝM NAPĚTÍM SELV
4. Nutno dožít bezpečnostní odstup signálních a datových vodičů od rozvodů silových a to ve vzdálenosti alespoň 15-20cm nebo použití pletchové kabelové kanály se stíněnými dělicími přepážkami.	
5. Die ČSN je nutné instalovat vstavená zařízení vodě odolnost potrubí zateplených vodičů o minimálním průřezu 6mm² (doporučí realizaci koordinovat s dodavateli VZT a ELE pro určení hranic dodávky, neboť i tyto profese mají některá zařízení vodě odolnost).	
6. Před uvedením do provozu je nutné provést výchozí revizi elektronizace, bez které není možné zařízení provozovat.	
7. Průběhy kabelů požární odolnosti konstrukcí požární odolnosti - požární odolnost příslušné stavební konstrukce viz. technická zpráva PŘBŠ.	