


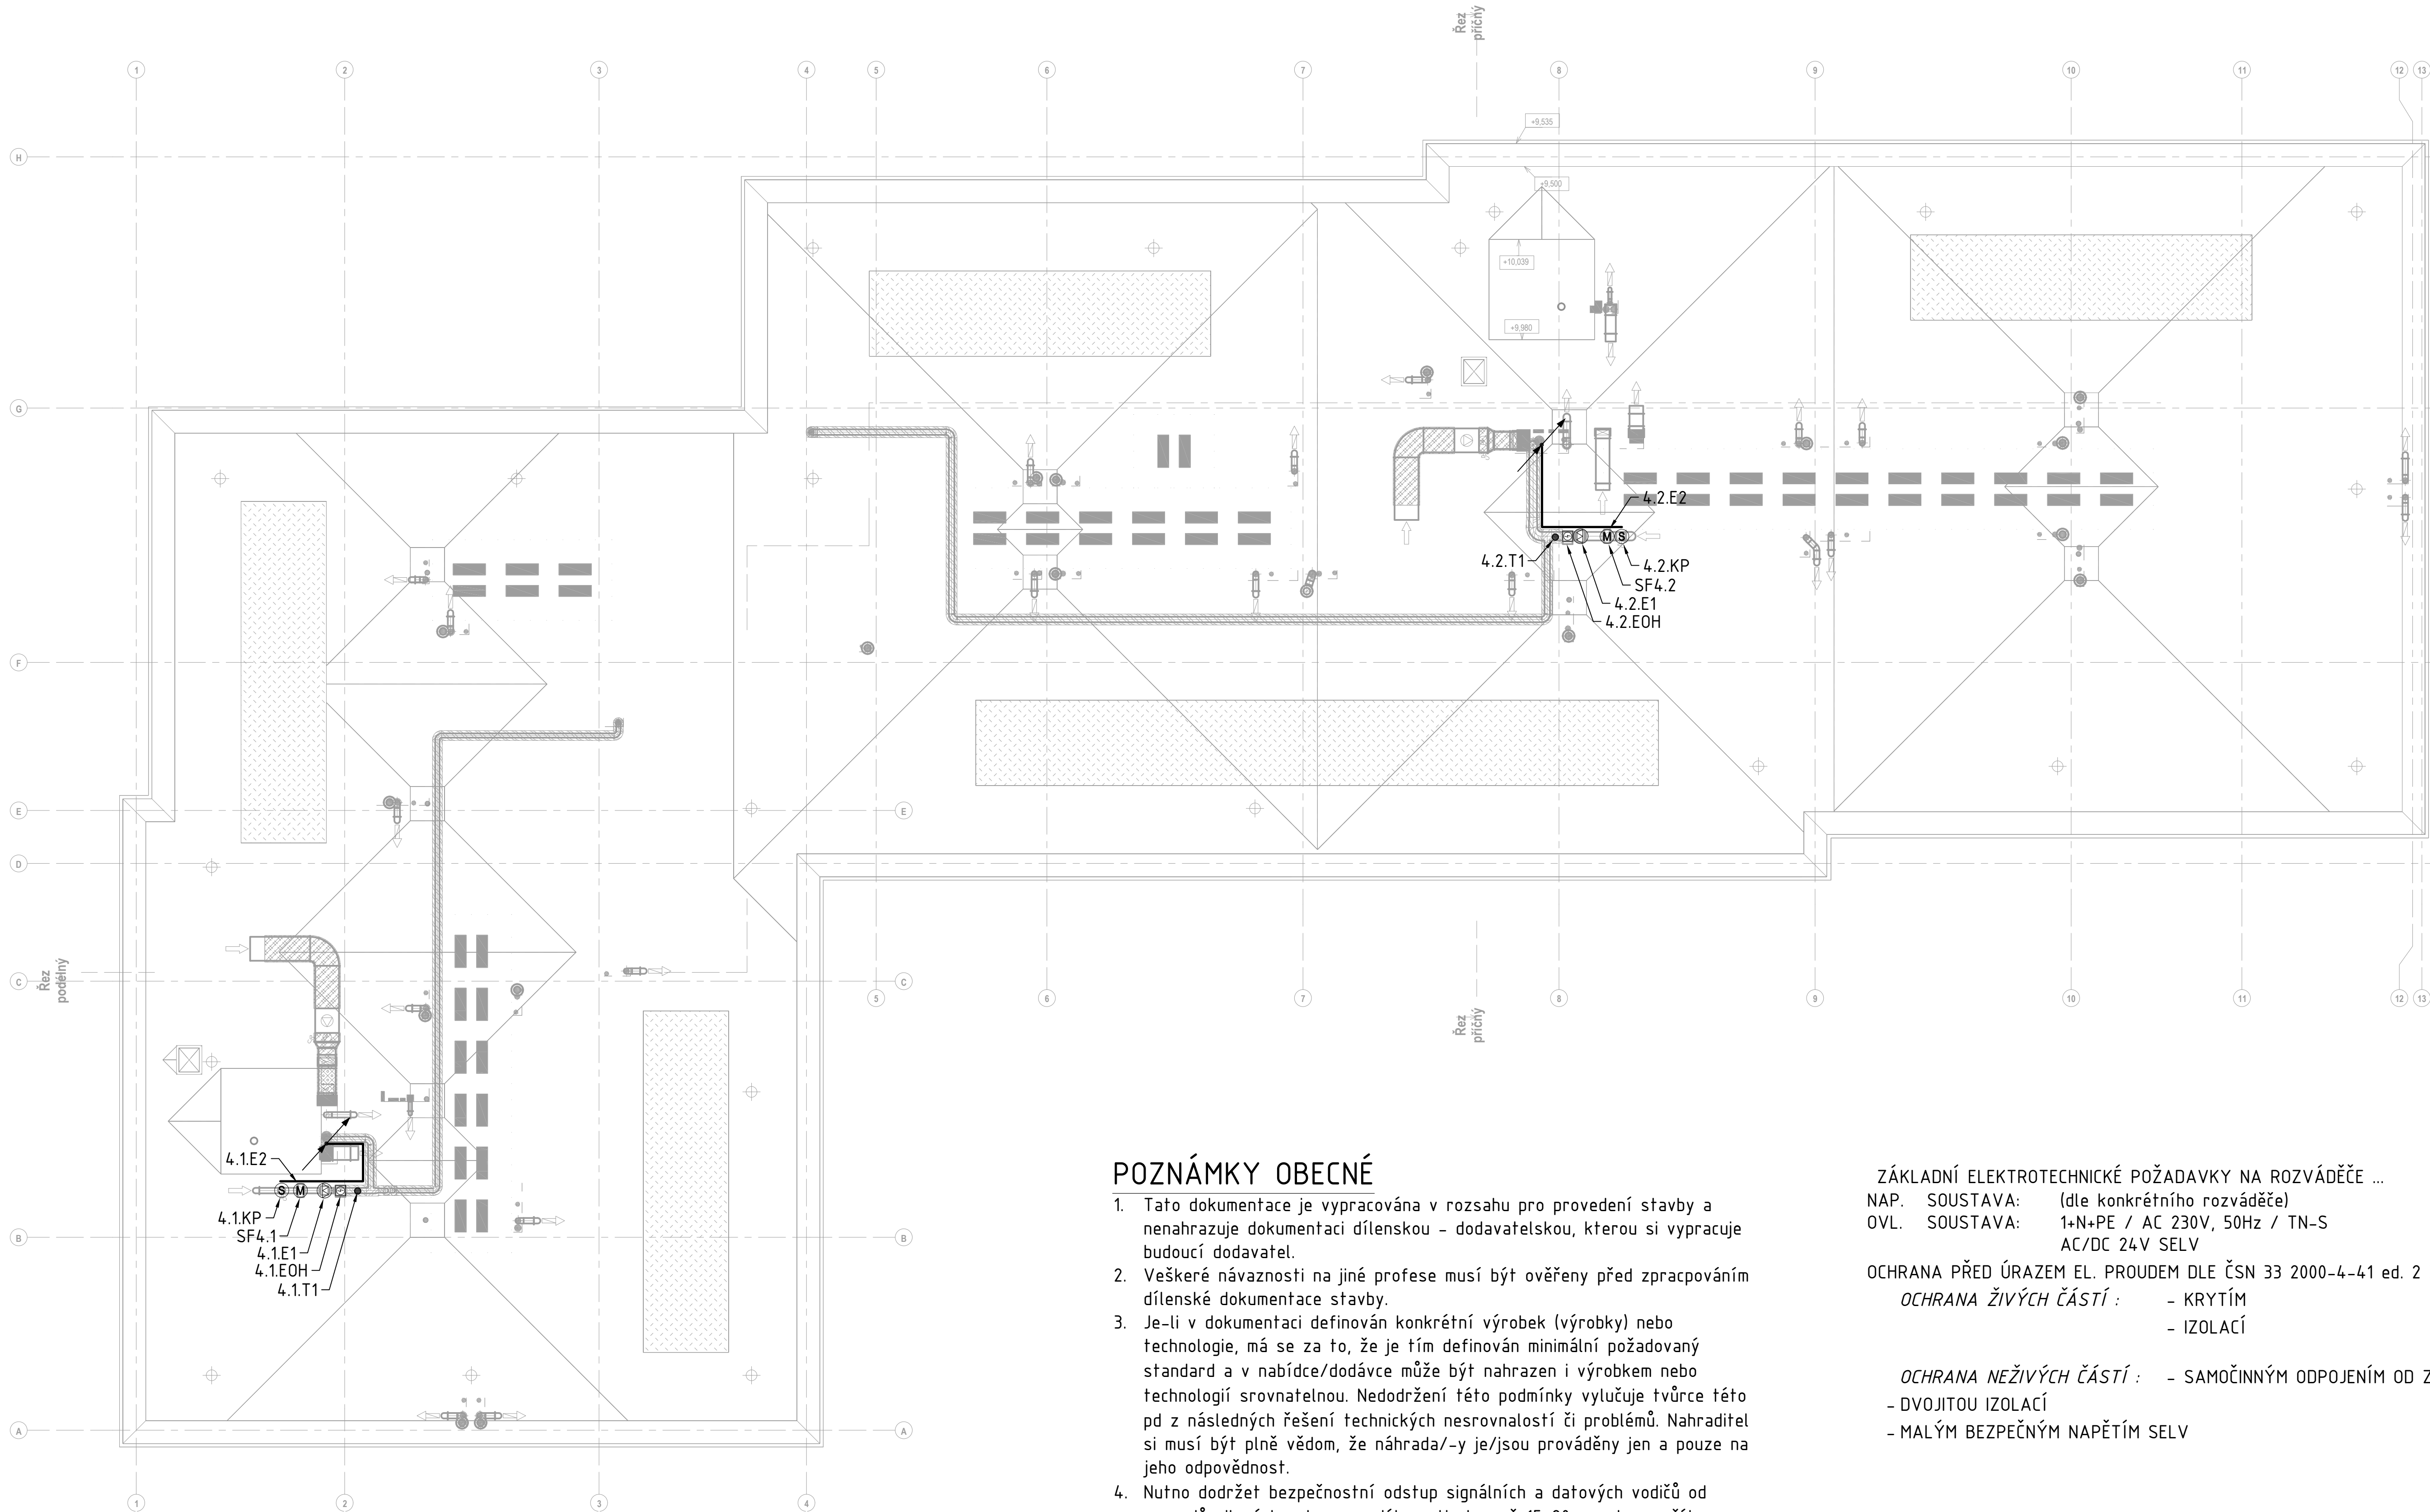

POZNÁMKY OBECNÉ

- 1. Tato dokumentace je vypracována v rozsahu pro provedení stavby a nenahrazuje dokumentaci dílenskou – dodavatelskou, kterou si vypracuje budoucí dodavatel.
- 2. Veškeré návaznosti na jiné profese musí být ověřeny před zpracováním dílenské dokumentace stavby.
- 3. Je-li v dokumentaci definován konkrétní výrobek (výrobky) nebo technologie, má se za to, že je tím definován minimální požadovaný standard a v nabídce/dodávce může být nahrazen i výrobkem nebo technologií srovnatelnou. Nedodržení této podmínky vylučuje tvůrce této pd z následných řešení technických nesrovnalostí či problémů. Nahradiatel si musí být plně vědom, že náhrada/-y je/jsou prováděny jen a pouze na jeho odpovědnost.
- 4. Nutno dodržet bezpečnostní odstup signálních a datových vodičů od rozvodů silových a to ve vzdálenosti alespoň 15-20cm nebo použít plechové kabelové kanály se stíněnými dělicími přepážkami.
- 5. Dle ČSN je nutné veškerá instalovaná zařízení vodičé pospojit zelenožlutým vodičem o minimálním průřezu 6mm2 (doporučuji realizaci koordinovat s dodavateli VZT a ELE pro určení hranic dodávek, neboť i tyto profese mají některá zařízení vodičé pospojovat).
- 6. Před uvedením do provozu je nutné provést výchozí revizi elektroinstalace, bez které není možné zařízení provozovat.
- 7. Prostupy kabelů požárně dělicími konstrukcemi požárně utěsnit – požární odolnost příslušné stavební konstrukce viz. technická zpráva PBRŠ.

ZÁKLADNÍ ELEKTROTECHNICKÉ POŽADAVKY NA ROZVÁDĚČE ...
NAP. SOUSTAVA: (dle konkrétního rozváděče)
OVL. SOUSTAVA: 1+N+PE / AC 230V, 50Hz / TN-S
AC/DC 24V SELV

OCHRANA PŘED ÚRAZEM EL. PROUDEM DLE ČSN 33 2000–4–41 ed. 2 Z1 :
OCHRANA ŽIVÝCH ČÁSTÍ : - KRYTÍM
- IZOLACÍ

OCHRANA NEŽIVÝCH ČÁSTÍ : - SAMOČINNÝM ODPOJENÍM OD ZDROJE
- DVOJITOU IZOLACÍ
- MALÝM BEZPEČNÝM NAPĚTÍM SELV


LEGENDA

- MR... ROZVÁDĚČ MĚŘENÍ A REGULACE
- M... VÝVOD PRO ELEKTRICKÝ MOTOR (VENTILÁTOR)
- S... VÝVOD PRO ELPOHON VZD. Klapky
- CO... ČIDLO DEKCE CO V GARÁŽÍCH
(montáž v nádechové výšce 1,5m nad čistotu podlahou)
- I... POKOJOVÝ PROGRAMOVATELNÝ TERMOSTAT PRO PDL VYTÁPĚNÍ
KABEL MEZI TERMOSTATEM A ROZDĚLOVAČEM PDL - CYKY-J 5x1,5
- MaR POŽÁRNÍ Klapky MONITORUJE (OTV/ZAV)
- OVLADÁ EPS (NAPÁJÍ ESI)

POZOR!!! VÝSTRAŽNÁ SVĚTELNÁ TABULE - GARÁŽE

- TAB-9.1 ... ZÁKAZ VJEZDU - NEBEZPEČÍ OTRAVY
- TAB-9.2 ... ZÁKAZ VSTUPU - NEBEZPEČÍ OTRAVY
- TAB-9.3 ... VYPNĚTE MOTOR, OPUSŤTE GARÁŽ
- H1 ... SÍŘENA 230V AC - GARÁŽE

- QT... CALORIMETR TEPLA - M-BUS
- SV... VODOMĚR STUDENÁ VODA - M-BUS
- TV... VODOMĚR TEPLÁ VODA - M-BUS
- EM... ELEKTROMĚR - M-BUS

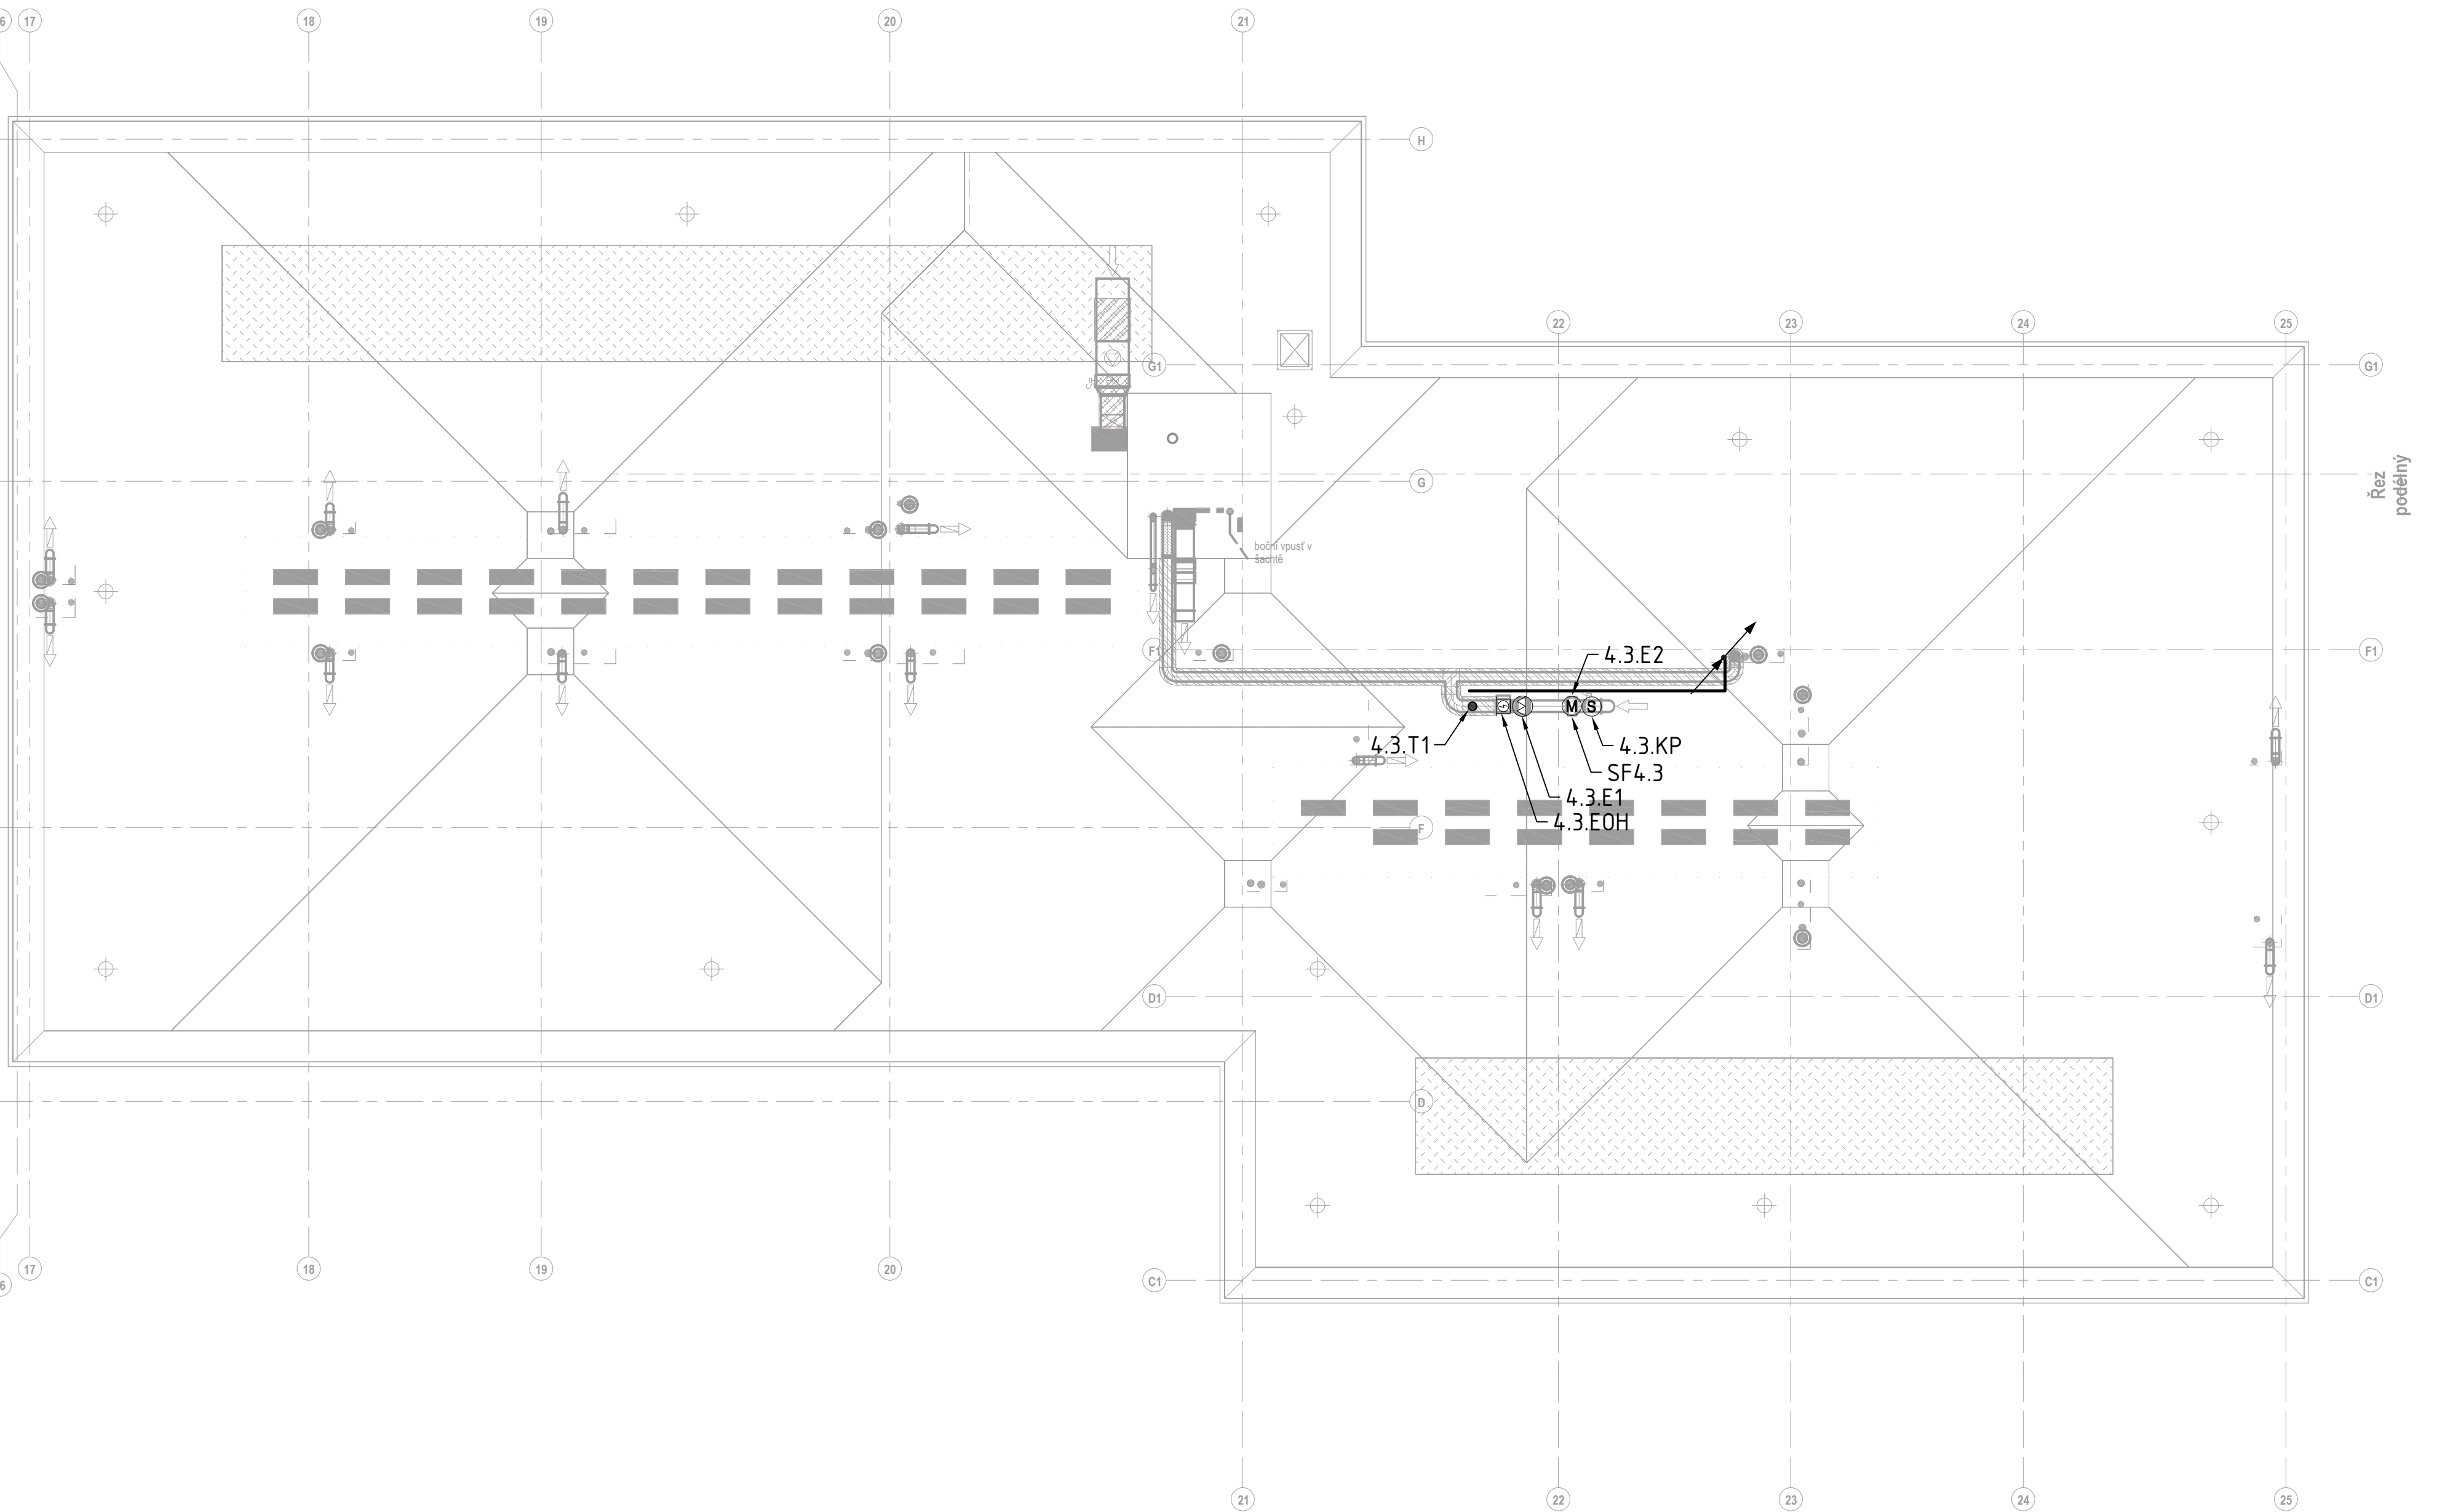

Revize

Popis revize

Datum

sever

stavba

BD Na Mariánské cestě - 2. etapa

zpracoval

zodpovědný projektant

Ing. Jiří Pavlovský

vypracoval

Radek Hak

MINET ELEKTRO, spol. s r.o.

Pražská 810/16, 102 21 Praha 10

Česká Republika

T: +420 281 017 299

www.minet-elektro.cz

Investor

DOMORLAN s.r.o.

Trnitá 543/16, Brno, 602 00

generální projektant

BK engineering projekt s.r.o.

Hranovice 347/16

140 03 Praha 4

info@bupard.cz

hlavní inženýr projektu

Ing. Libor Doležal

± 0,000 = 224,62 m.n.m (BPV)

stavba

Dokumentace pro provádění stavby

stavění objektu

SO03 - Bytový dům D2 a C2

část

D.1.2 Technika prostředí staveb

prohnutí dle / členění část

D.1.2.8 Měření a regulace

datum

11/2025

x A4

14

mřížka

1:100

zákazka

365

etapa

50

s.objekt

SO03

část

D.1.2

členění

08

č. výkresu

104

revize

PŮDORYS STŘECHY